


CODE	AANTAL	PAALTYPE (mm.)	LENGTE (m.)	INHEINIVO tov. NAP
	21	beton vierkant 250	4.5	4.00 & 4.25 m -

Maatvoering:
Maten in mm.
Peil = 0.000
Hoogtematen in mm. tov. Peil

1 - 359 KN Paalnummer-Paalbelasting (rekenwaarde)




Sondering nr. 1

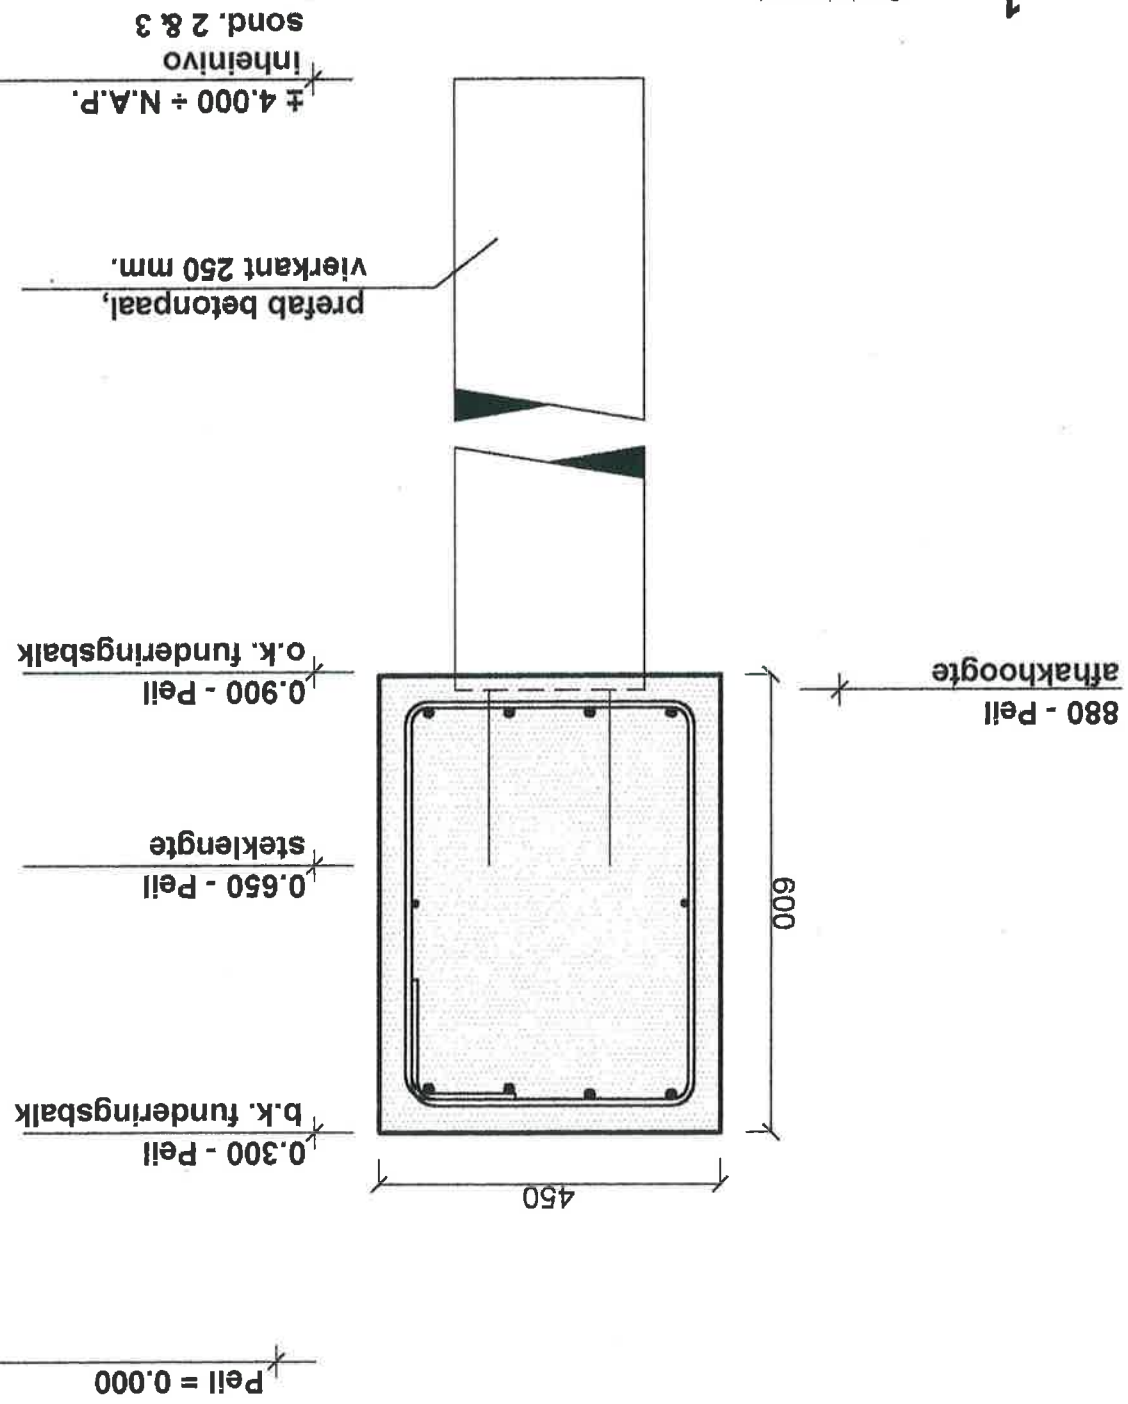

project	Bijeenkomstgebouw "Haci Bayram"
elgenaar	De heer S. Bozkurt
adres	Leeuwerik 80
plaats	3752 NJ BUNSCHOTEN-SPAKENBURG
telefoon	033-2987603 (2988061, M. Öztürk)
onderdeel	RENVOOI + DETAILS PALENPLAN
schaal	1:10
format	A3
datum	28 oktober 2003

projectnummer	A-109498
tek. nummer	1
W1jz. A:	W1jz. G:
W1jz. B:	W1jz. H:
W1jz. C:	W1jz. I:
W1jz. D:	W1jz. J:
W1jz. E:	W1jz. K:
W1jz. F:	W1jz. L:

ALLE MAATVOERING IN HET WERK TE KONTROLEREN!!!


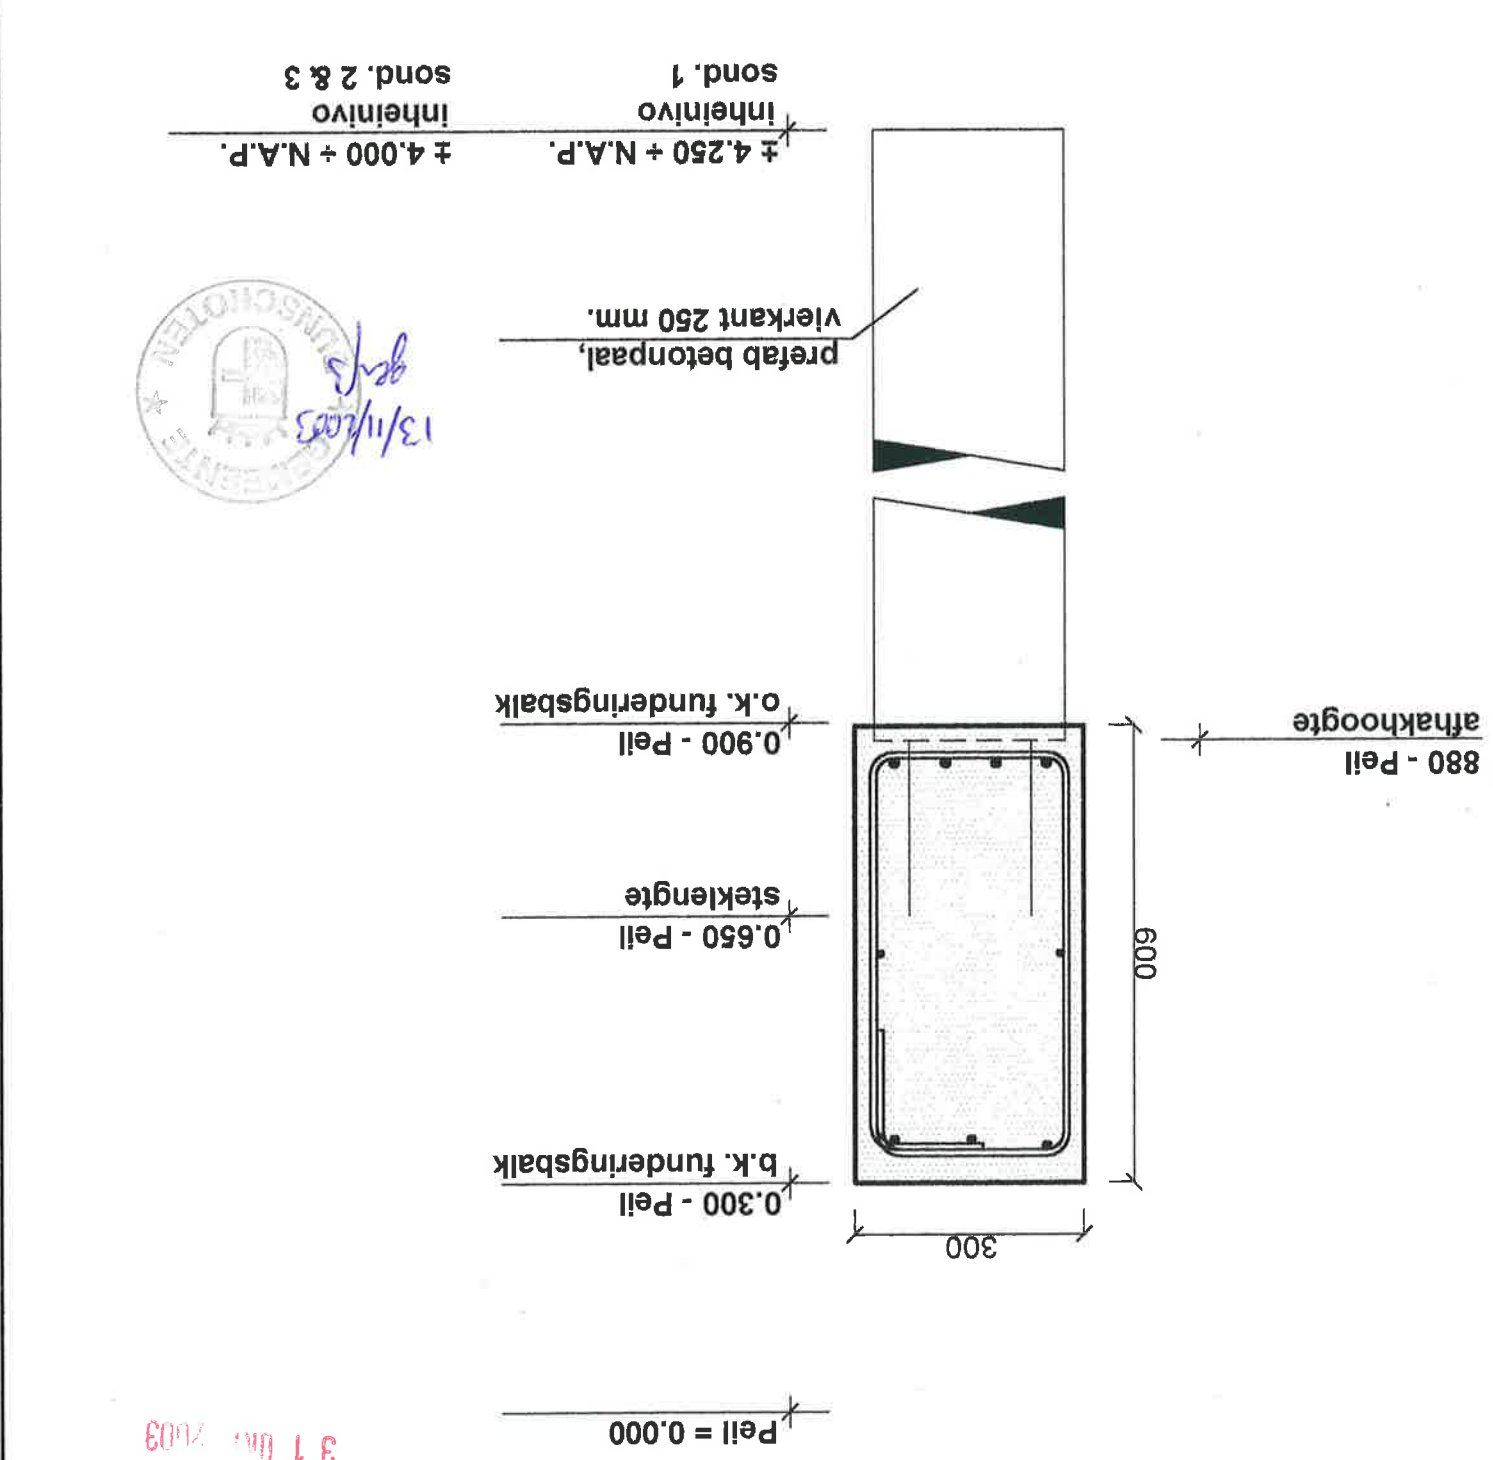


3 1 okt 2003

Niets van deze tekening mag worden vervaelvoudigd, opgeslagen in een geautomatiseerd gegevensbestand, of openbaar gemaakt in enige vorm of op enige wijze, hetzij elektronisch, mechanisch, door fotokopieën, opnamen, of op andere wijze, zonder voorafgaande schriftelijke toestemming van de ontwerper, op grond van artikel 17b en 17c Auteurswet 1912.



onderdeel OVERZICHT DAK schaal 1:100/ 1:10 format A3 datum 28 oktober 2003		projektnummer A-109498 tek. nummer 10 Wtjz. A1 Wtjz. B1
---	--	---

Oplegging ligger 1 & 2

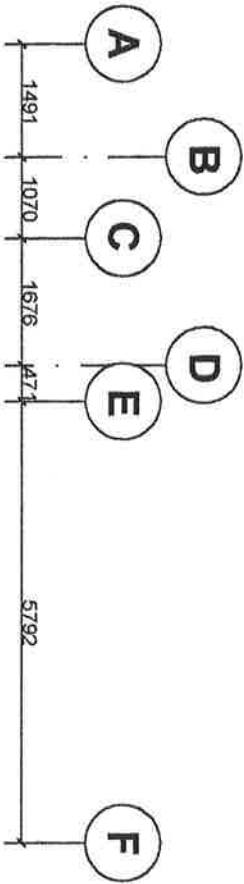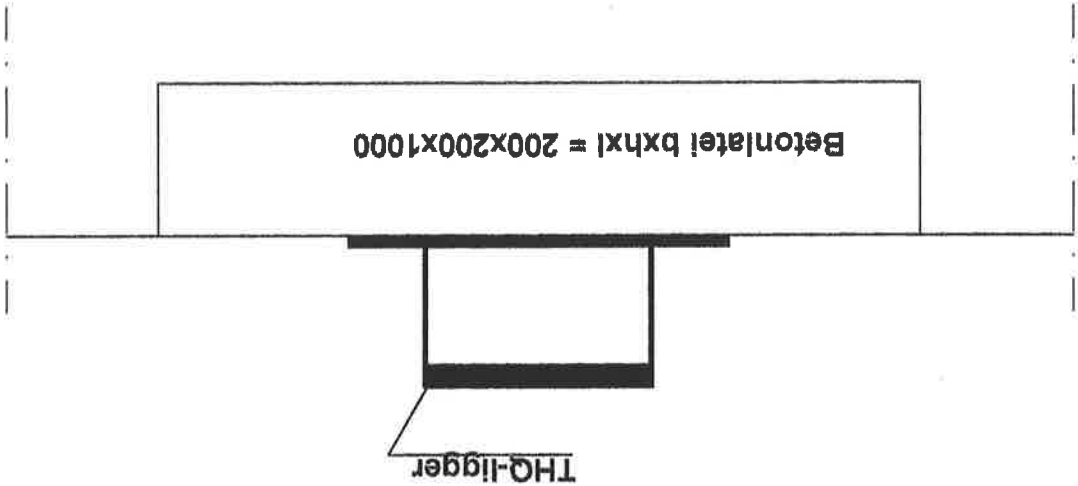


Gasbeton dakplaten, dik 200 mm
type GB4/600.

Ligger 1---THQ 200.5-290.30-500.20; loog 25 mm.
Ligger 2---THQ 200.5-290.30-500.20; loog 15 mm.
Ligger 3---THQ 200.5-290.30-500.20

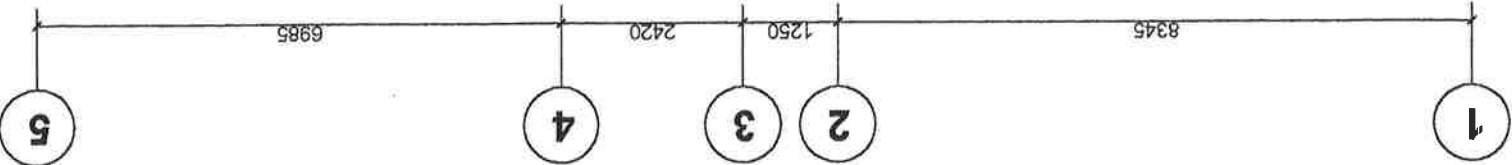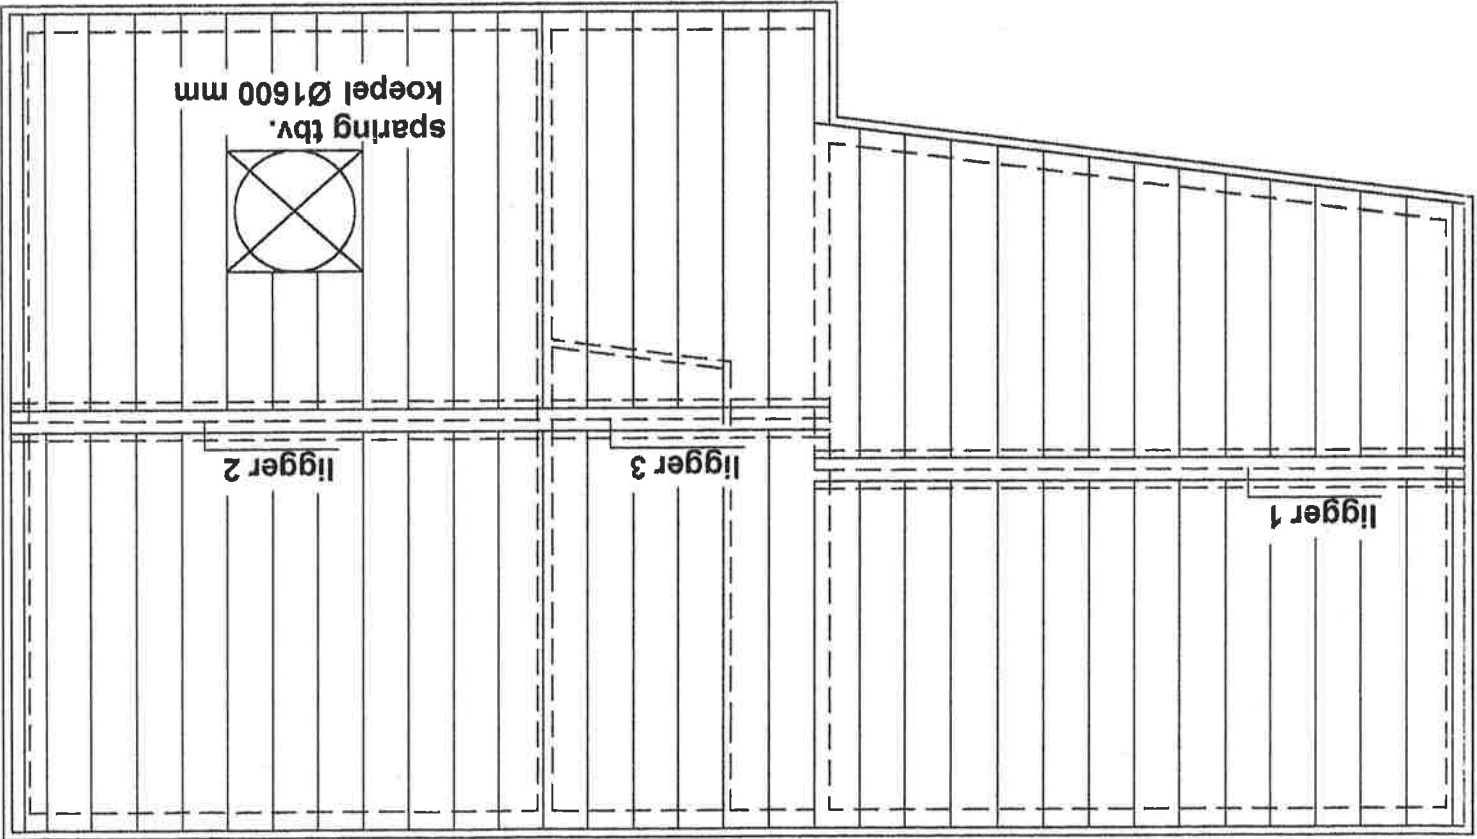


onderdeel : PALENPLAN		datum : 28 oktober 2003	
schaal : 1:100		format : A3	
projektnummer : A-109498		teek. nummer : 2	
Wzjg. A:		Wzjg. B:	

1/1 c

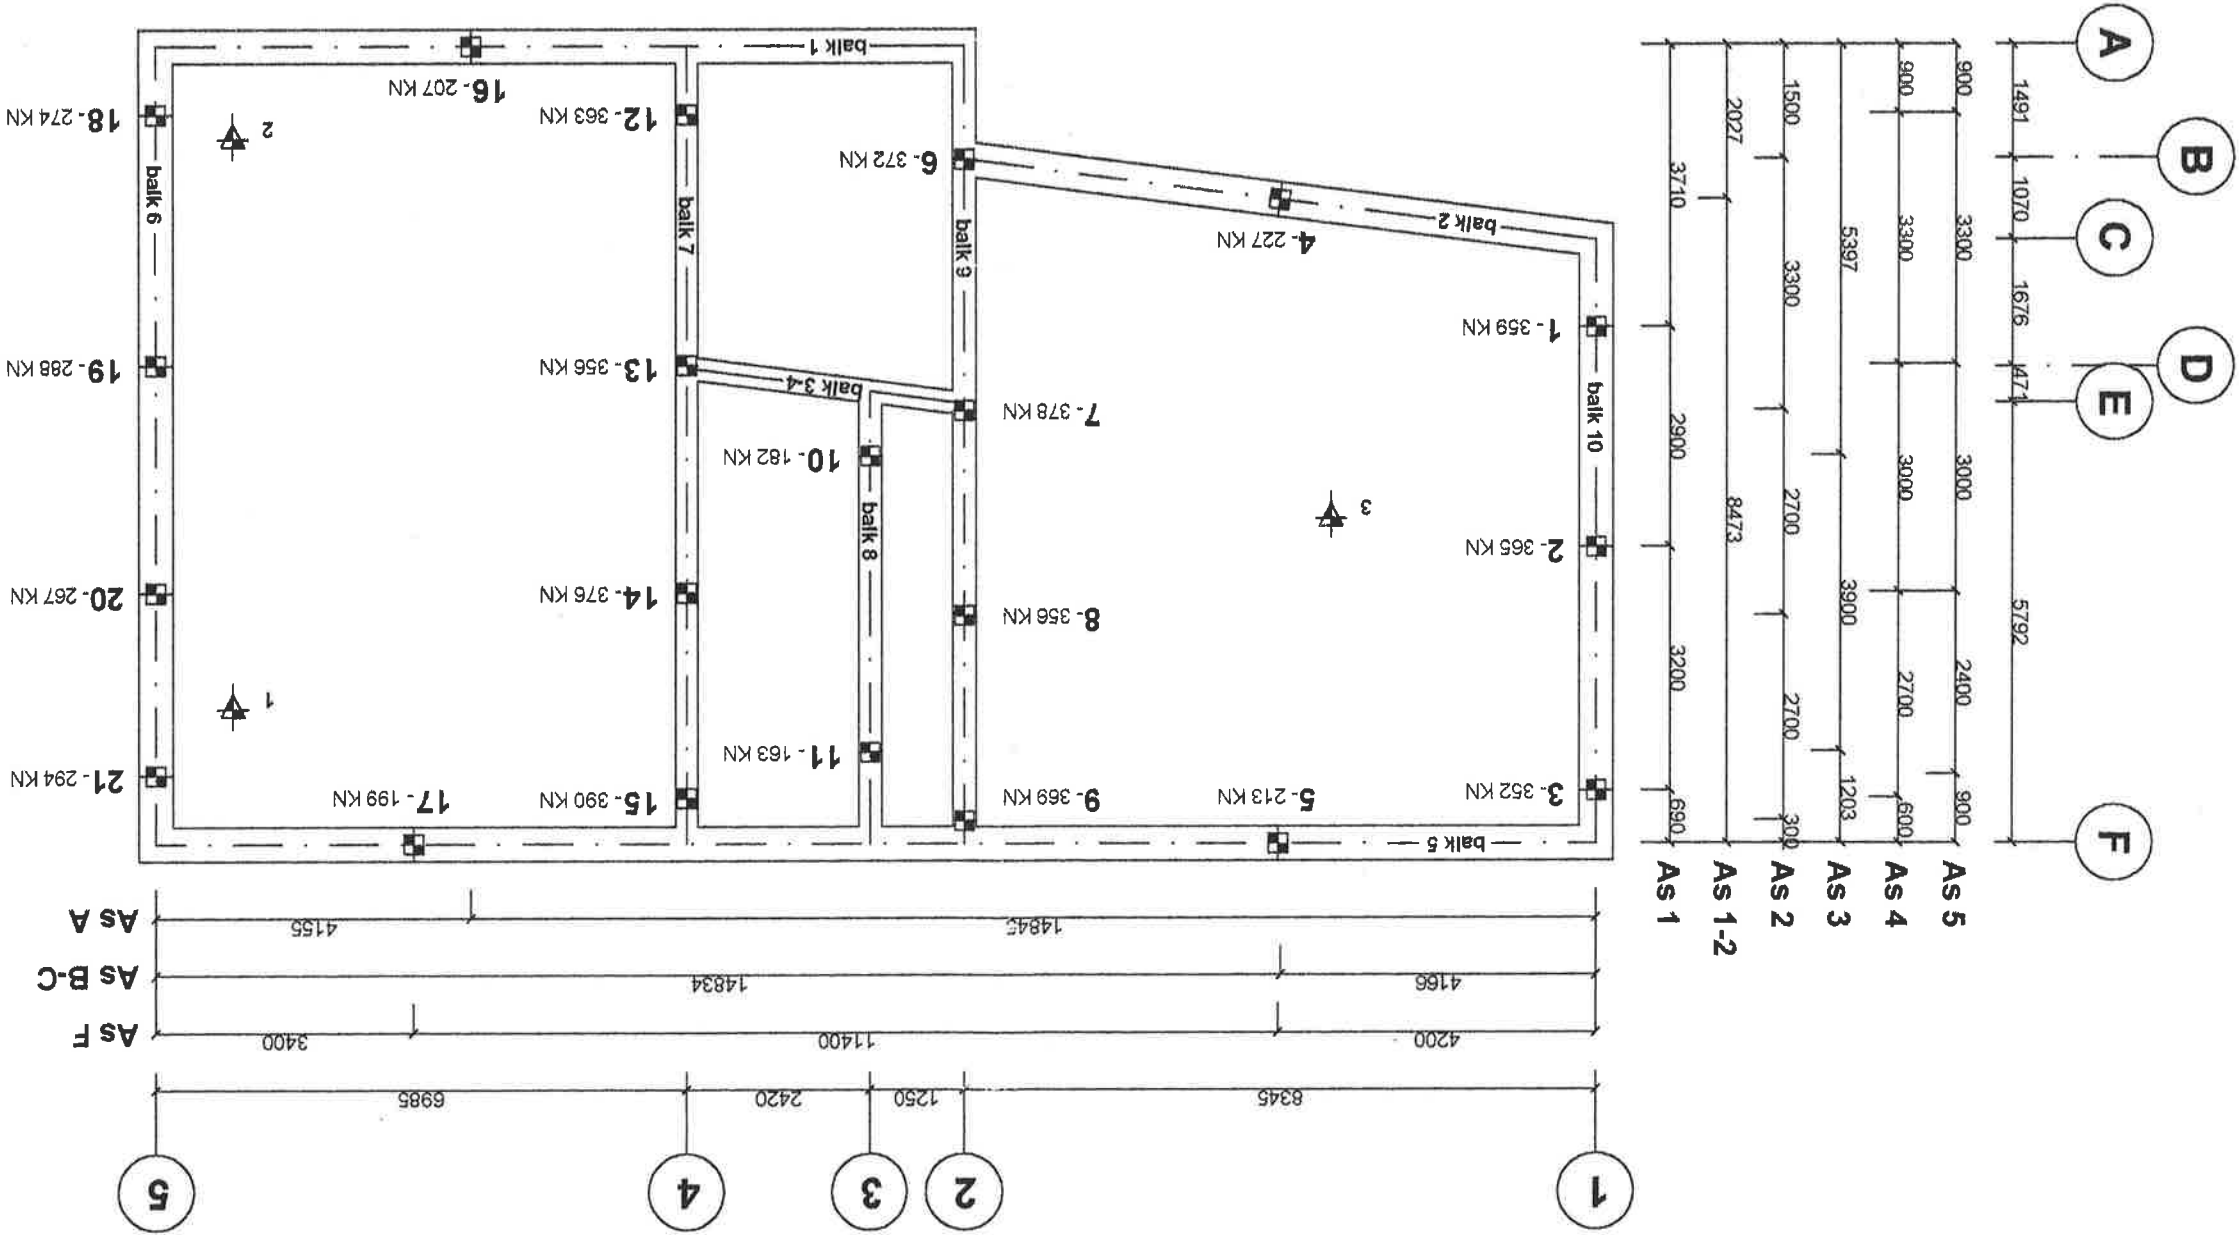


Voorschriften Beton VBT 1995:	
Betonstaal:	FEB500 HWL
Staven:	FEB500 HKN
Netten:	FEB500 HKN
Vloeren en wanden:	
Beton:	Sterkteklasse : B25 Milieuklasse : 2 Consistentiegebied : 2 Dekking : 25 mm. Oncontroleerbaar : +5 mm.
Minimale laslengten betonstaal in mm.	vervolg:
Diameter: Ø11	Onder: 400 mm. Boven: 500 mm.
Diameter: Ø7	Onder: 300 mm. Boven: 300 mm.
Diameter: Ø9	Onder: 350 mm. Boven: 400 mm.
Diameter: Ø10	Onder: 400 mm. Boven: 450 mm.
Balken (bxh): 300x600 mm² & 450x600 mm²	
Beton:	Sterkteklasse : B25 Milieuklasse : 2 Consistentiegebied : 2 Dekking : 35 mm. Oncontroleerbaar : +5 mm.
Minimale laslengten betonstaal in mm.	vervolg:
Diameter: Ø16	Onder: 650 mm. Boven: 800 mm.
Diameter: Ø20	Onder: 850 mm. Boven: 1050 mm.
Maatvoering:	
Maten in mm. Peil = 0.000 Hoogtematen in mm, t.o.v. Peil	


1, 2 & 5
DRSN. BALK

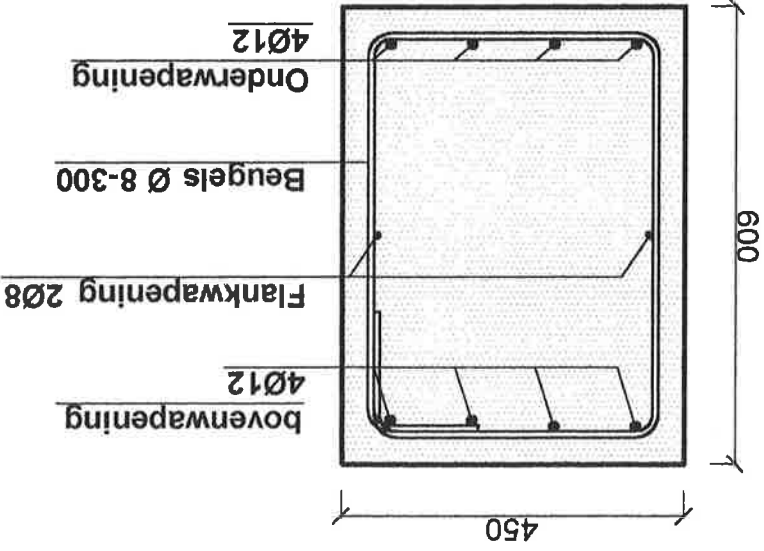


6 & 10
DRSN. BALK

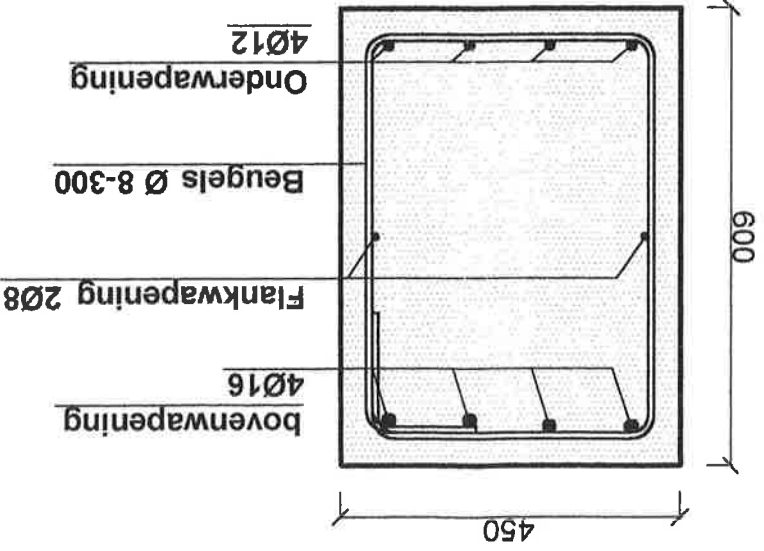


3-4 & 8
DRSN. BALK

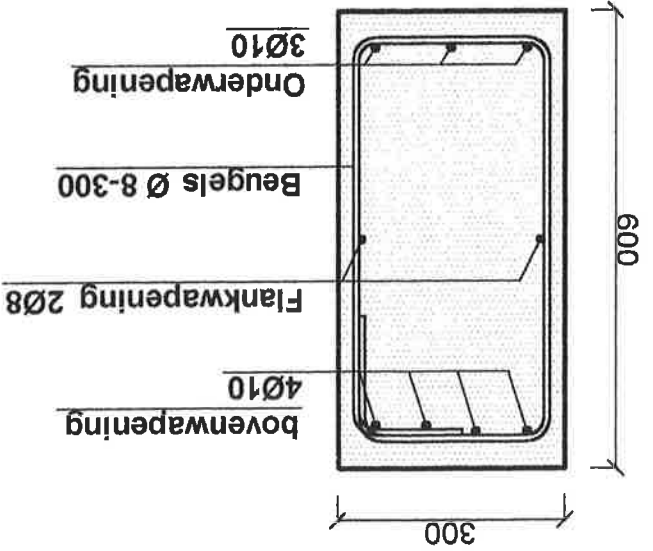


7 & 9
DRSN. BALK

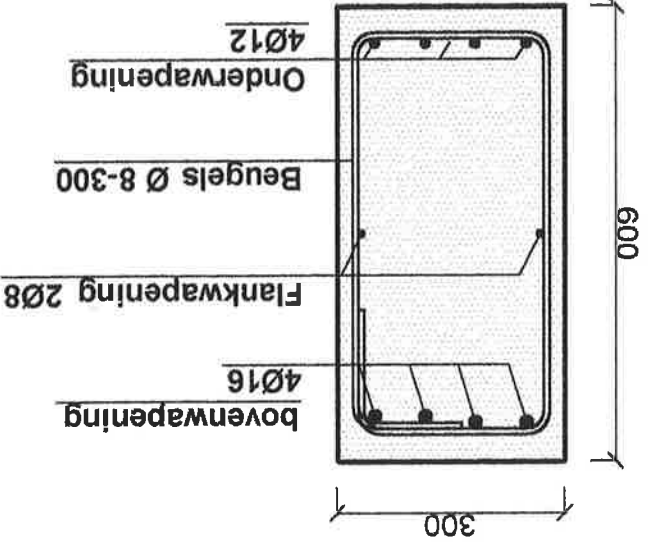

onderdeel : RENVOL + DETAILS FUNDERING schaal : 1:10 format : A3 datum : 28 oktober 2003	projectnummer : A-109498 tek. nummer : 3 wijz. A: wijz. B:
---	---

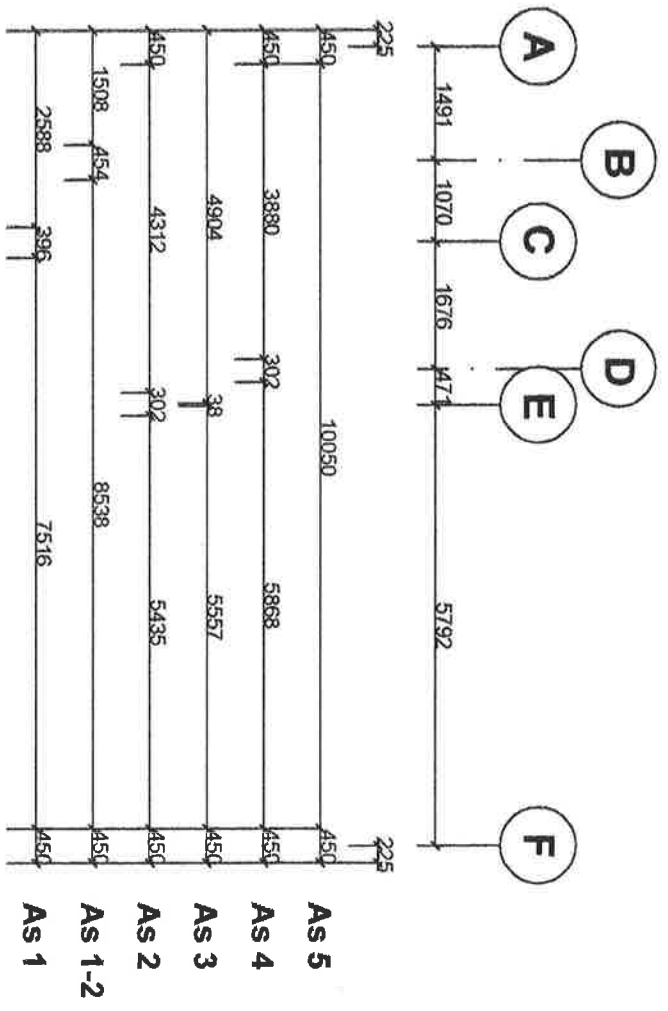


Algemeen betonbalken
balk 1, 2, 5, 6 & 10 bxxh= 450x600 mm.
balk 3, 4, 7, 8 & 9 bxxh= 300x600 mm.
bovenwapening zie detail,
onderwapening zie detail,
flankwaping 2Ø8
beugels Ø8-300,
Voor bijlegwapening en extra beugels, zie overzicht funderingsplan.

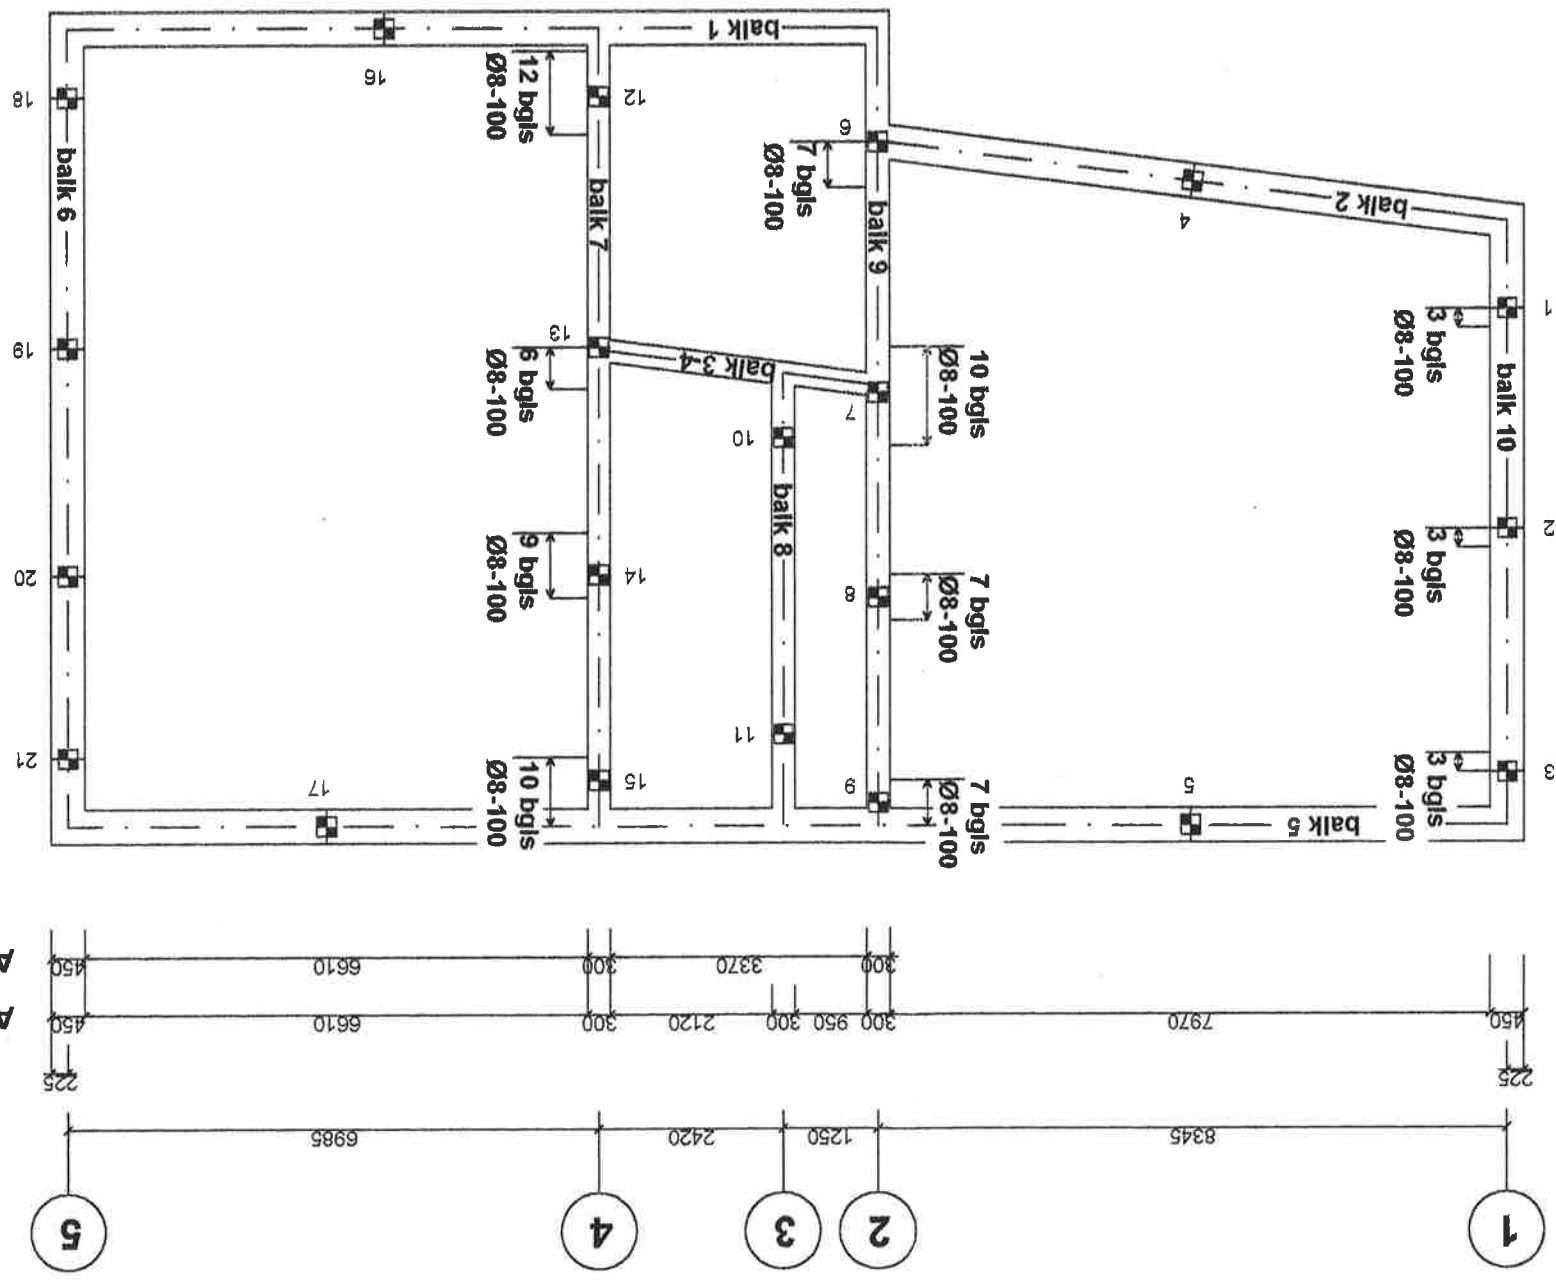


onderdeel : FUNDERINGSPLAN		schaal : 1:100		formaat : A3		datum : 28 oktober 2003	
projectnummer : A-109498		tek. nummer : 4		Wtjw. A:		Wtjw. B:	

WAPENING BALK 1, 2 & 5 : 1:50 : A3 : 28 oktober 2003		Wtjg. A: : 5
Wtjg. B: : A-109498		Wtjg. C: : 5


BALK 5

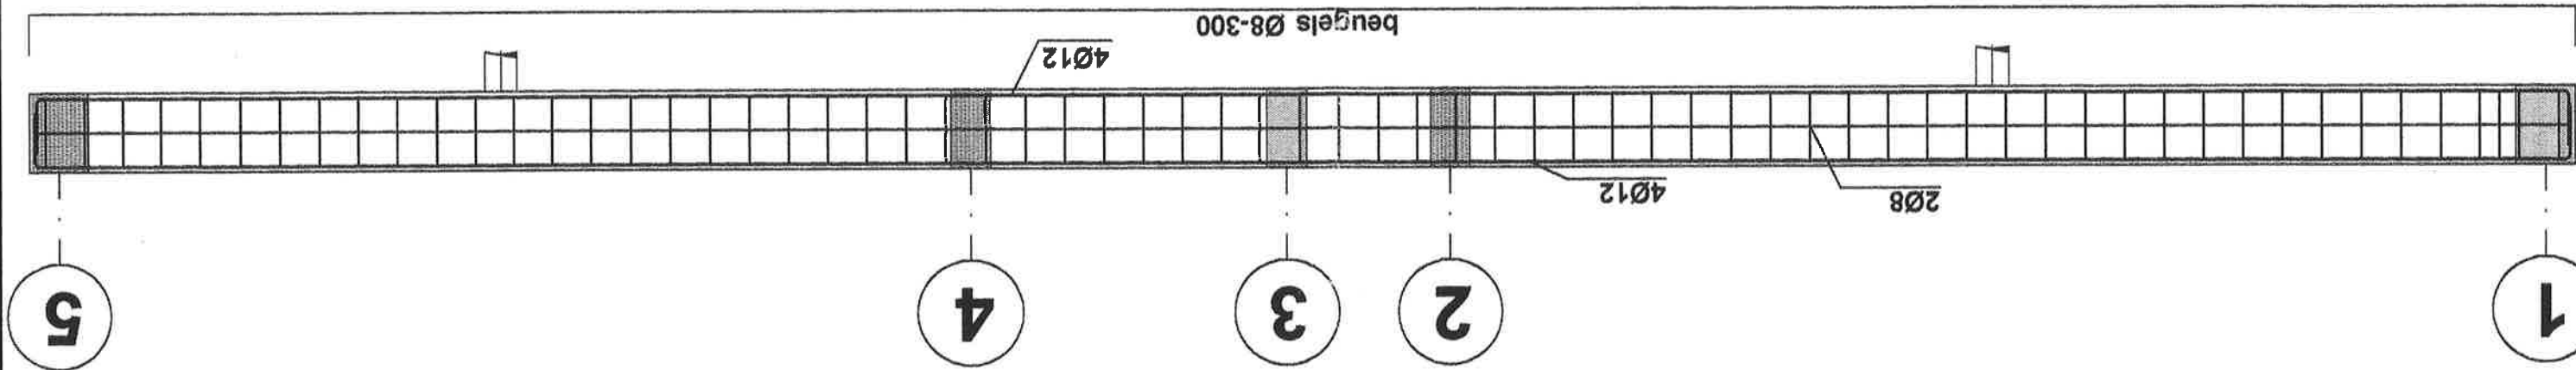


BALK 2

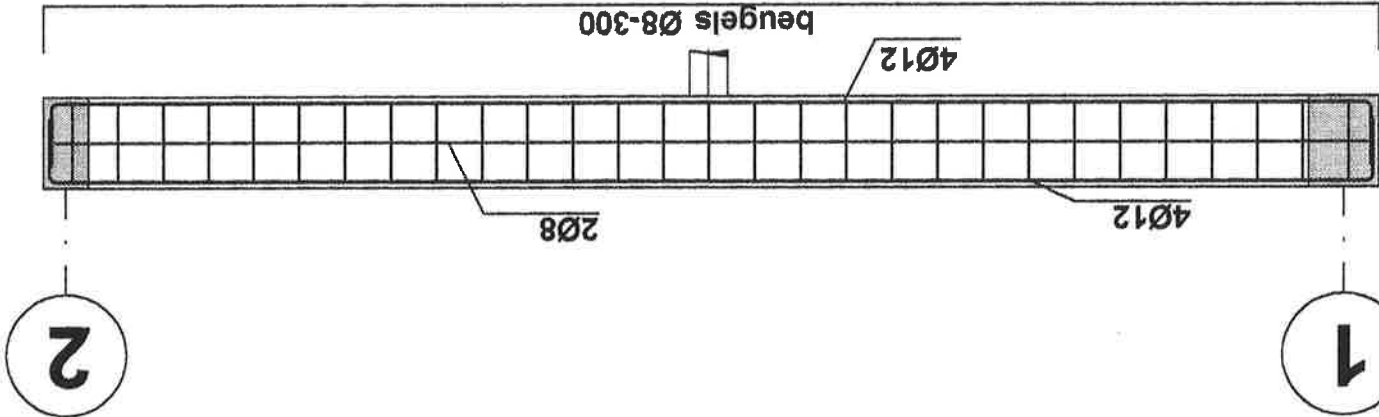


BALK 1

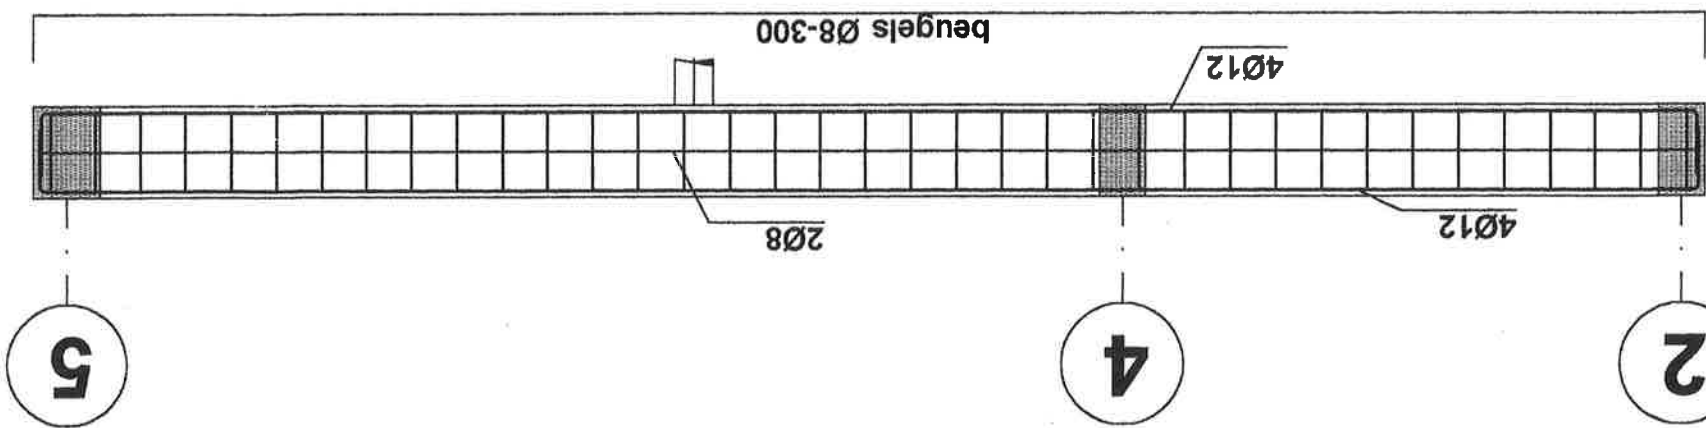





WAPENING BALK 6 & 10 : 1:50 : A3 : 28 oktober 2003		datum : 28 oktober 2003
WAPENING BALK 6 & 10 : 1:50 : A3 : 28 oktober 2003		format : A3
WAPENING BALK 6 & 10 : 1:50 : A3 : 28 oktober 2003		schaal : 1:50
WAPENING BALK 6 & 10 : 1:50 : A3 : 28 oktober 2003		onderdeel : WAPENING BALK 6 & 10
projectnummer : A-109498	tek. nummer : 6	Wtje. A : Wtje. B :

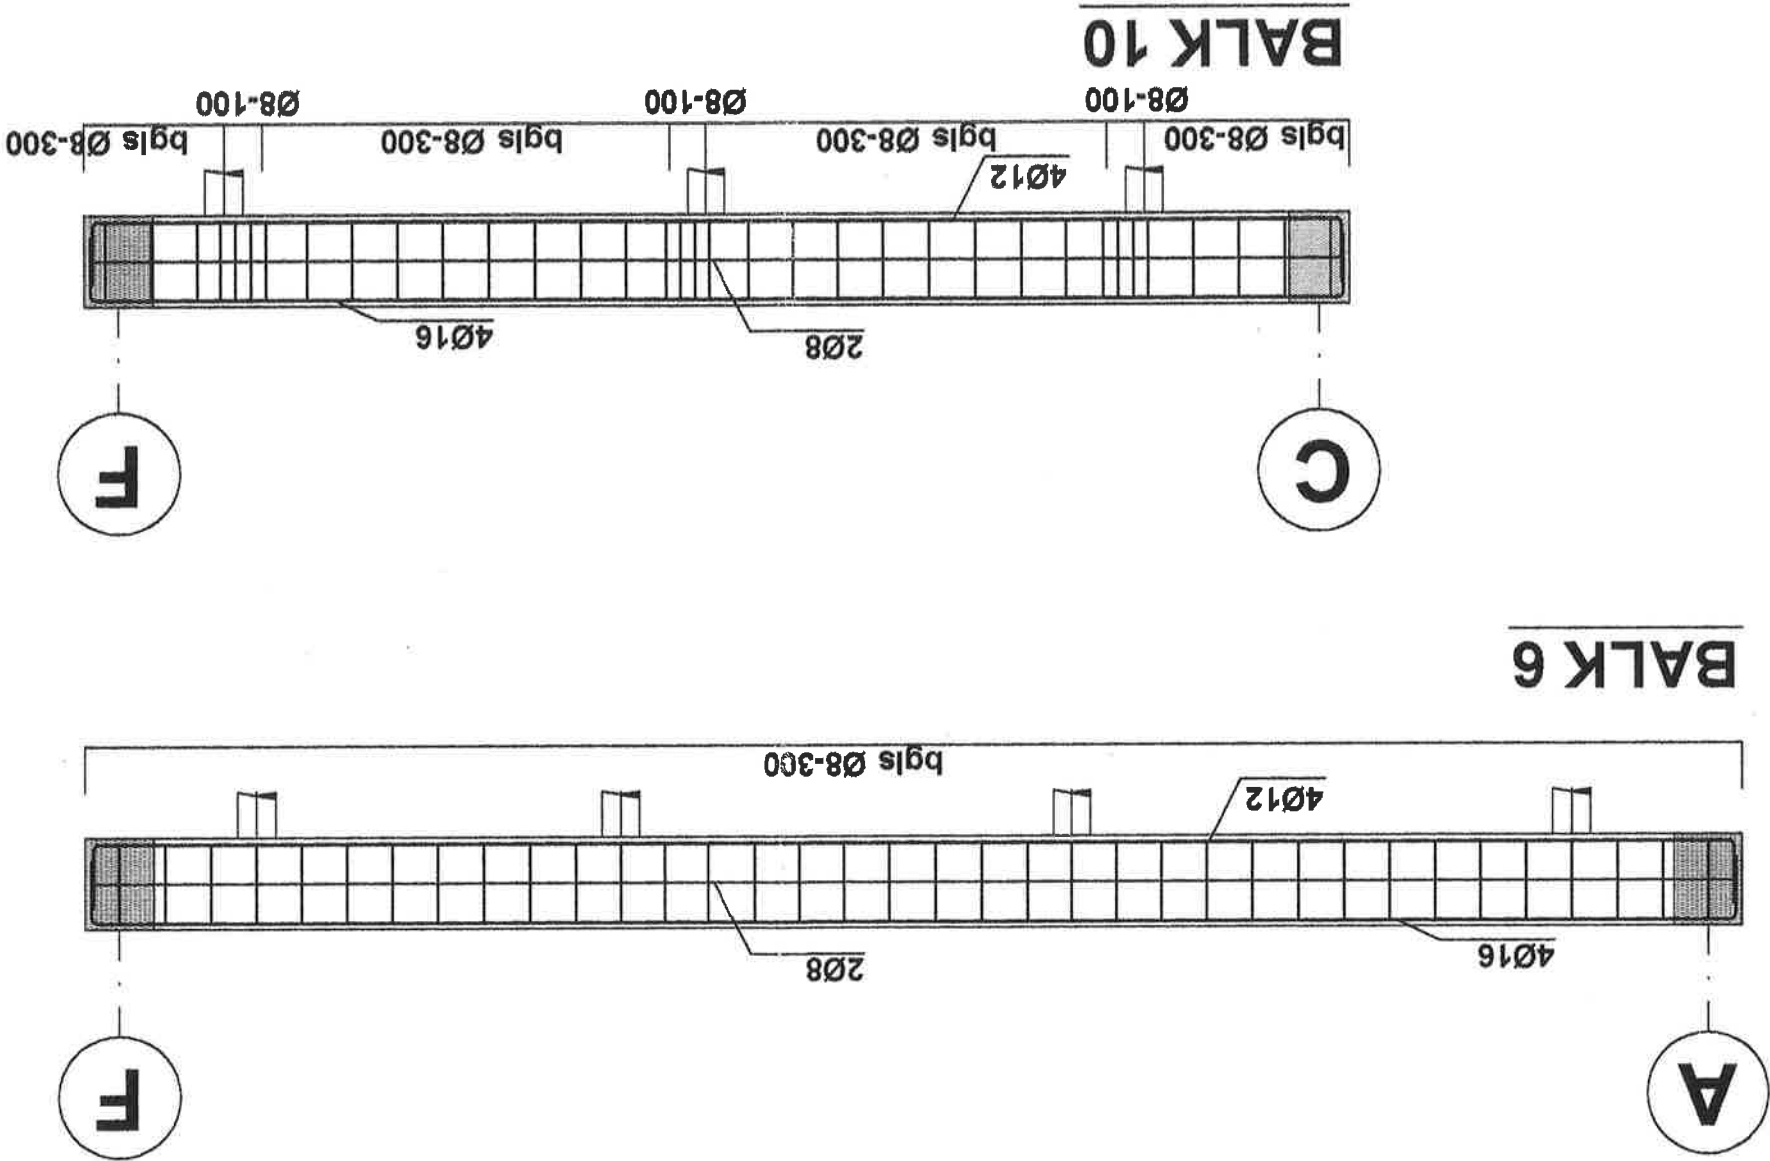

: WAPENING BALK 3-4, 7, 8 & 9 : 1:50 : A3 : 28 oktober 2003		: datum
: WAPENING BALK 3-4, 7, 8 & 9 : 1:50 : A3 : 28 oktober 2003		: schaal : 1:50 : A3
: WAPENING BALK 3-4, 7, 8 & 9 : 1:50 : A3 : 28 oktober 2003		: formaat : A3 : 28 oktober 2003
: WAPENING BALK 3-4, 7, 8 & 9 : 1:50 : A3 : 28 oktober 2003		: Wapen. A: : Wapen. B:
: WAPENING BALK 3-4, 7, 8 & 9 : 1:50 : A3 : 28 oktober 2003		: tek. nummer : 7
: WAPENING BALK 3-4, 7, 8 & 9 : 1:50 : A3 : 28 oktober 2003		: projectnummer : A-109498



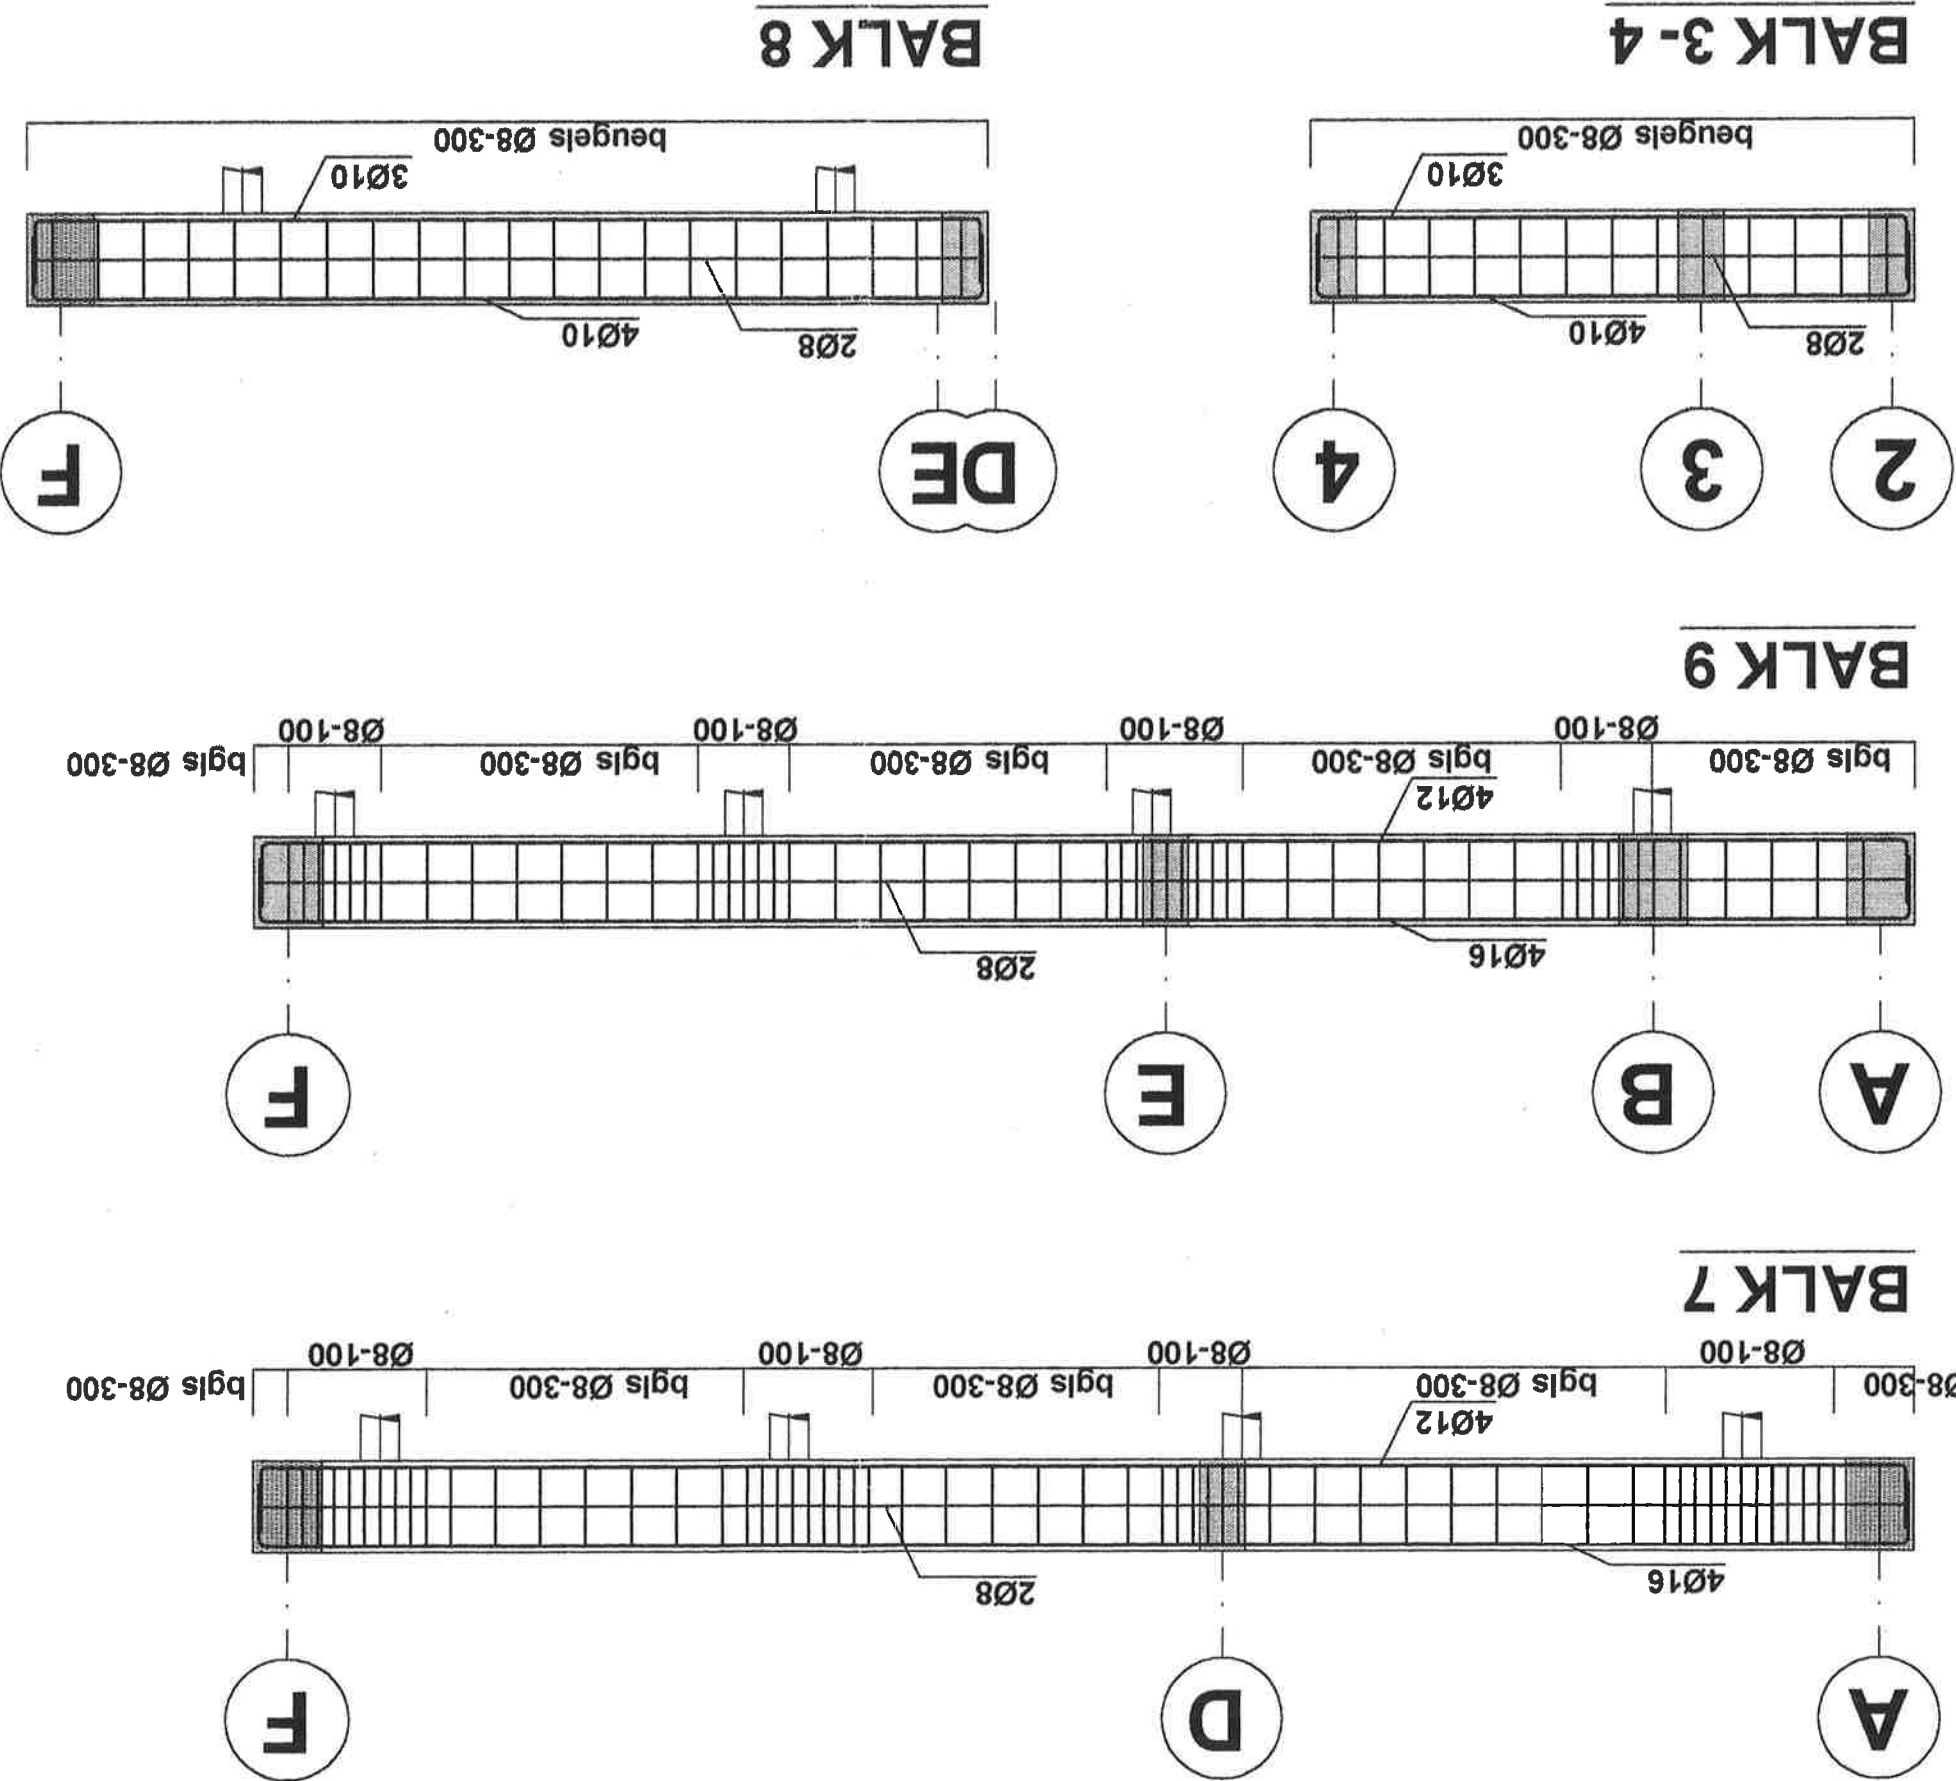


Detail kolomvoet

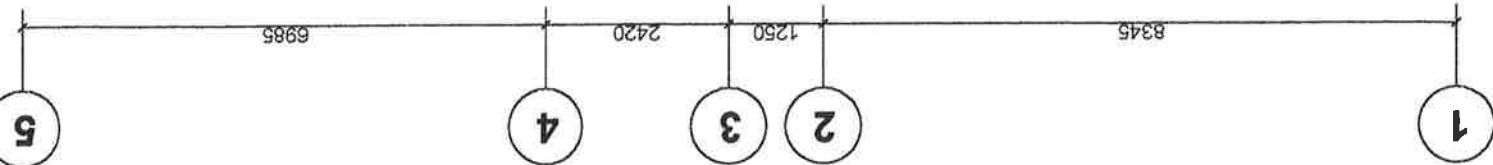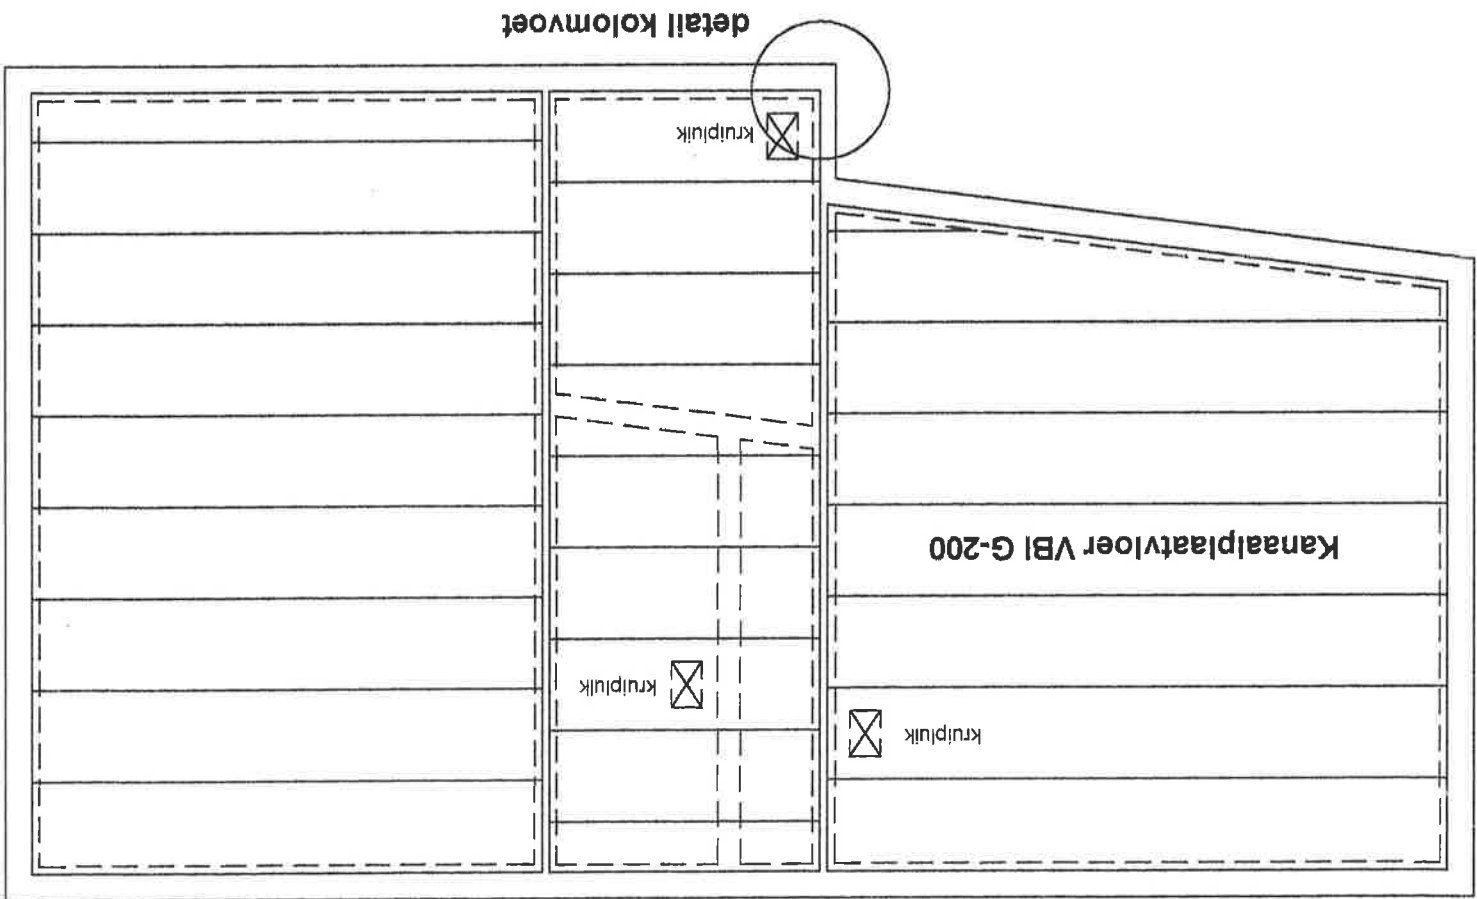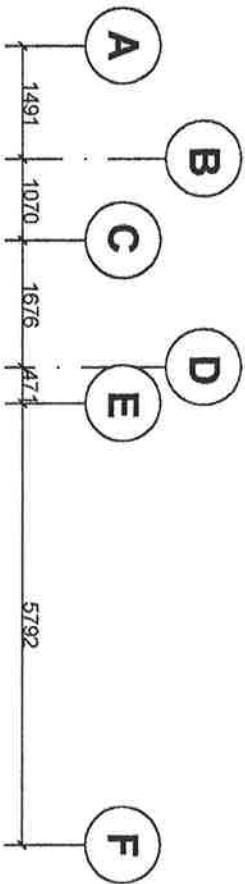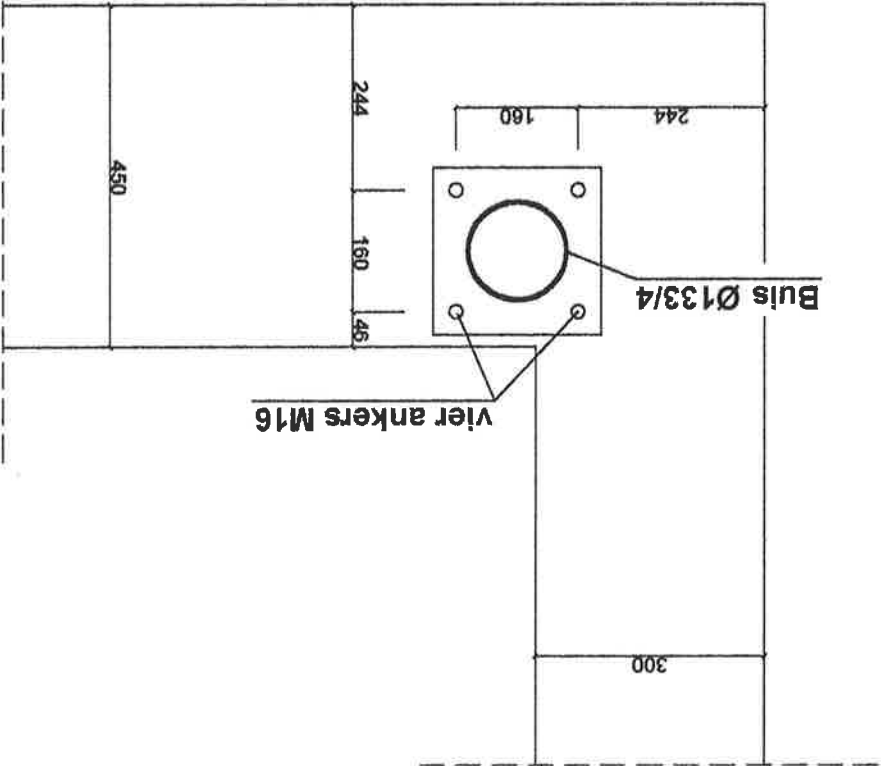

onderdeel	: OVERZICHT BEGANE GROND
schaal	: 1:100/ 1:10
format	: A3
datum	: 28 oktober 2003
proj. nummer	: A-109498
teek. nummer	: 8
Wtjz. A:	
Wtjz. B:	

Bovenaanzicht HEA200 met
kolom Ø133/4

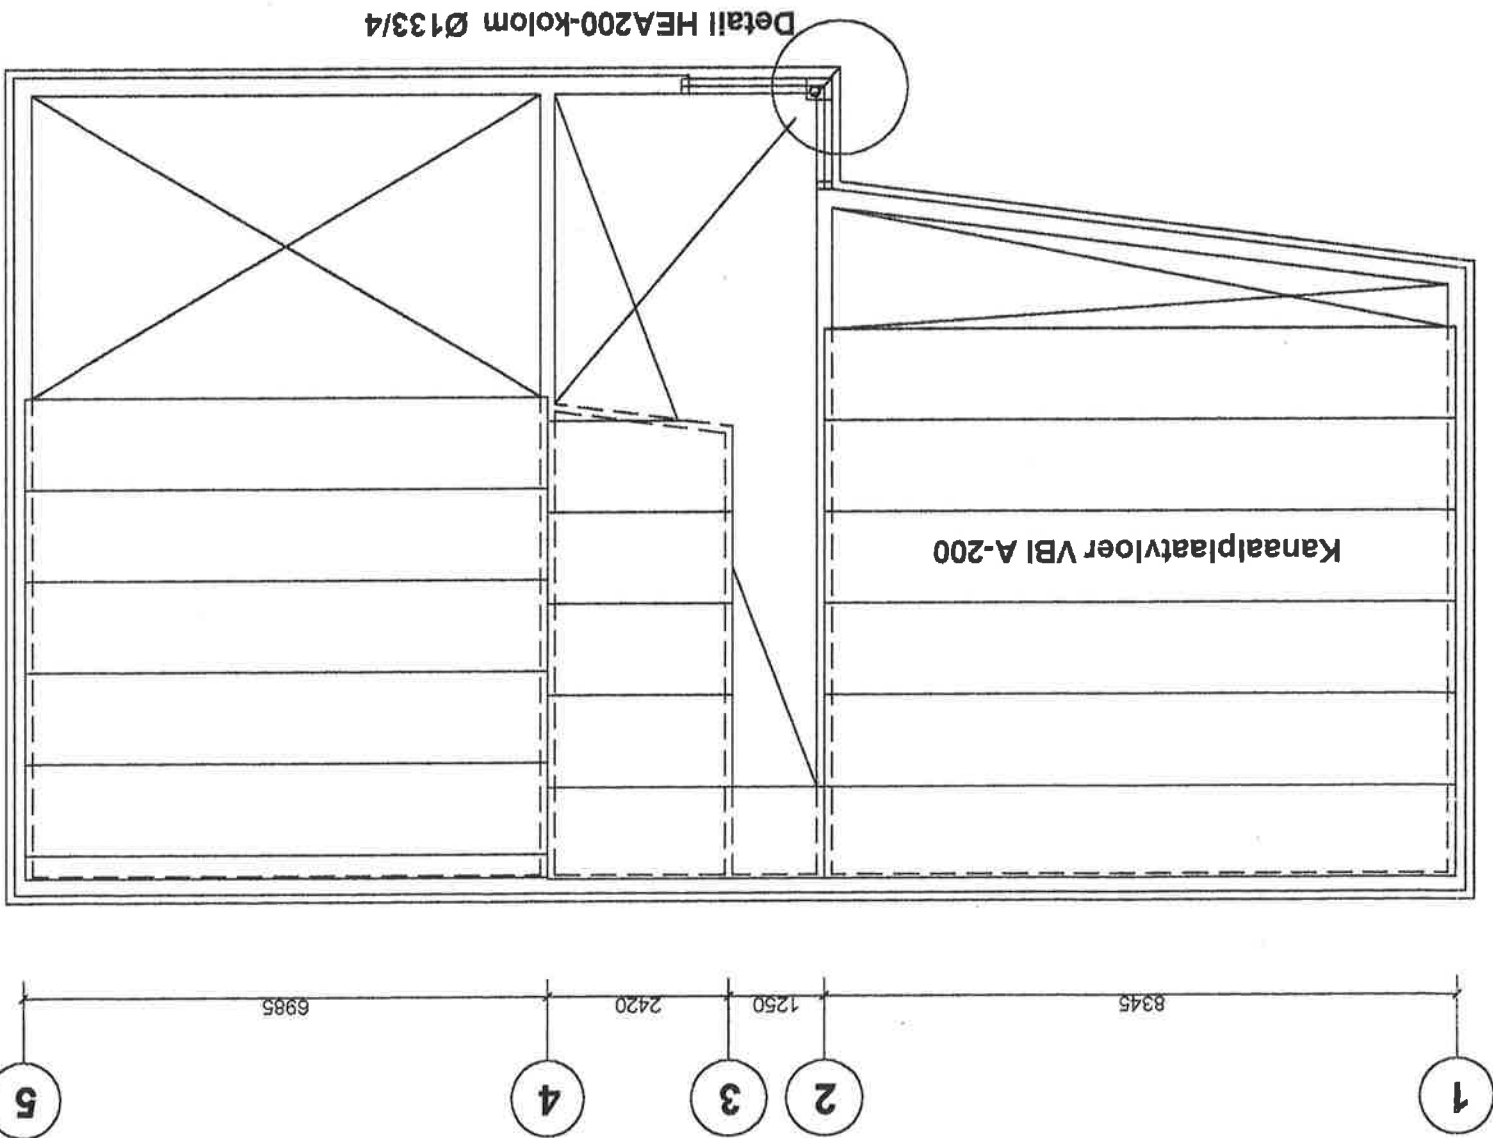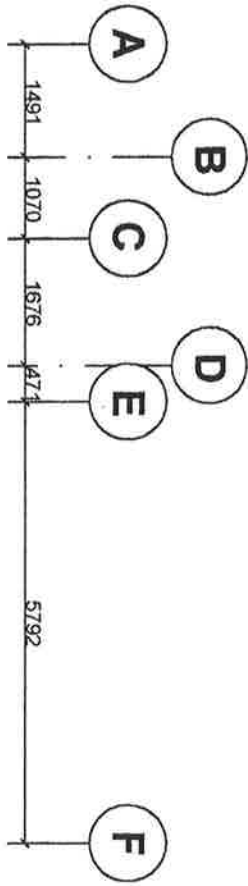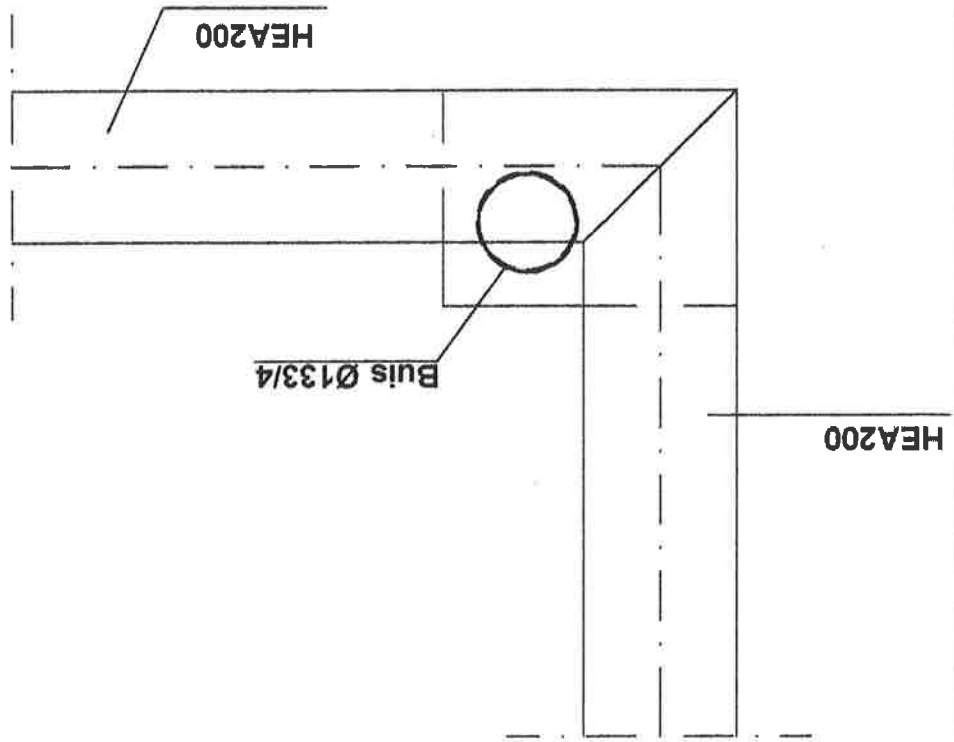

onderdeel : OVERZICHT VERDIEPING

onderdeel : OVERZICHT VERDIEPING
schaal : 1:100/ 1:10
format : A3
datum : 28 oktober 2003
proj.echnummer : A-109498
tek. nummer : 9
Wtje. A:
Wtje. B: