



Principe details


Gemeenschapsgebouw Hacı Bayram

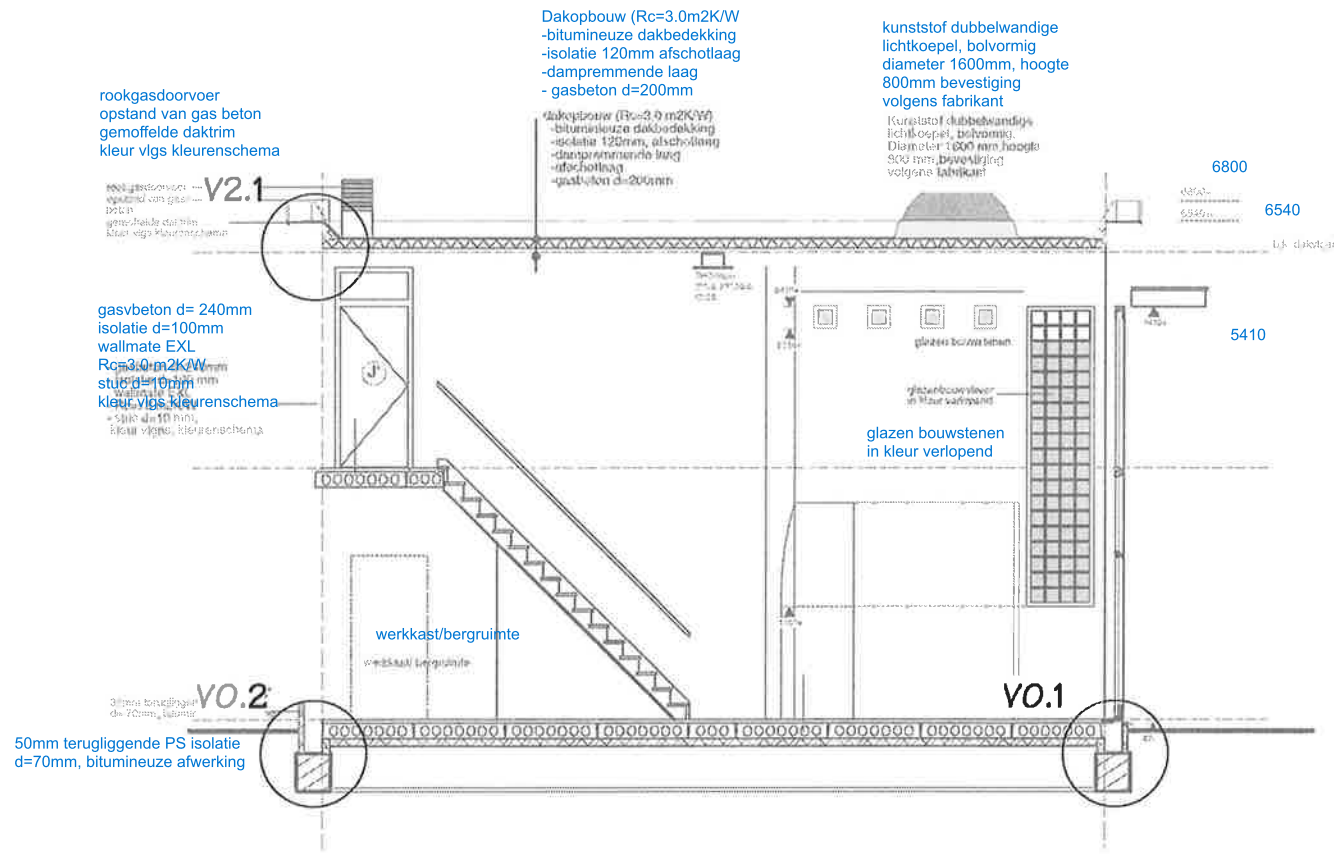


Type A: GEVEL STRAAT ZUID

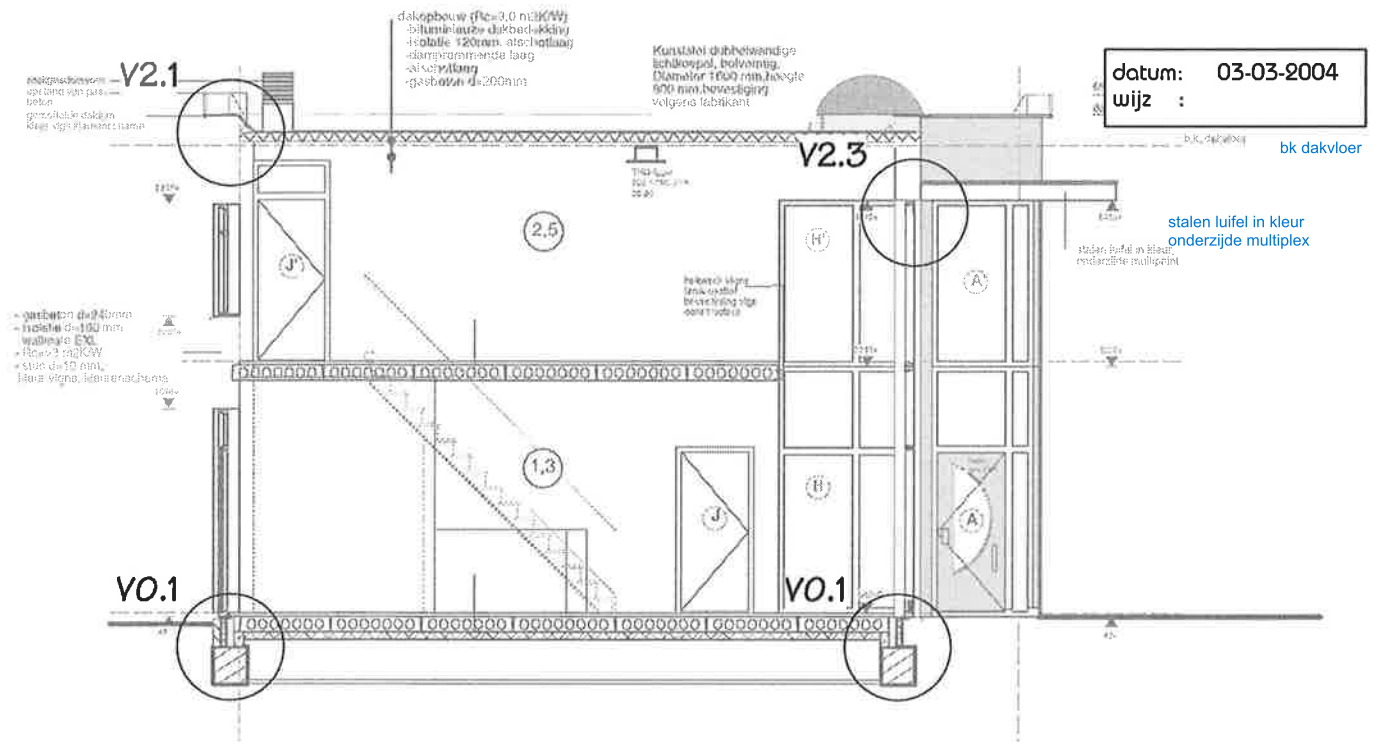

Type A: GEVEL STRAAT OOST

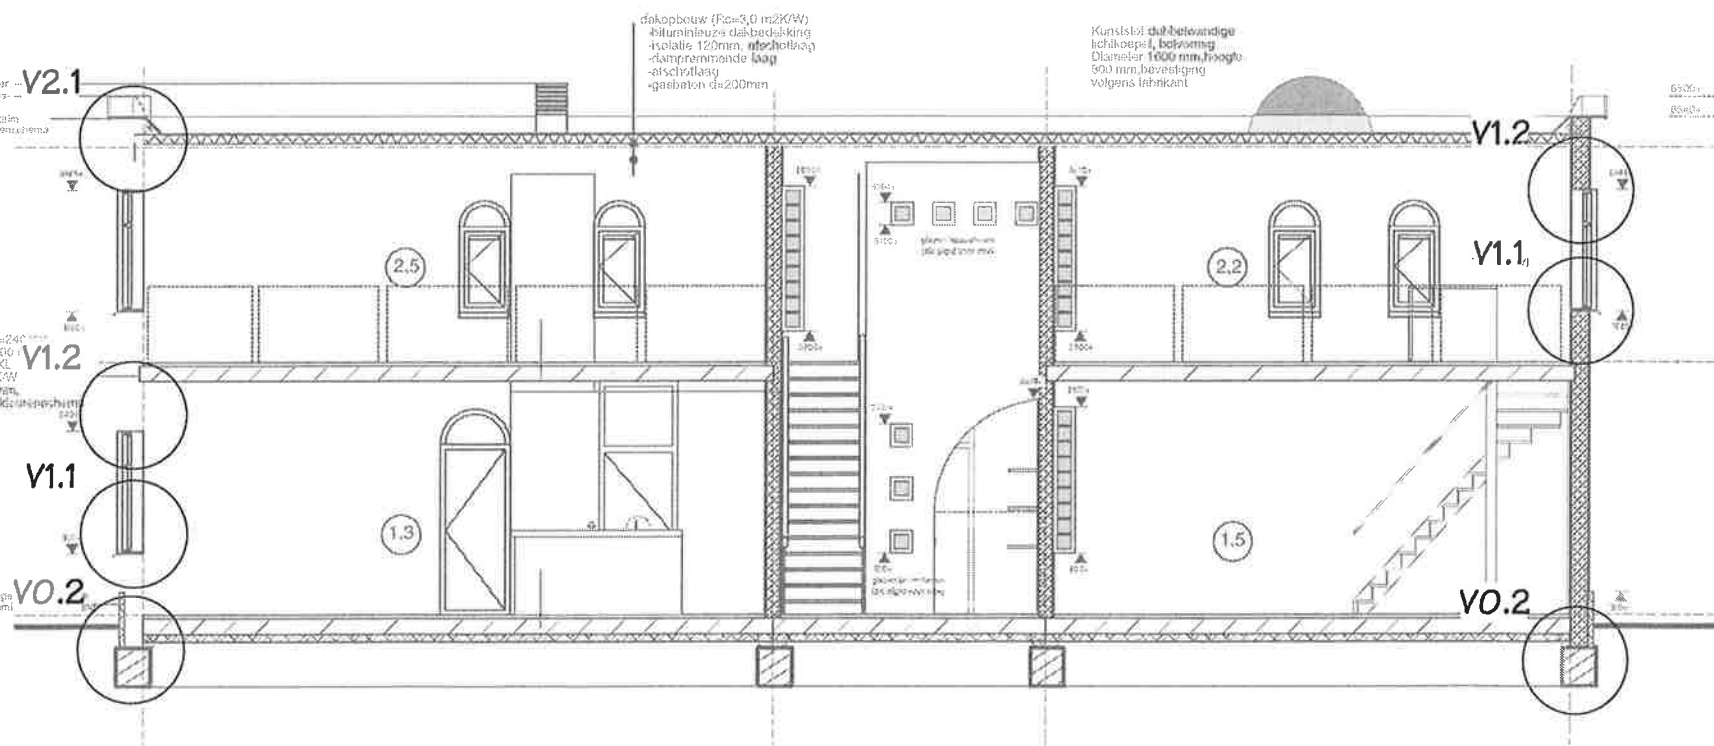

Type A: GEVEL TUIN NOORD




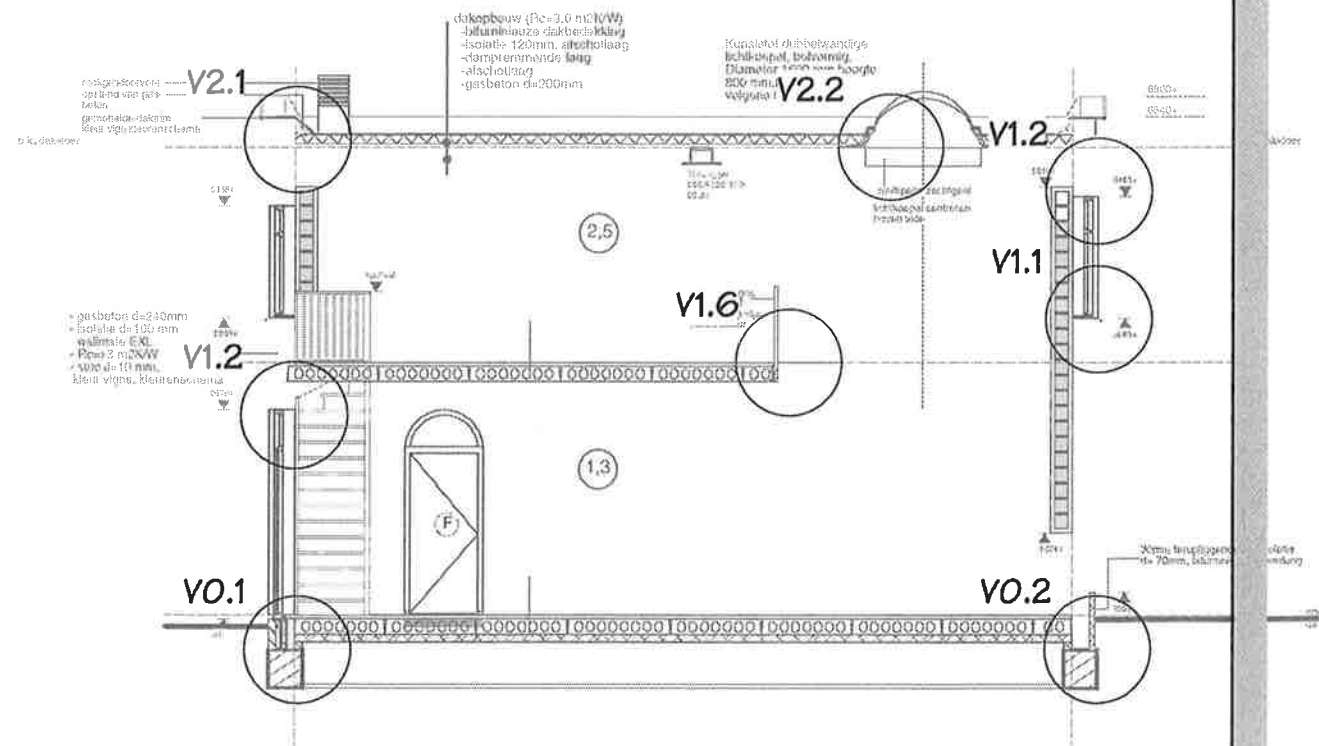


Type A: GEVEL TUIN WEST

SBB Spakenburgs Bouwbedrijf

datum: 03-03-2004
wiz :


"Haci Bayram", Bunschoten/Spakenburg

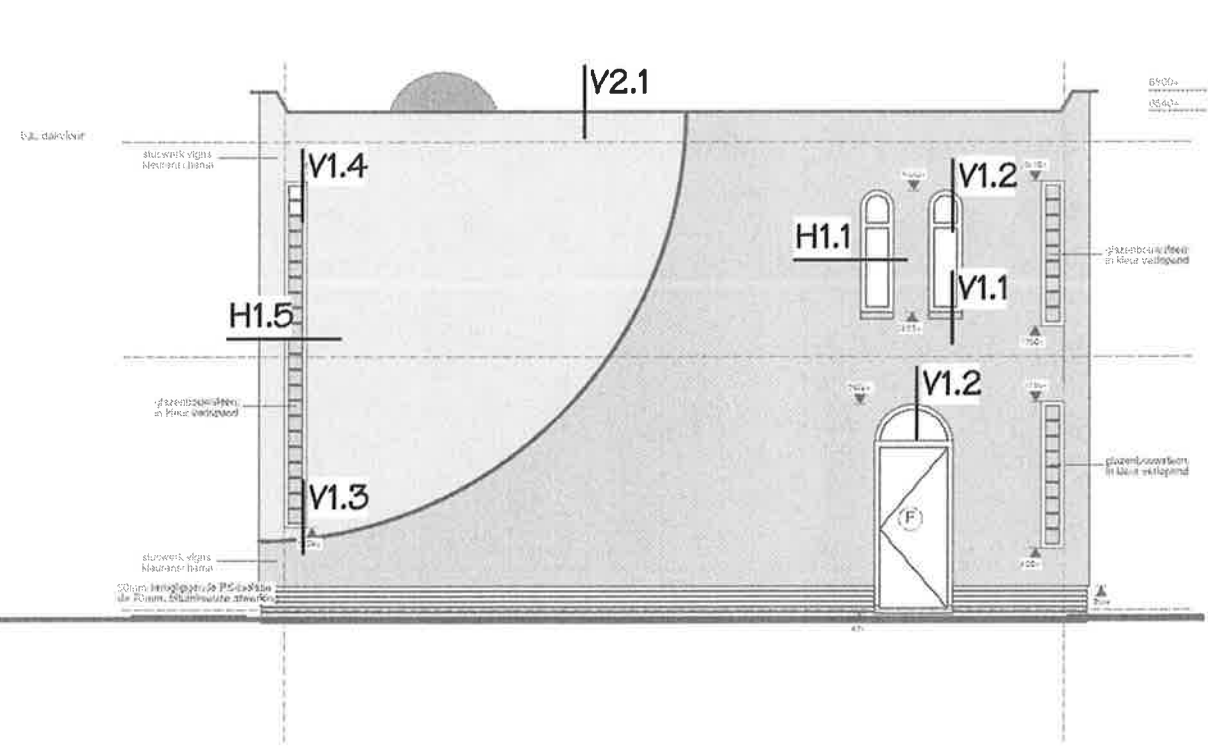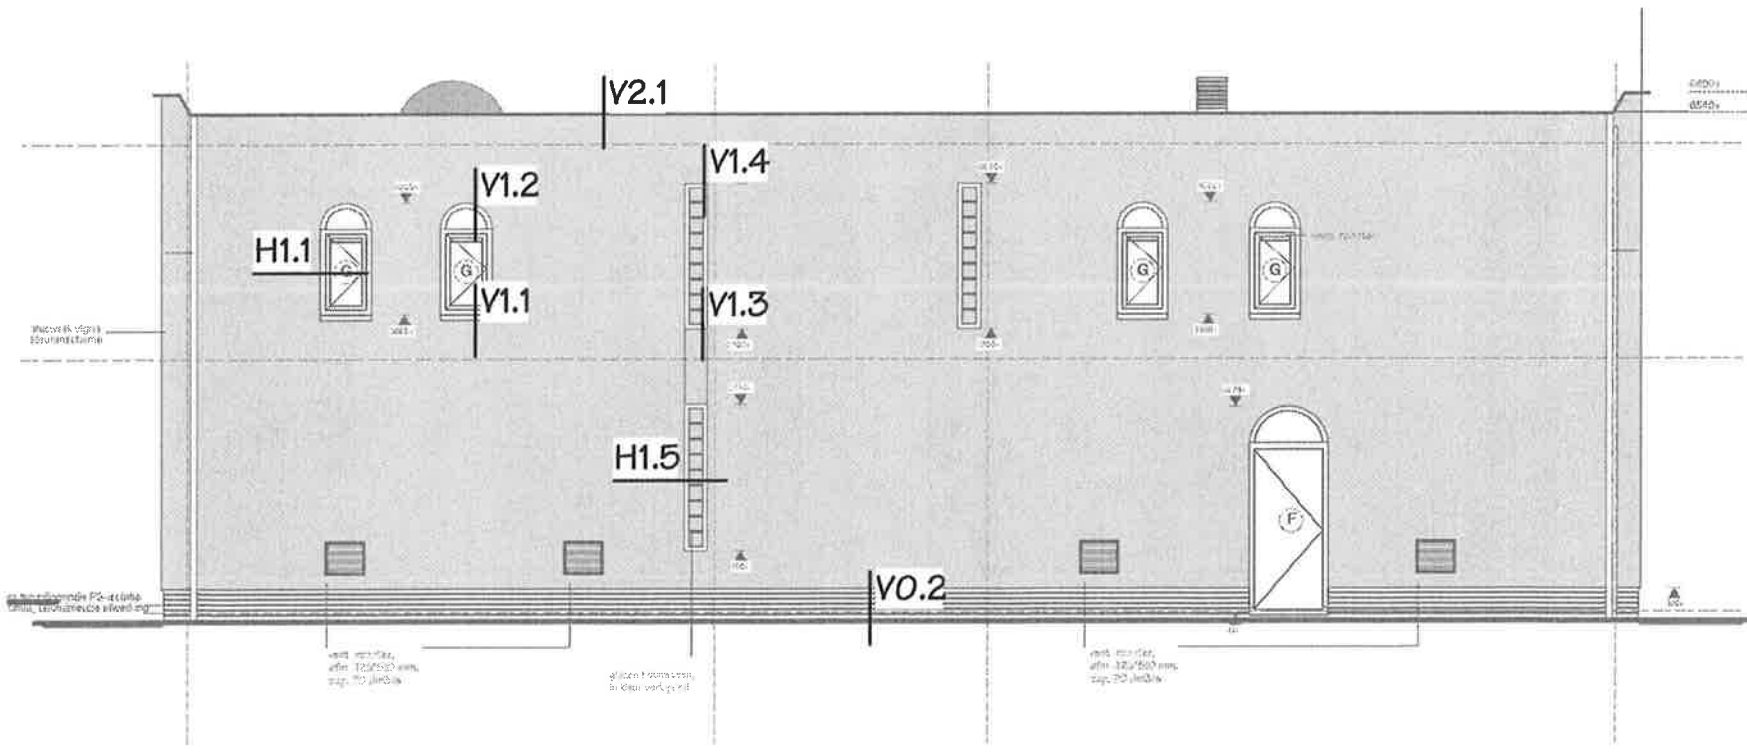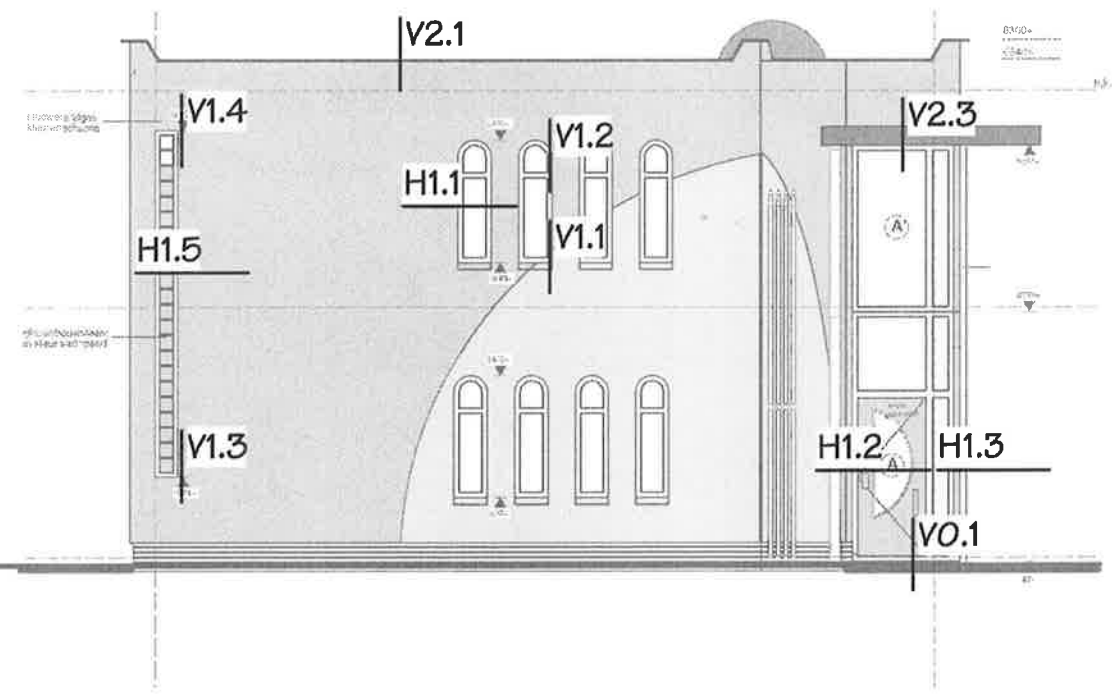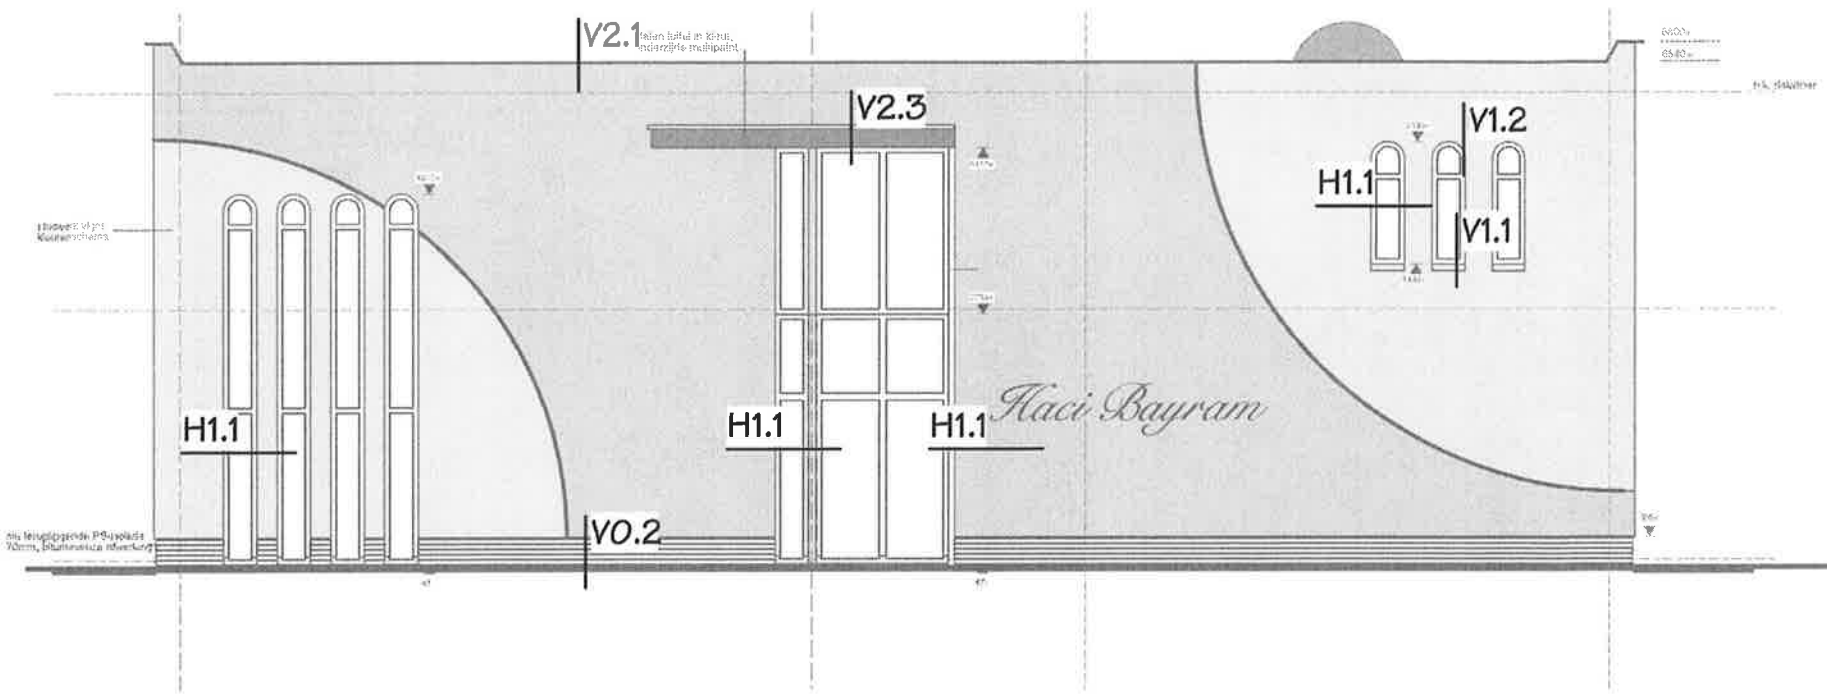

SBB Spakenburgs Bouwbedrijf


ir. Peter van Gerwen, architecten

datum: 03-03-2004
wiz :

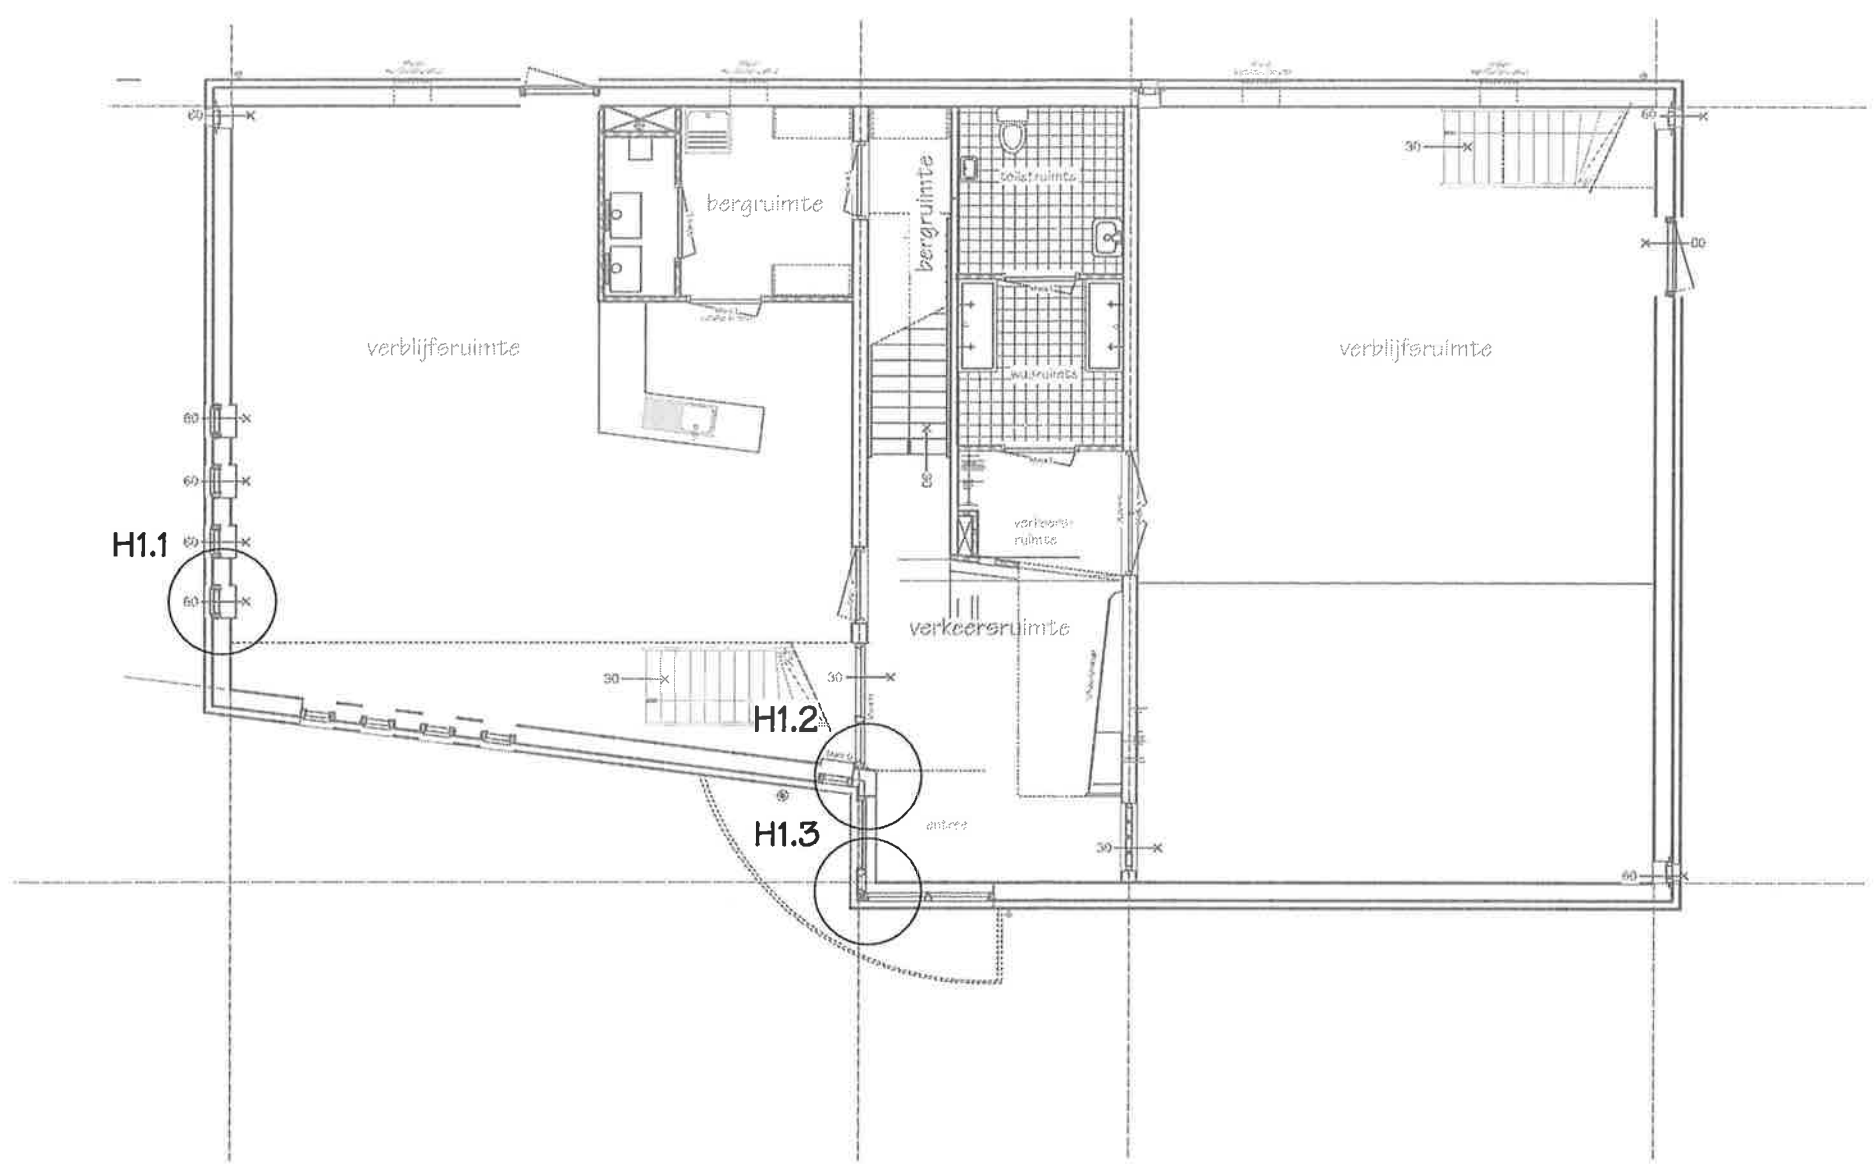



"Haci Bayram", Bunschoten/Spakenburg

datum: 03-03-2004
wijz :

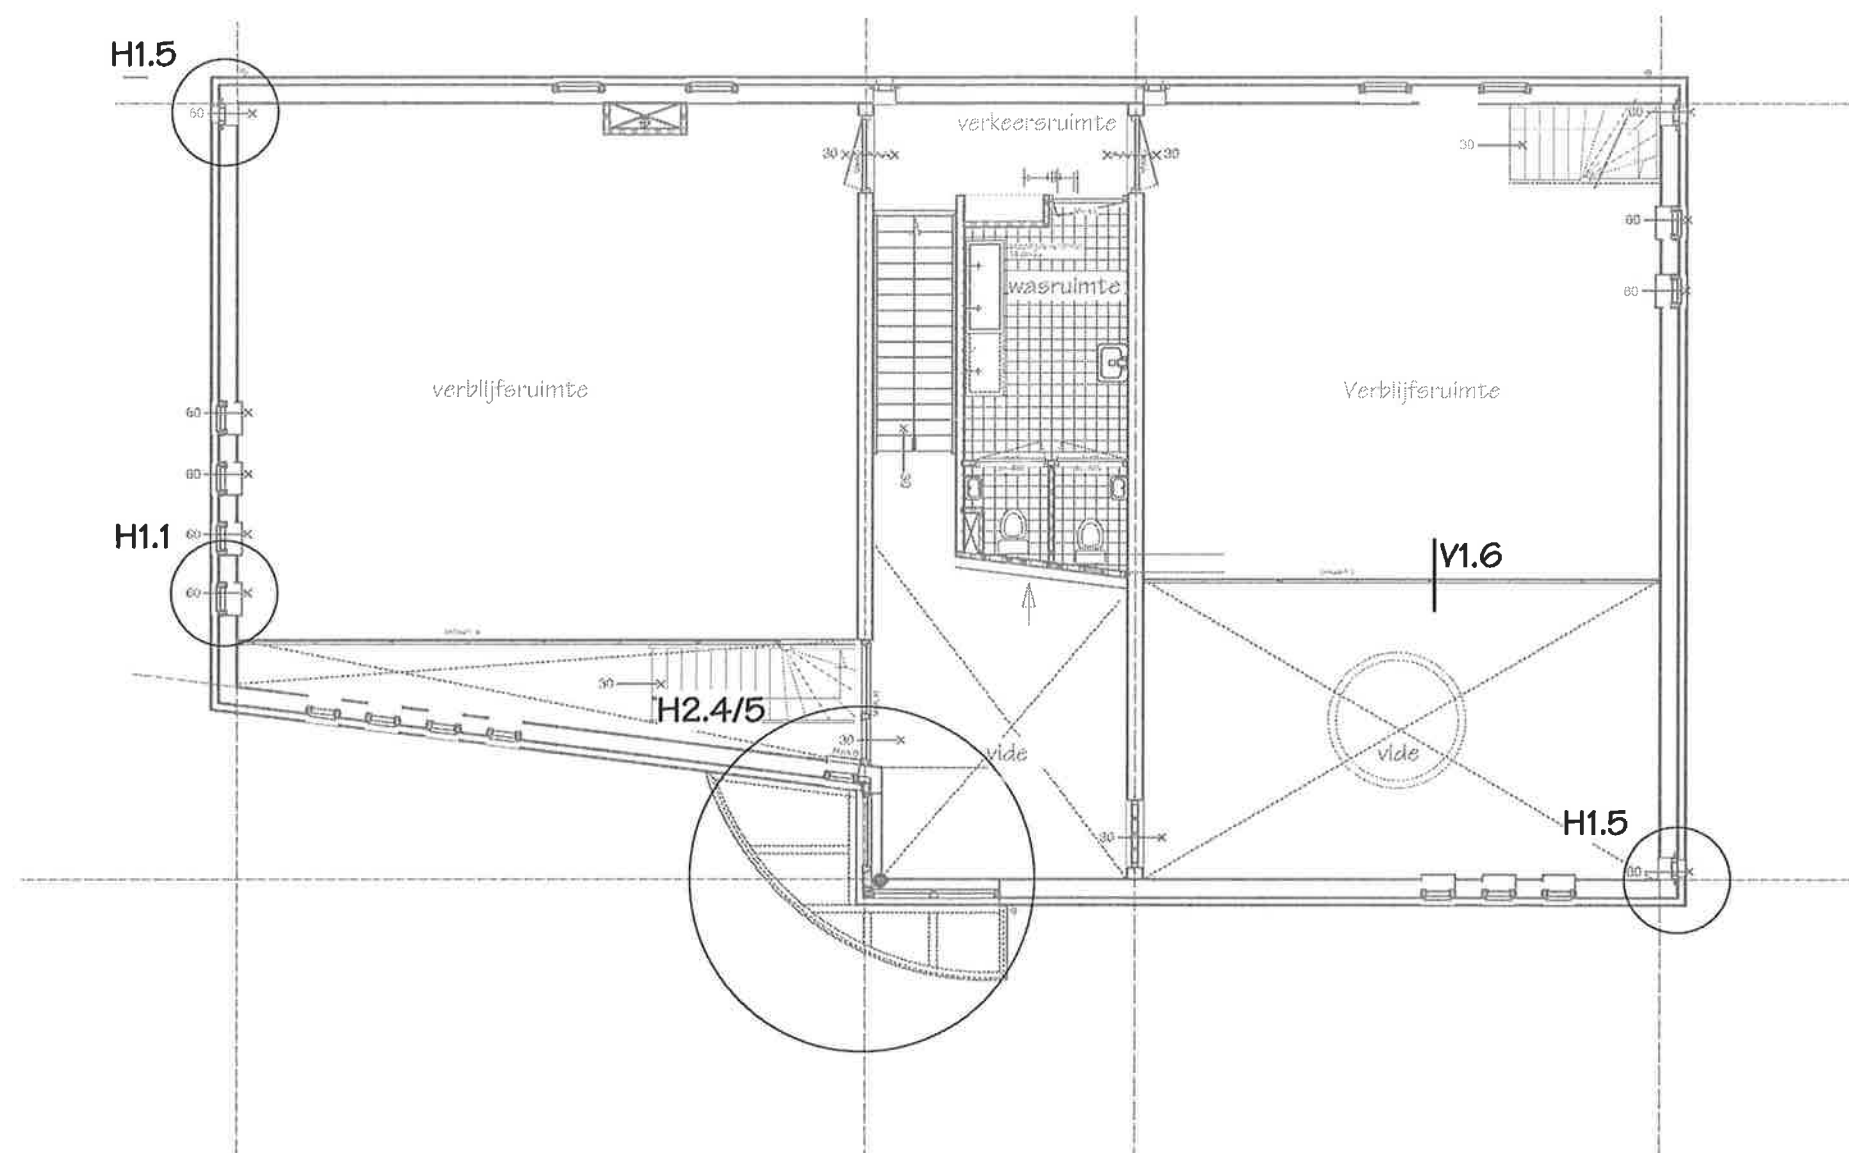


"Haci Bayram", Bunschoten/Spakenburg

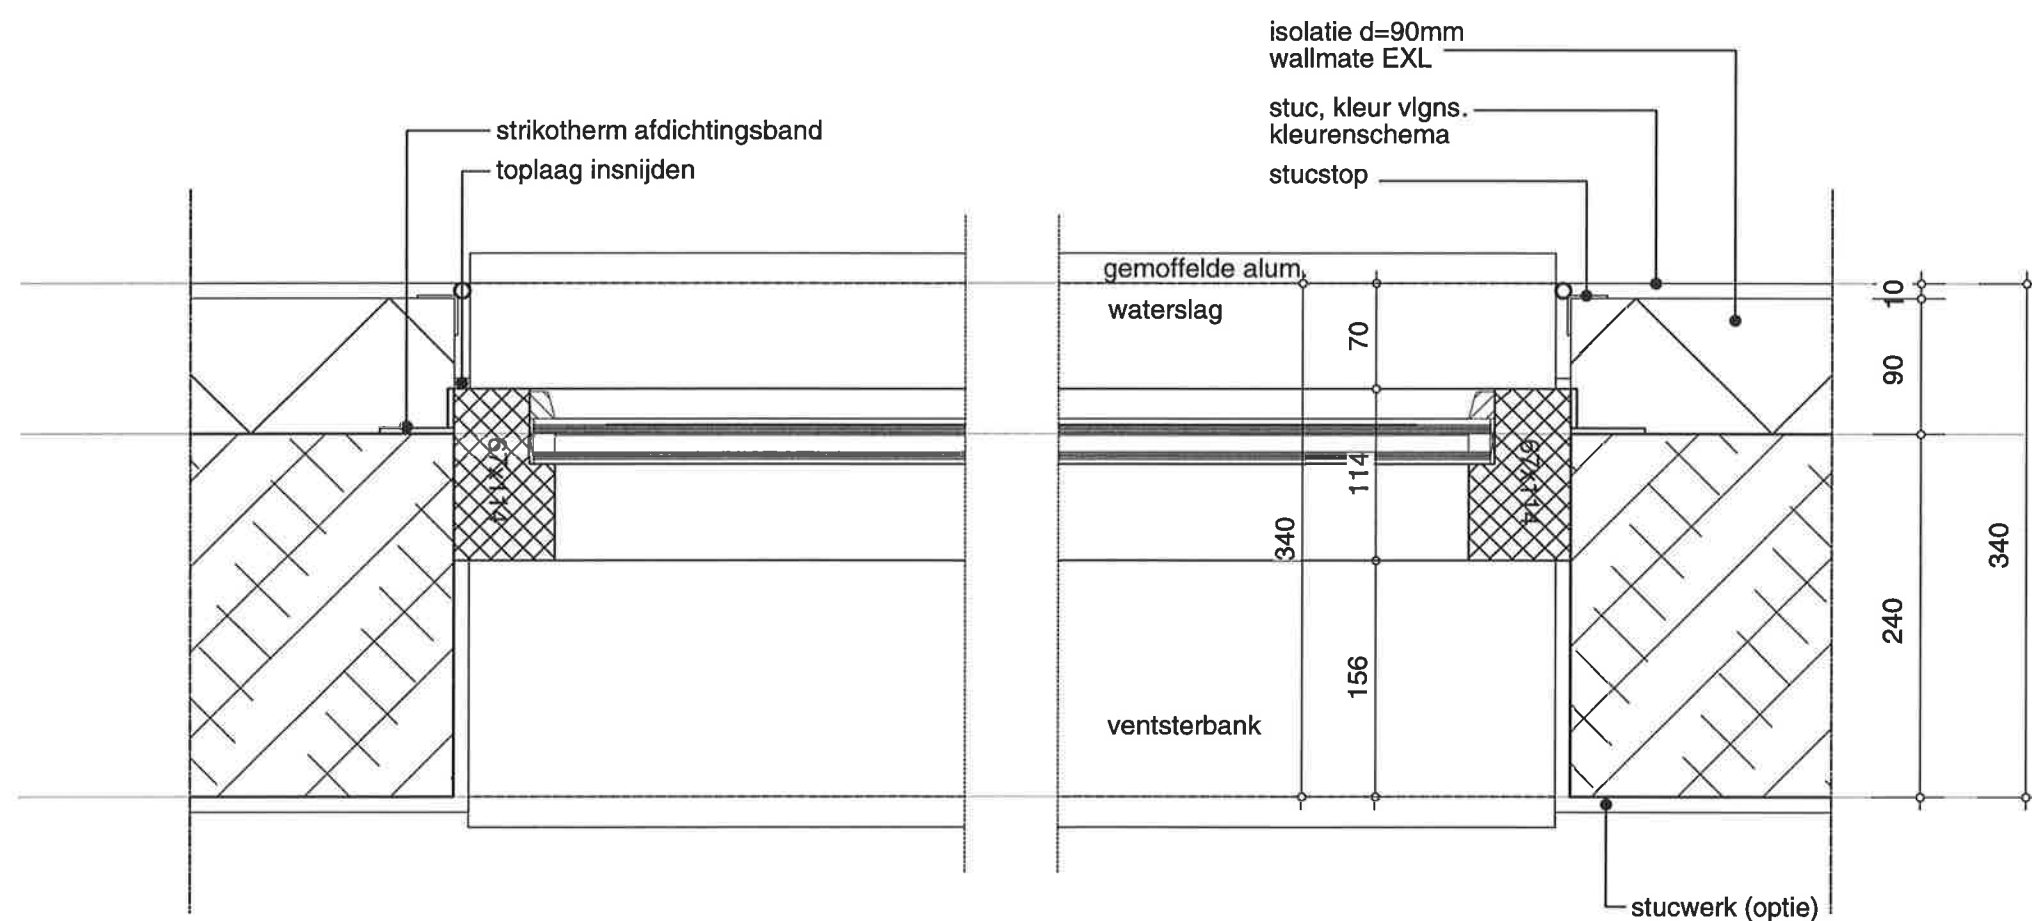


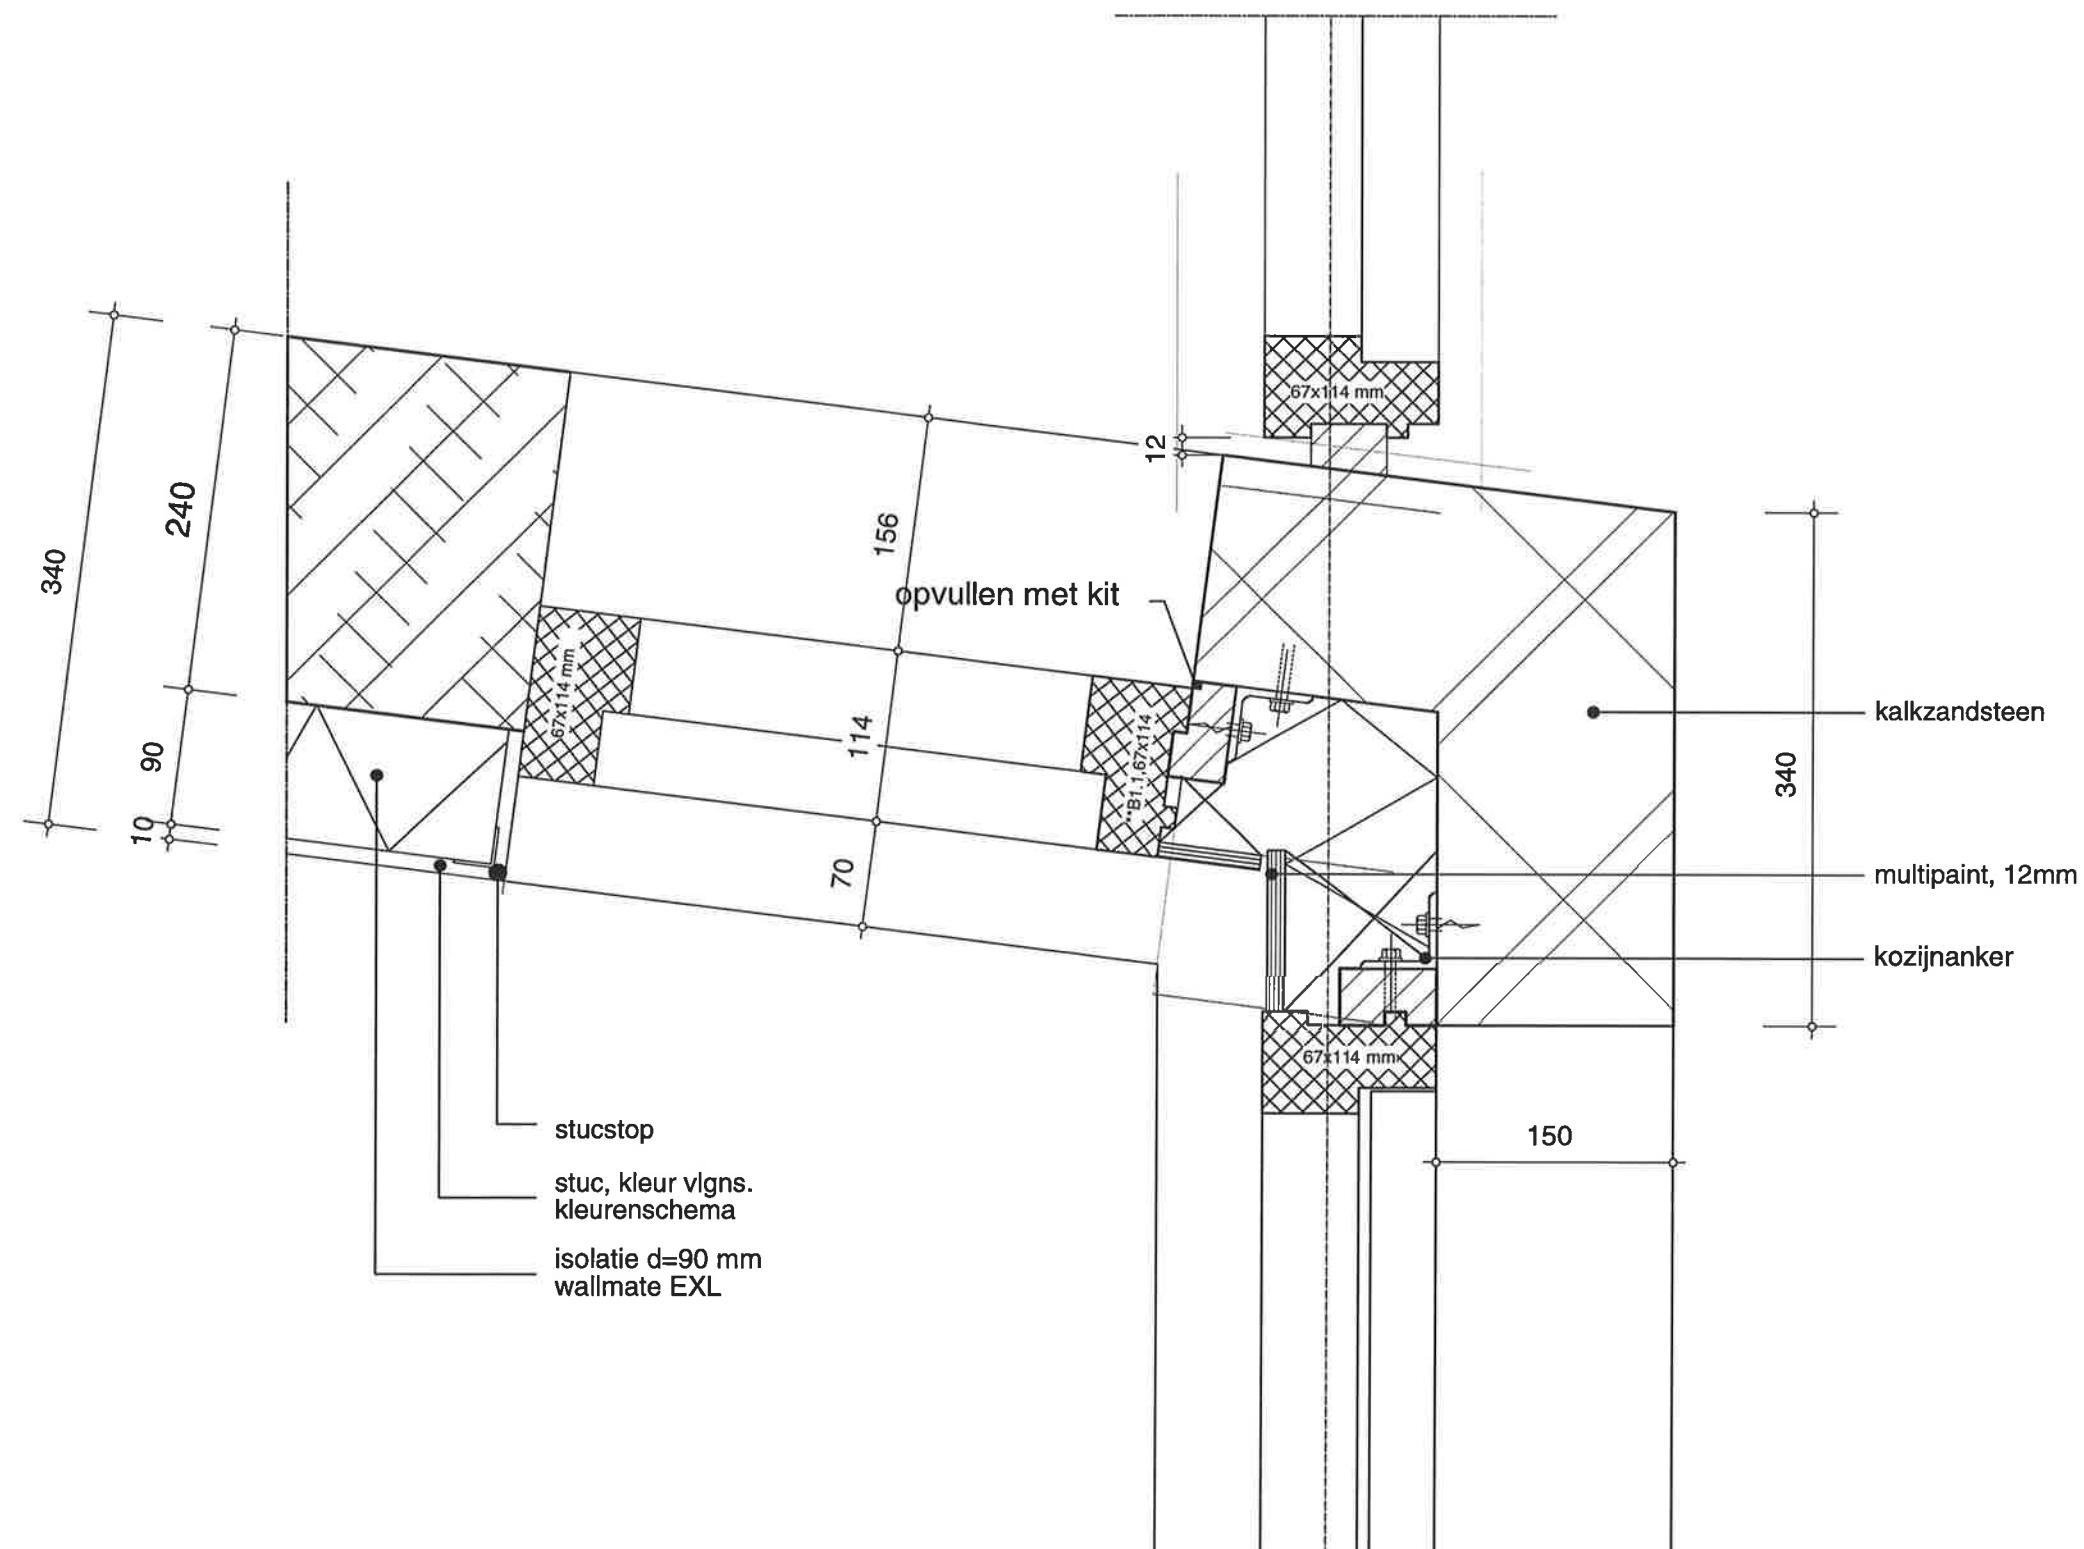


datum: 03-03-2004
wijz :

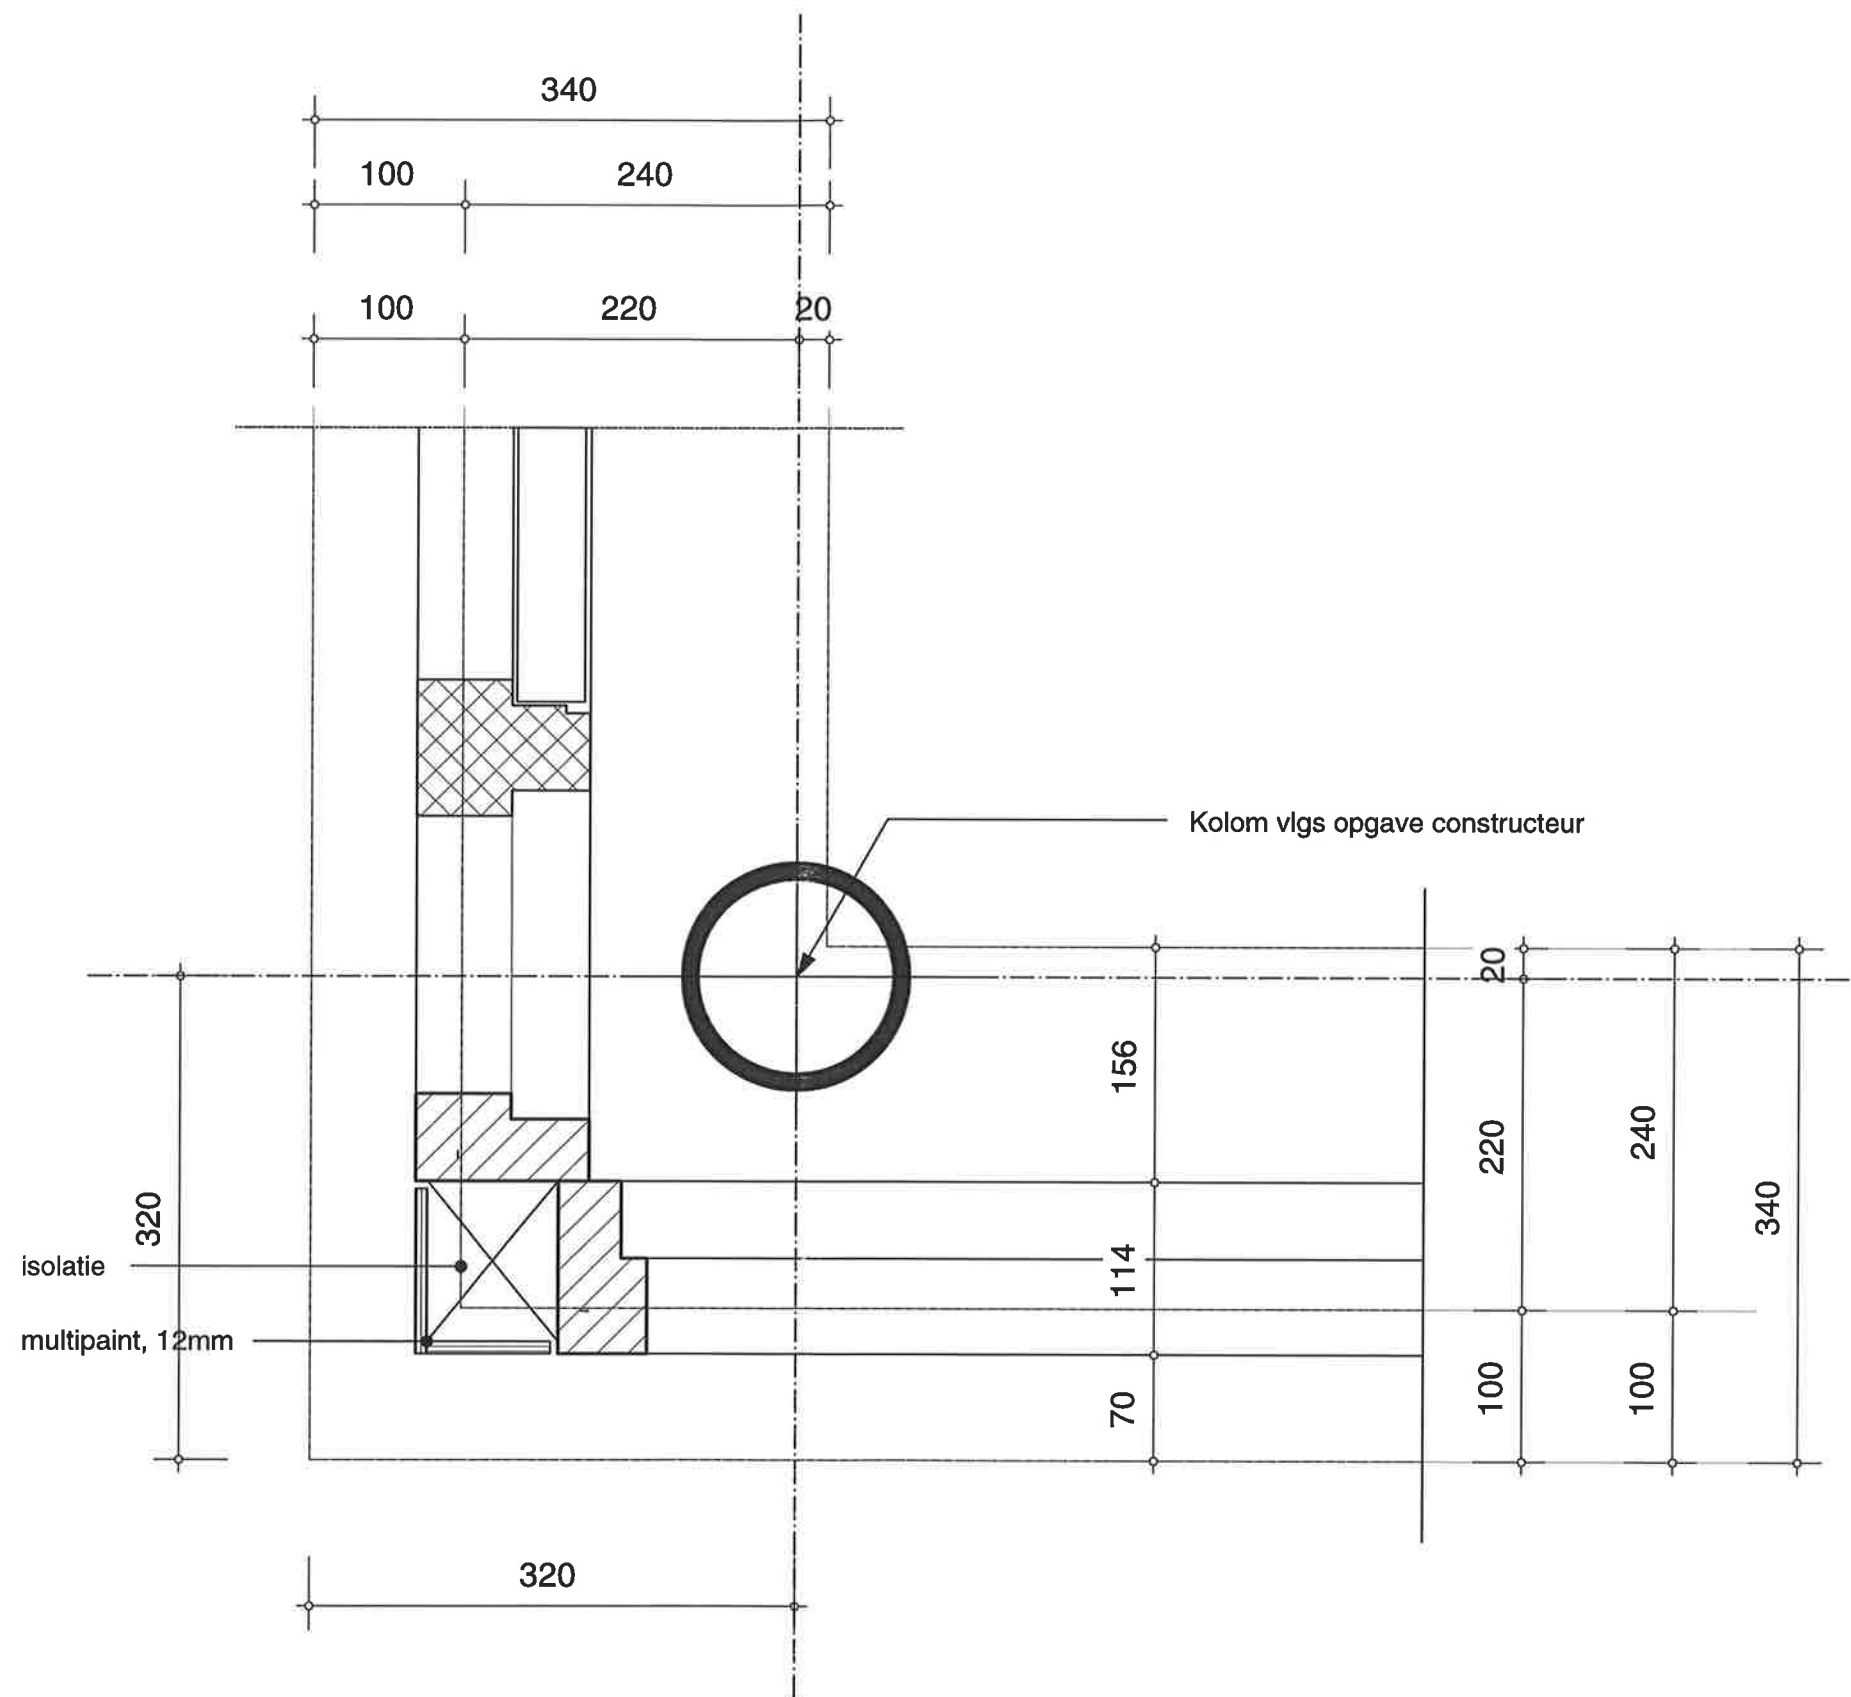


datum: 03-03-2004
wiz :

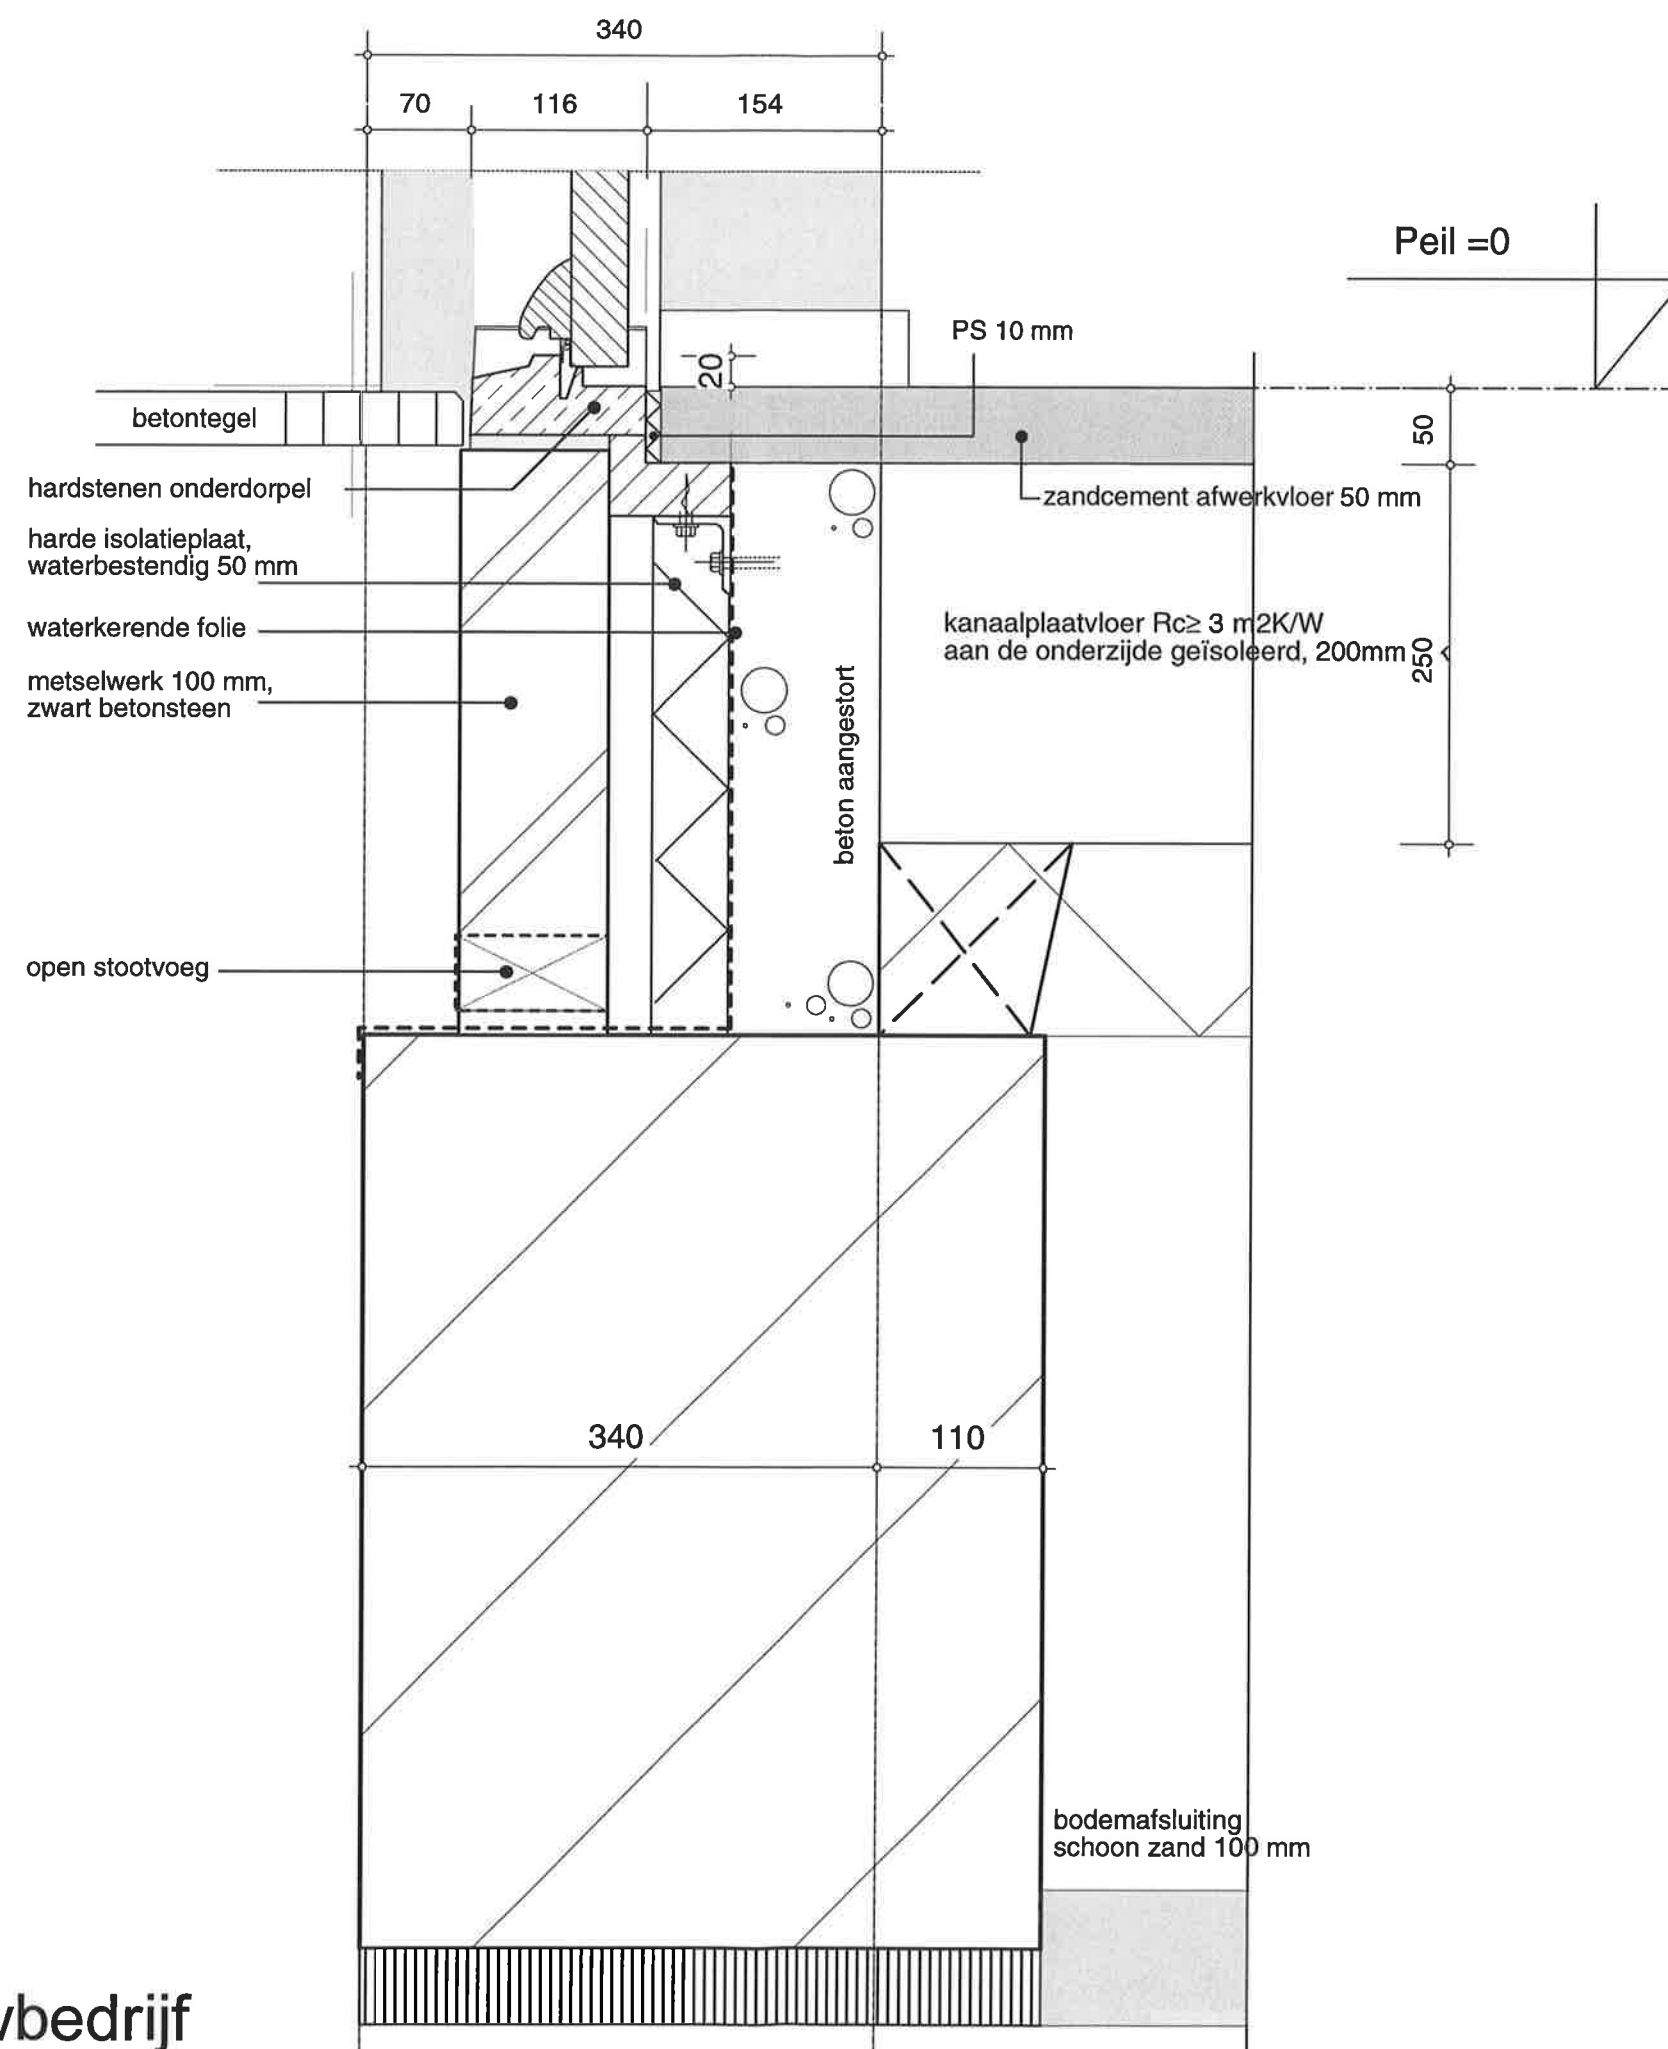


datum: 03-03-2004
wiz :

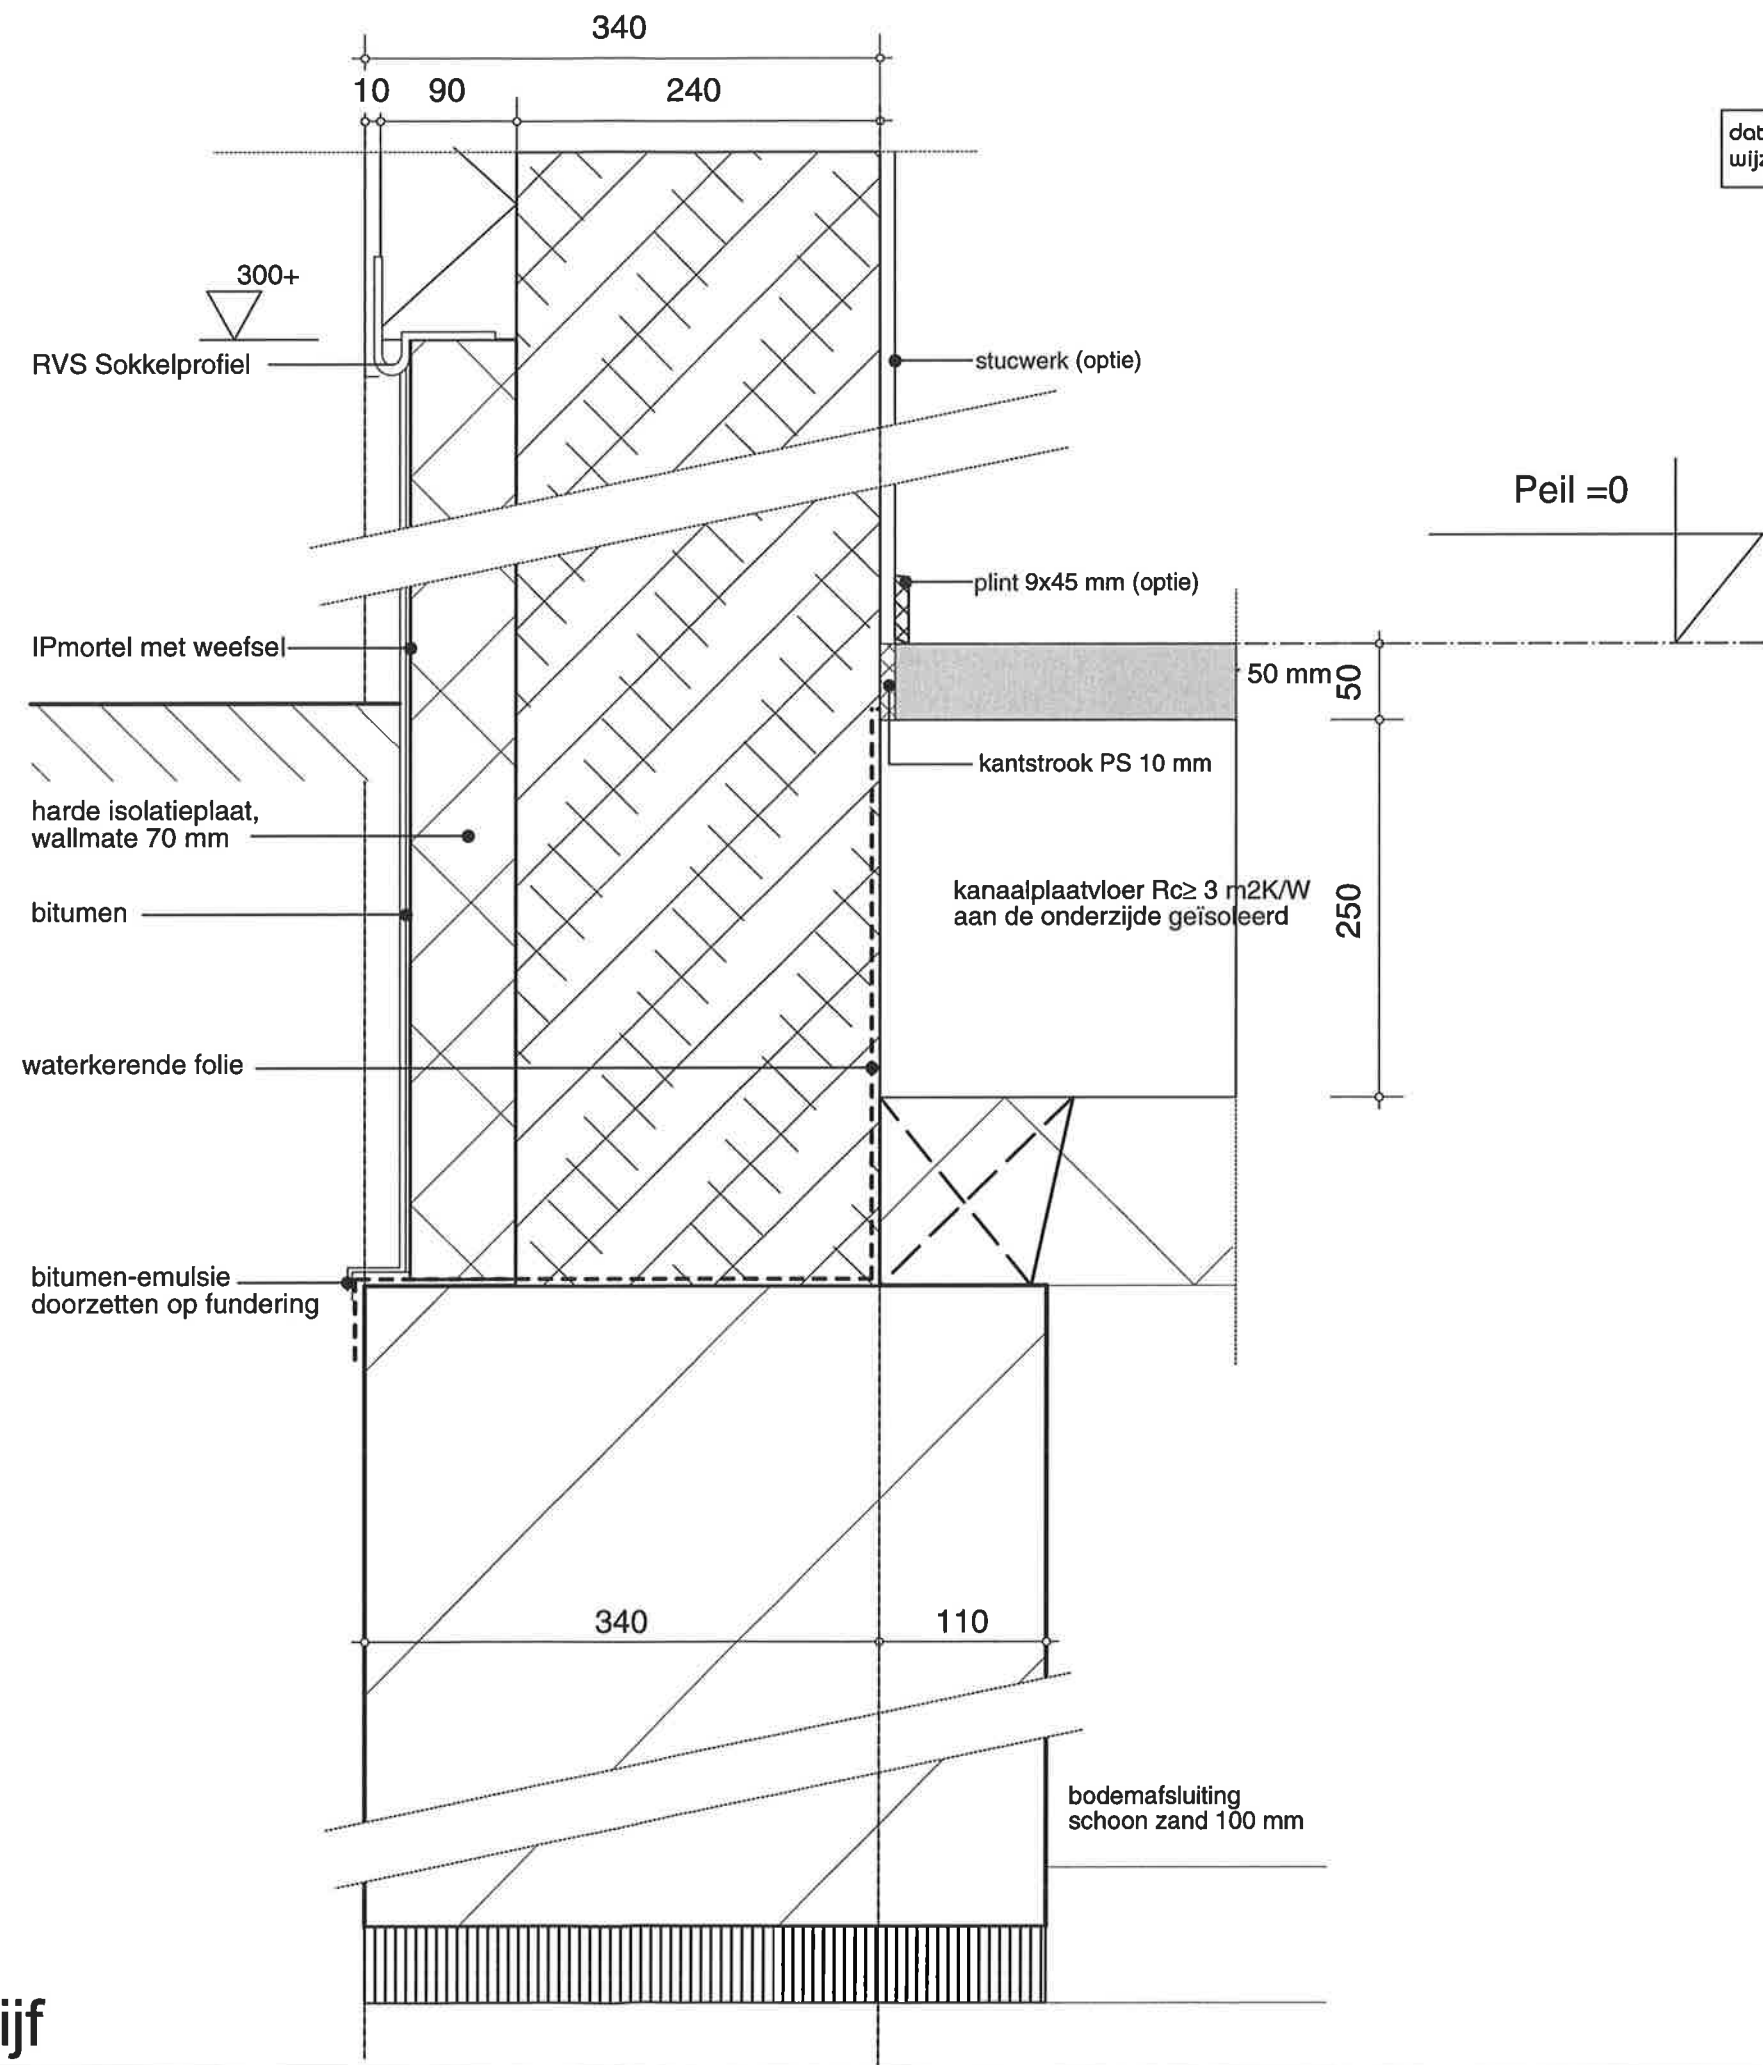


"Haci Bayram", Bunschoten/Spakenburg

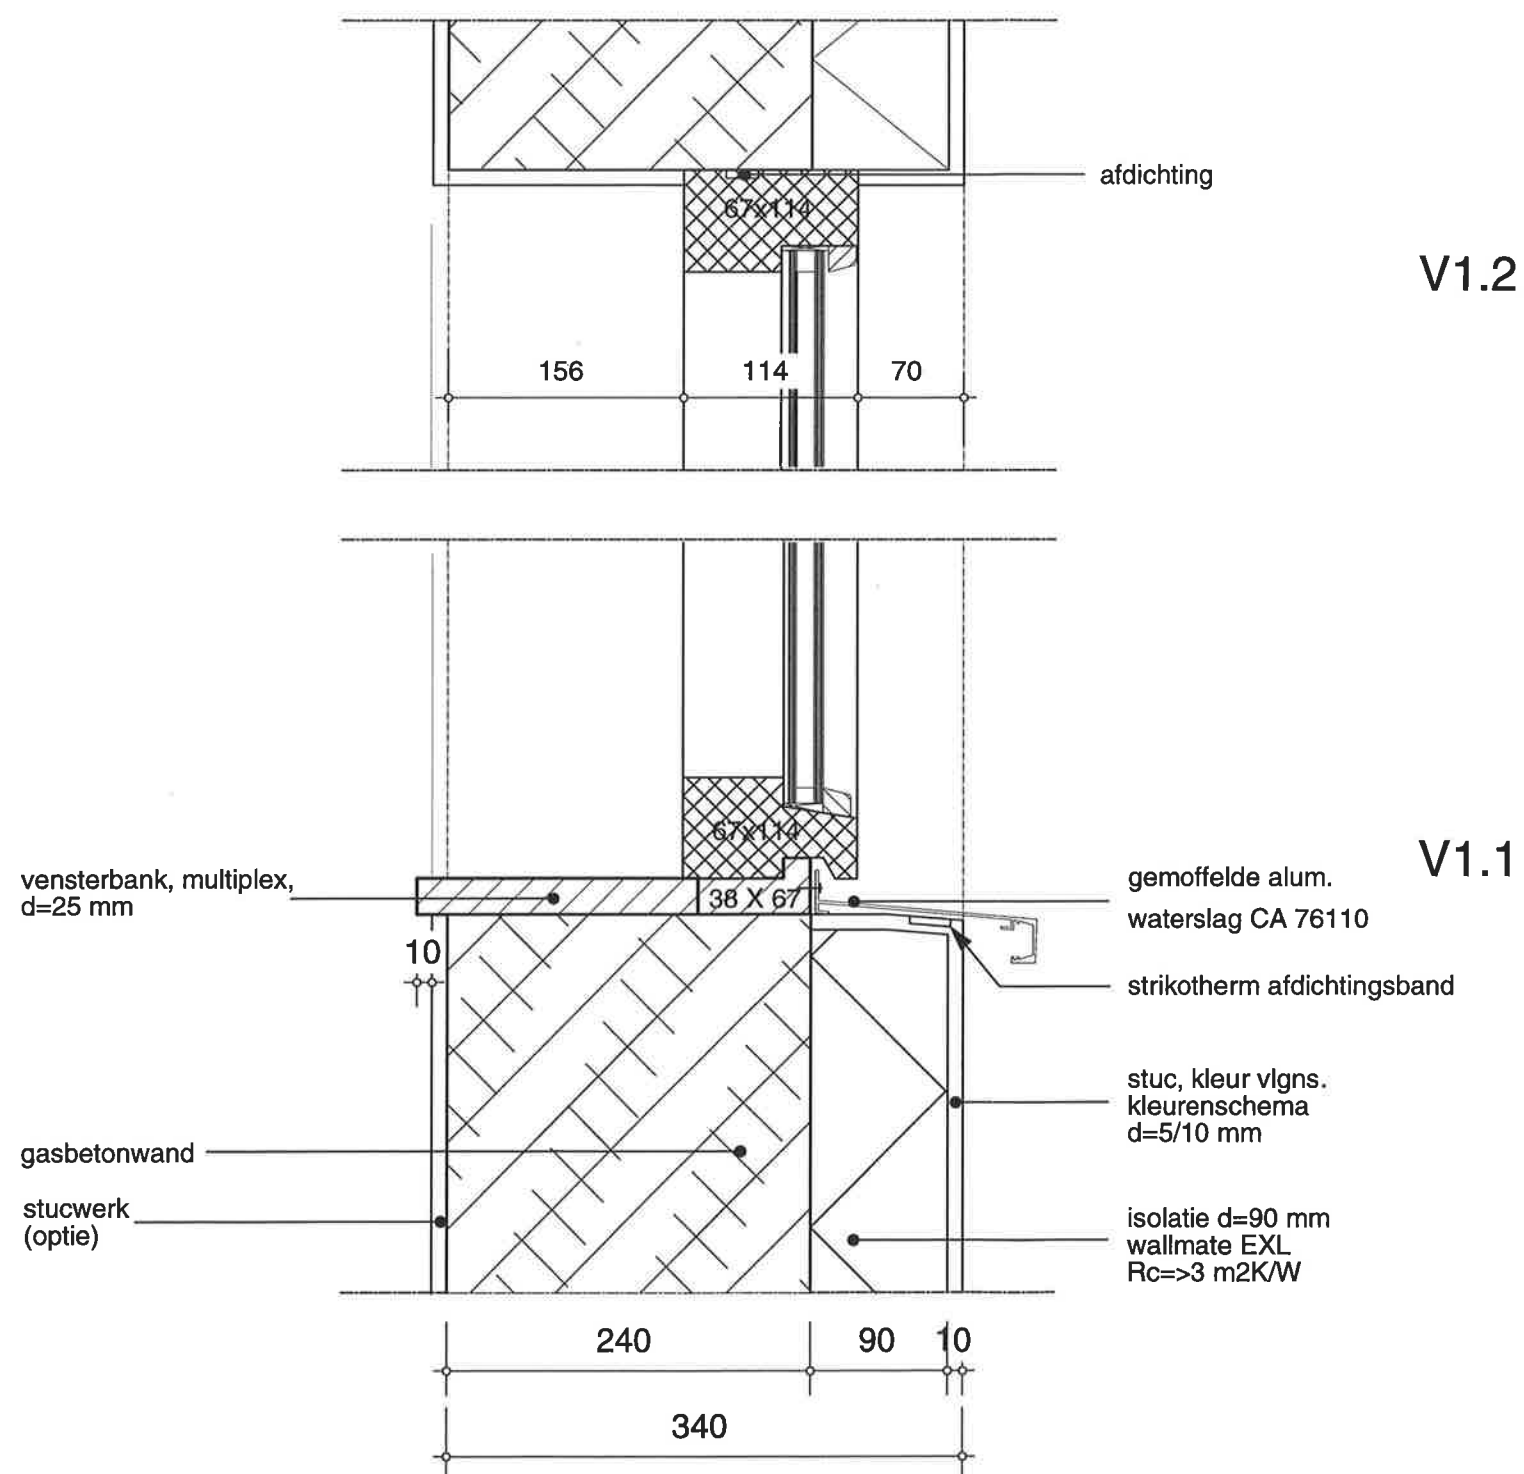

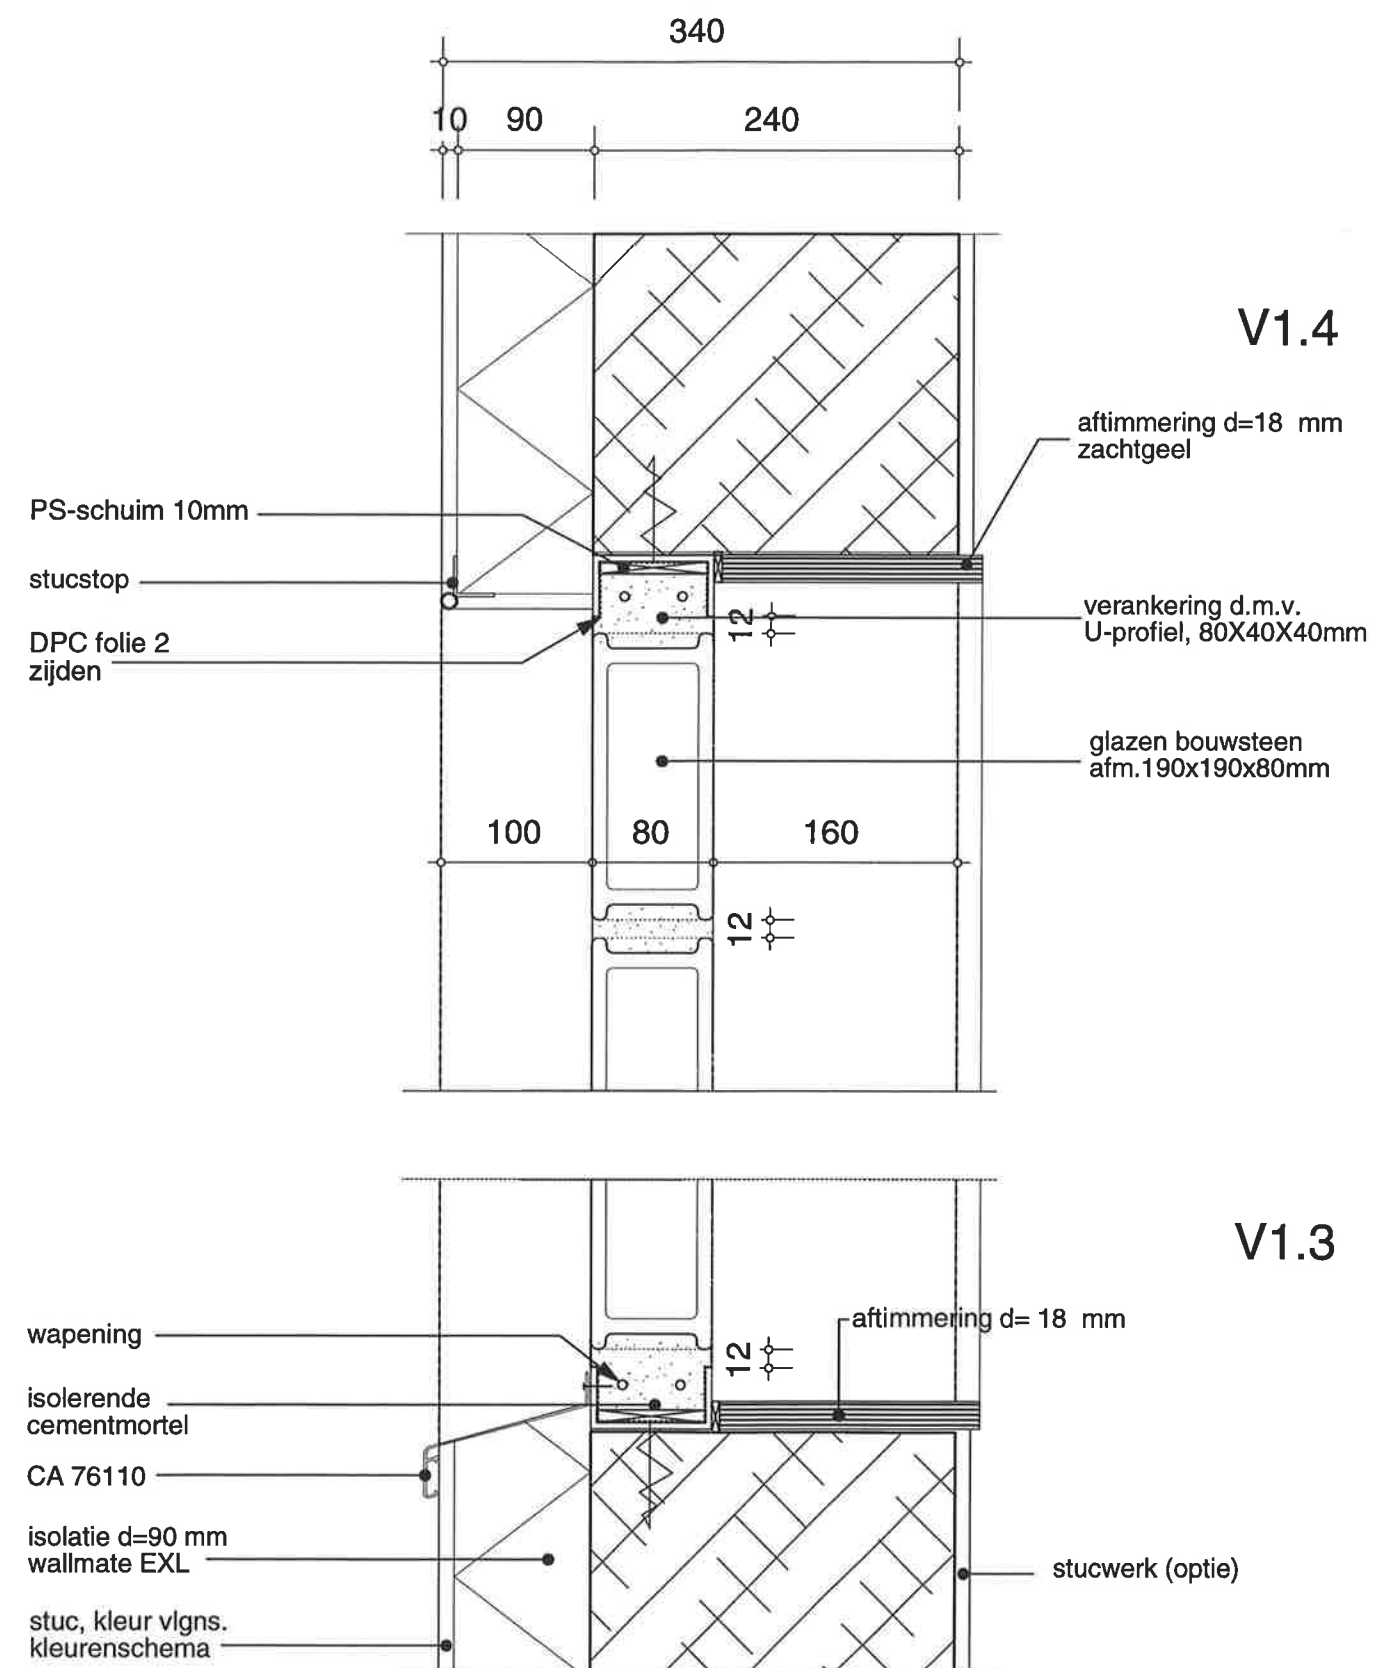

wiz

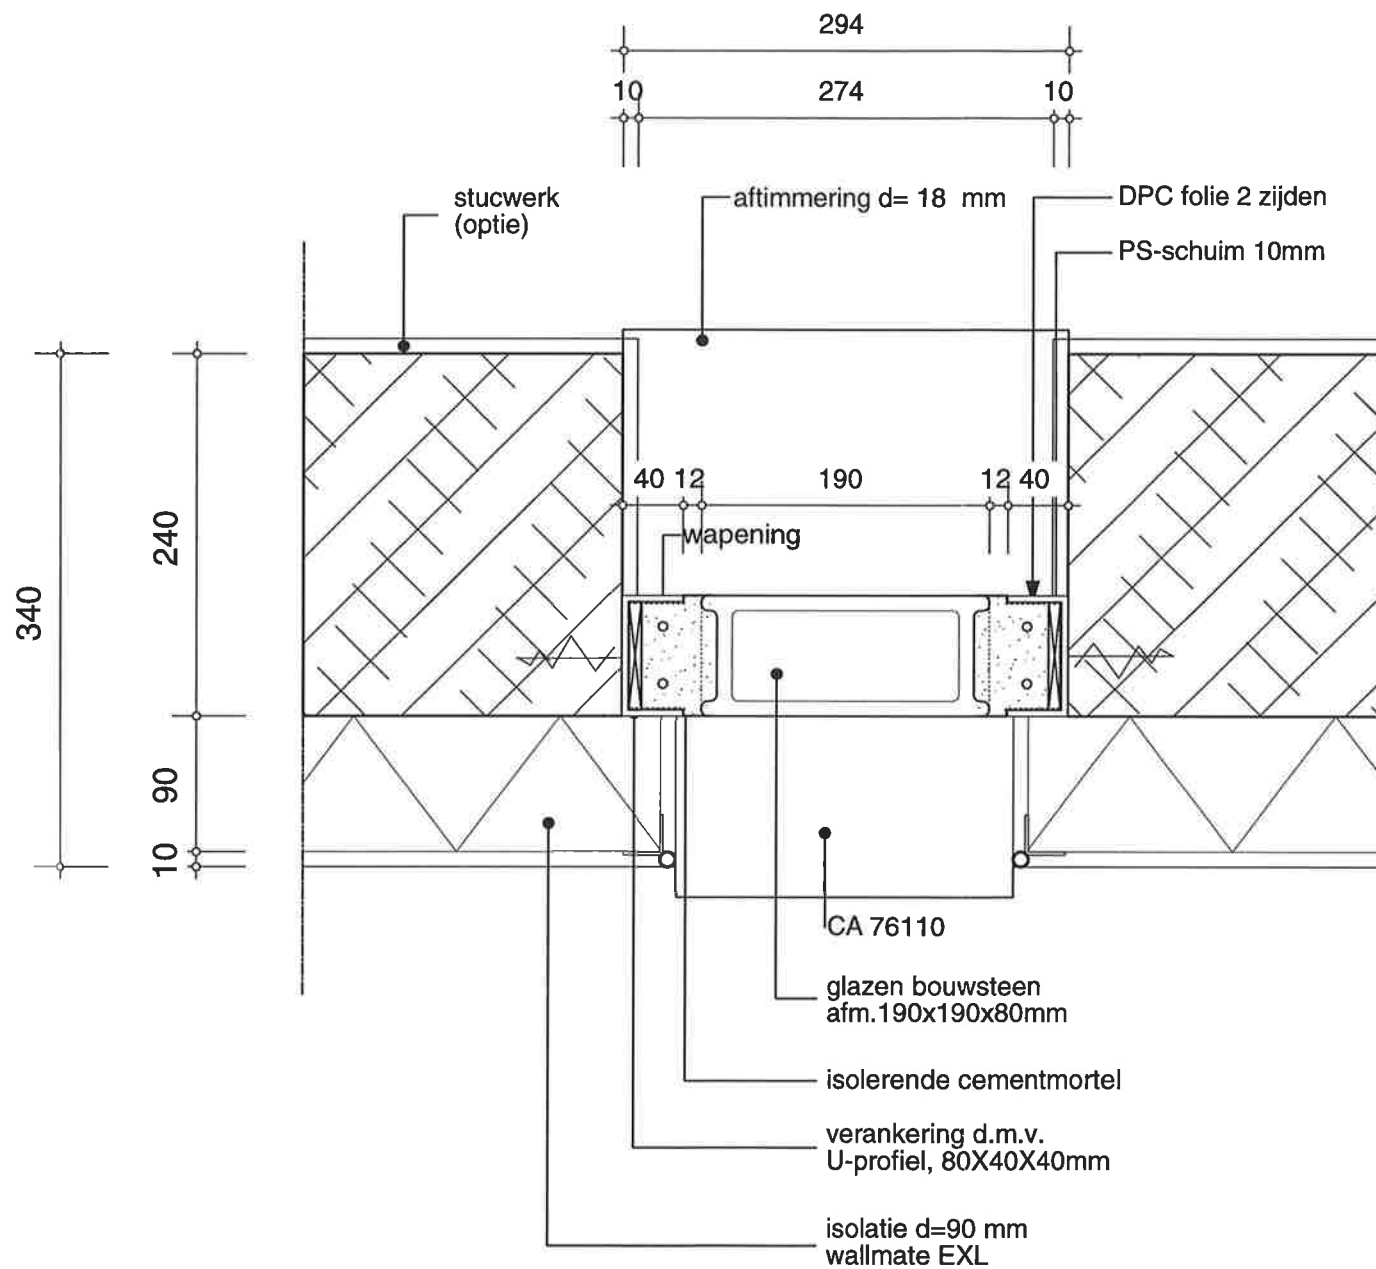


"Haci Bayram", Bunschoten/Spakenburg

SBB Spakenburgs Bouwbedrijf

ir. Peter van Gerwen, architecten


V1.5

datum: 03-03-2004
wiz :

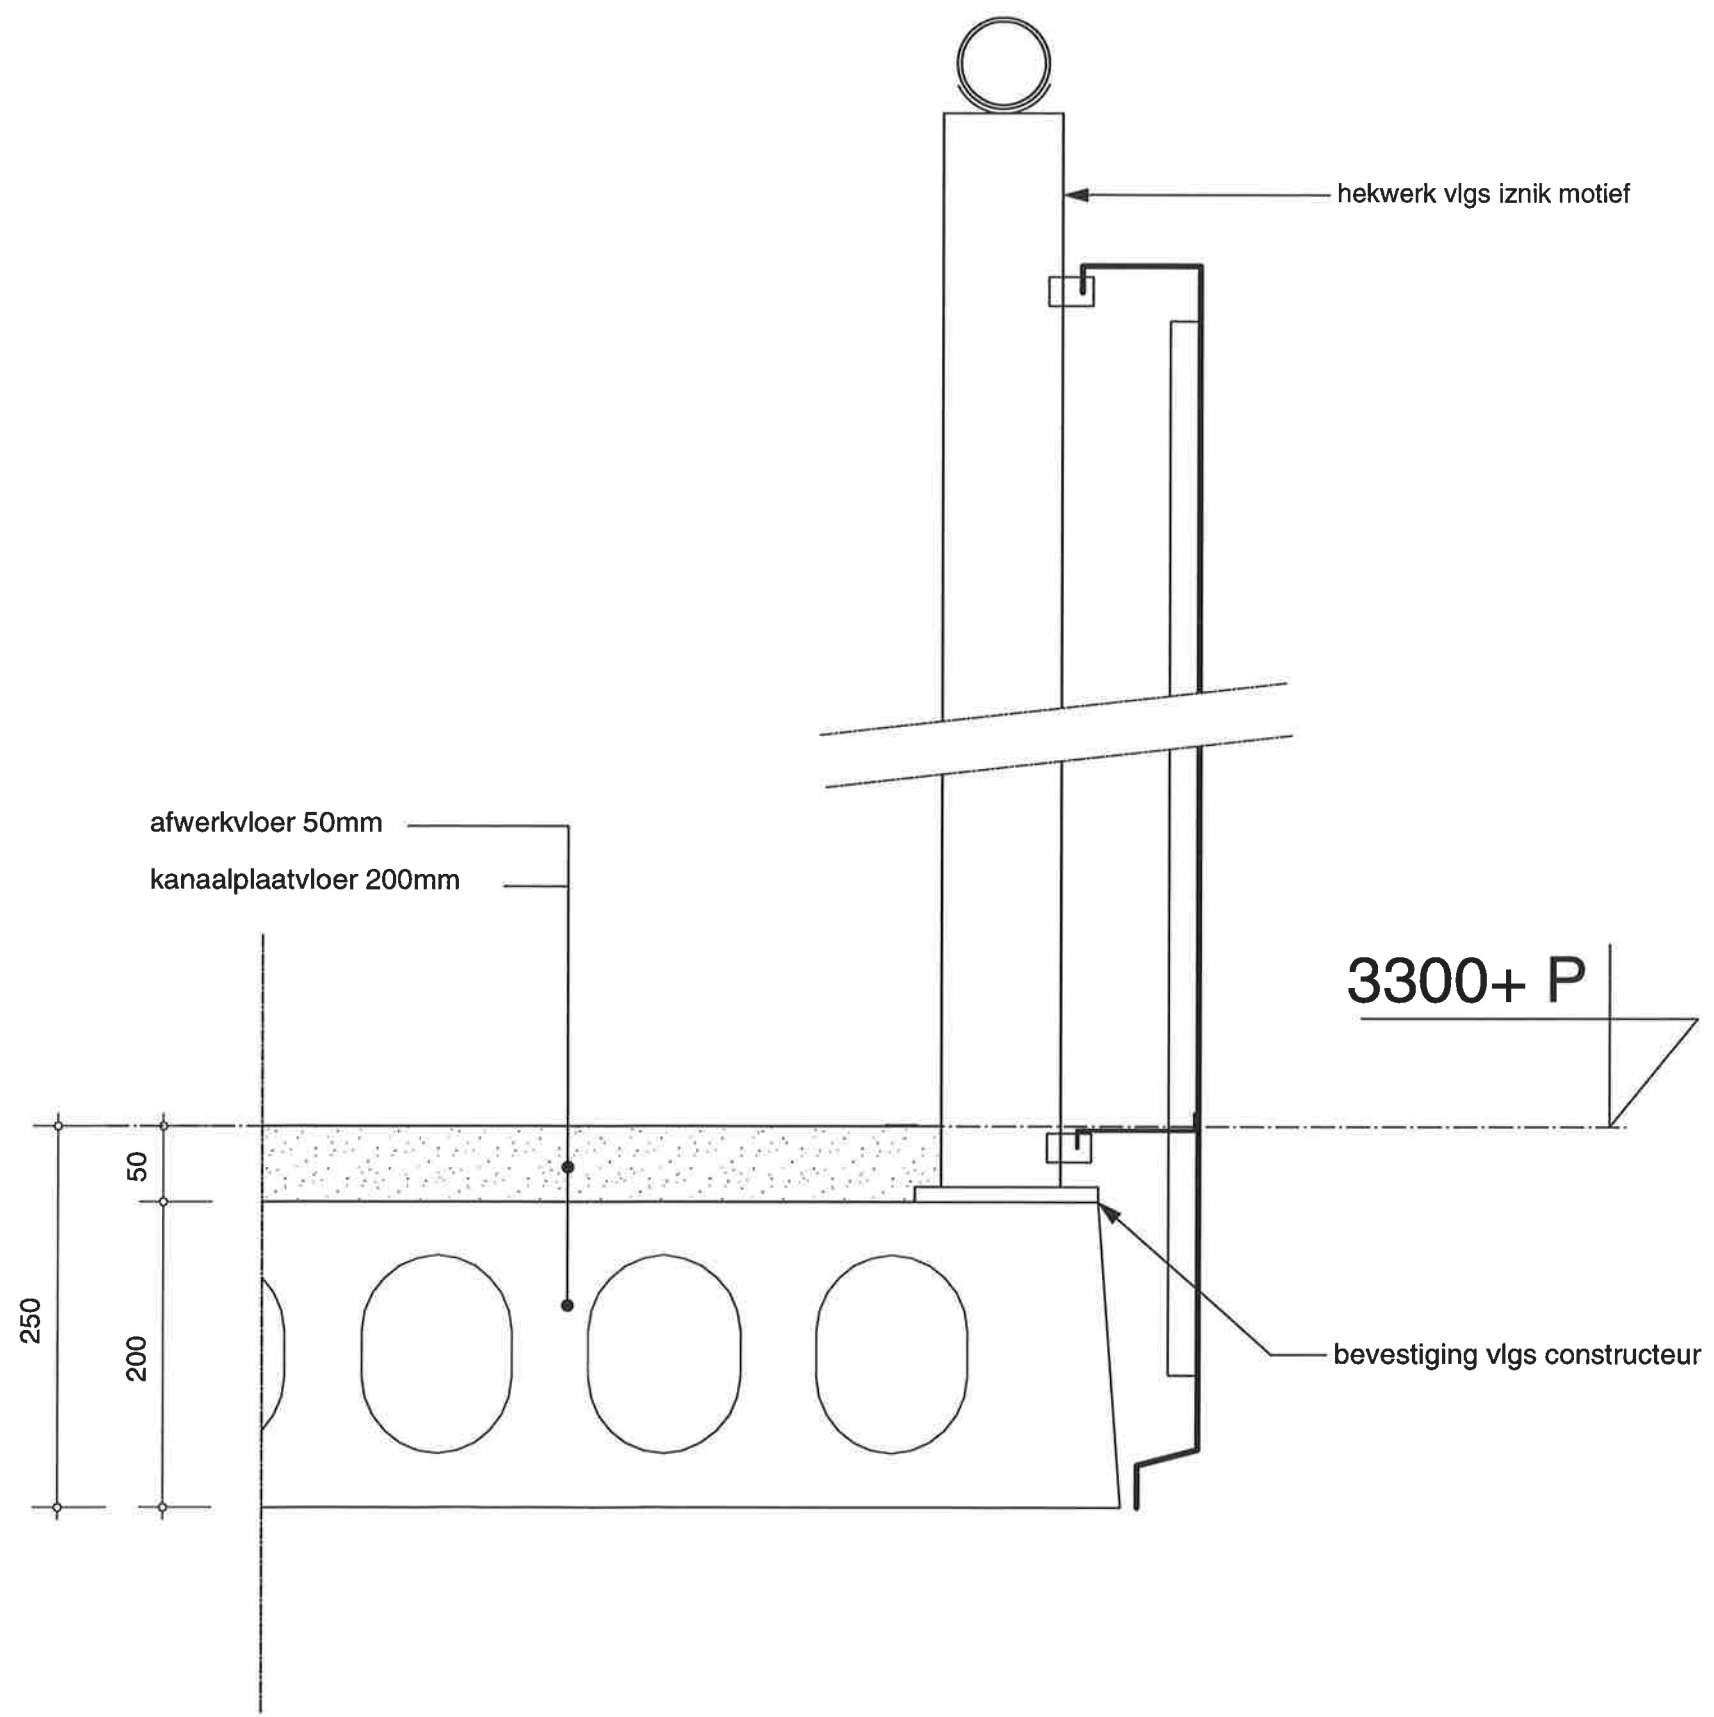


"Haci Bayram", Bunschoten/Spakenburg

datum: 03-03-2004
wiz :

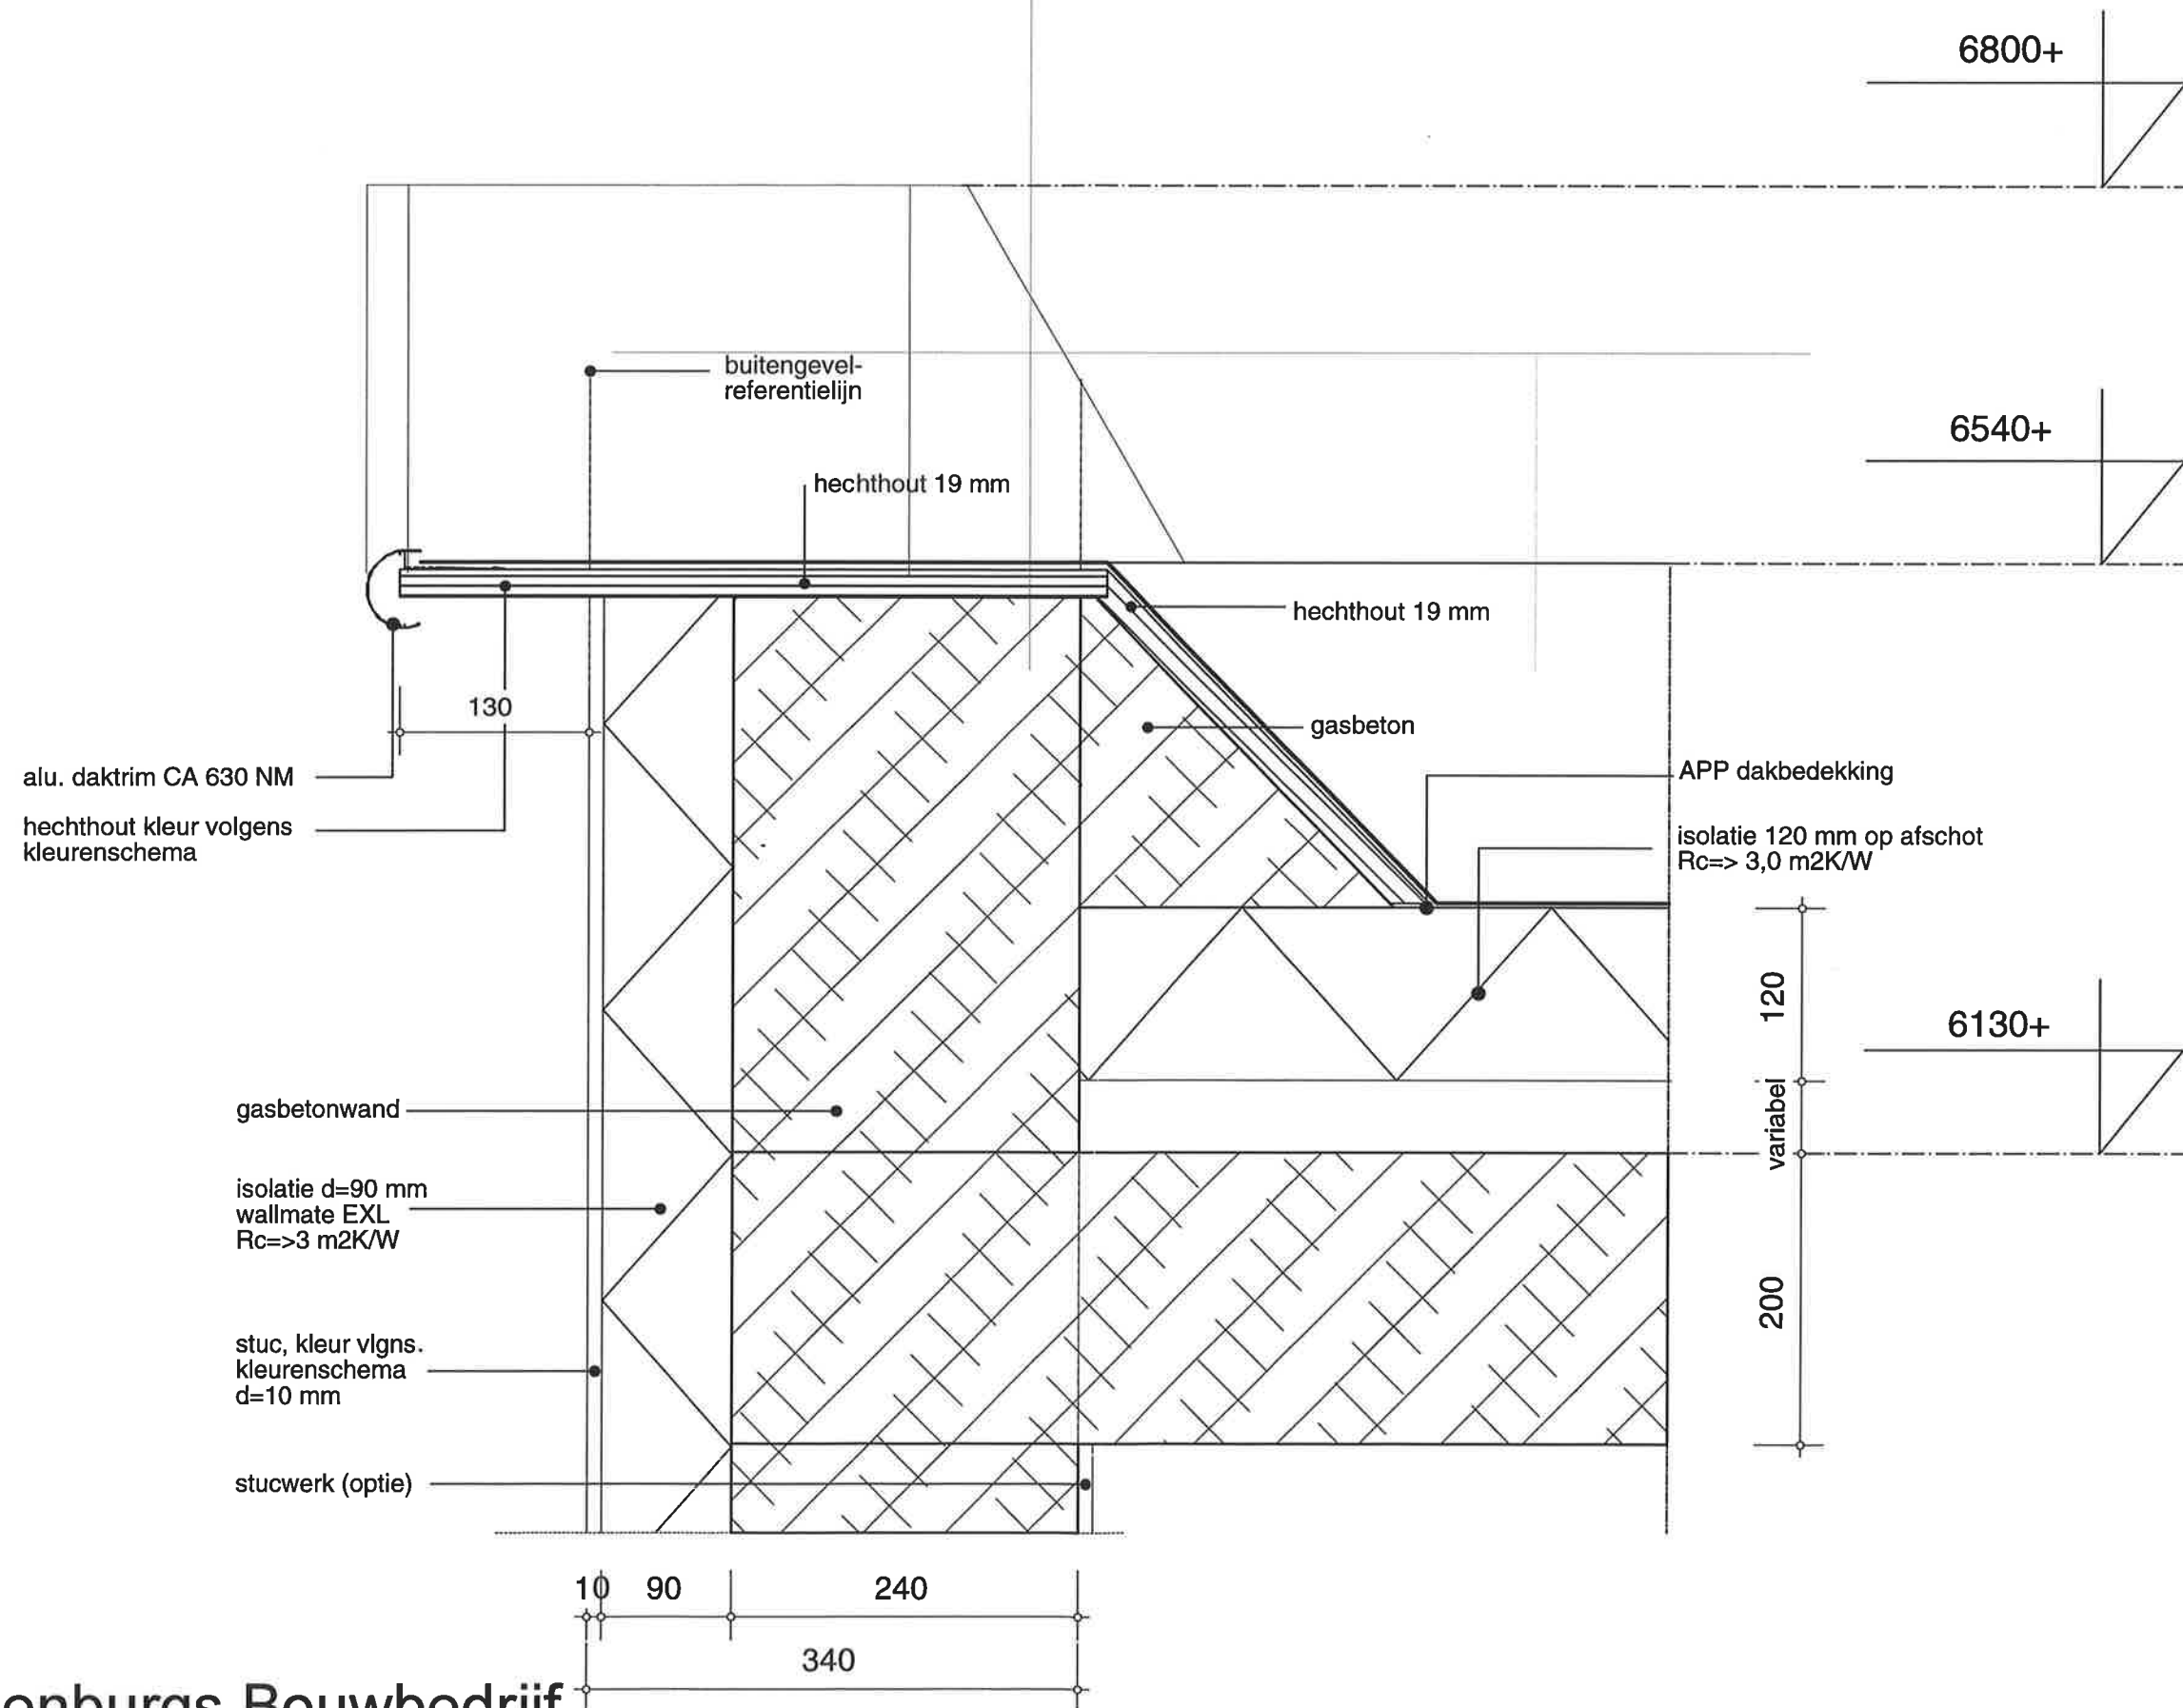

"Haci Bayram", Bunschoten/Spakenburg

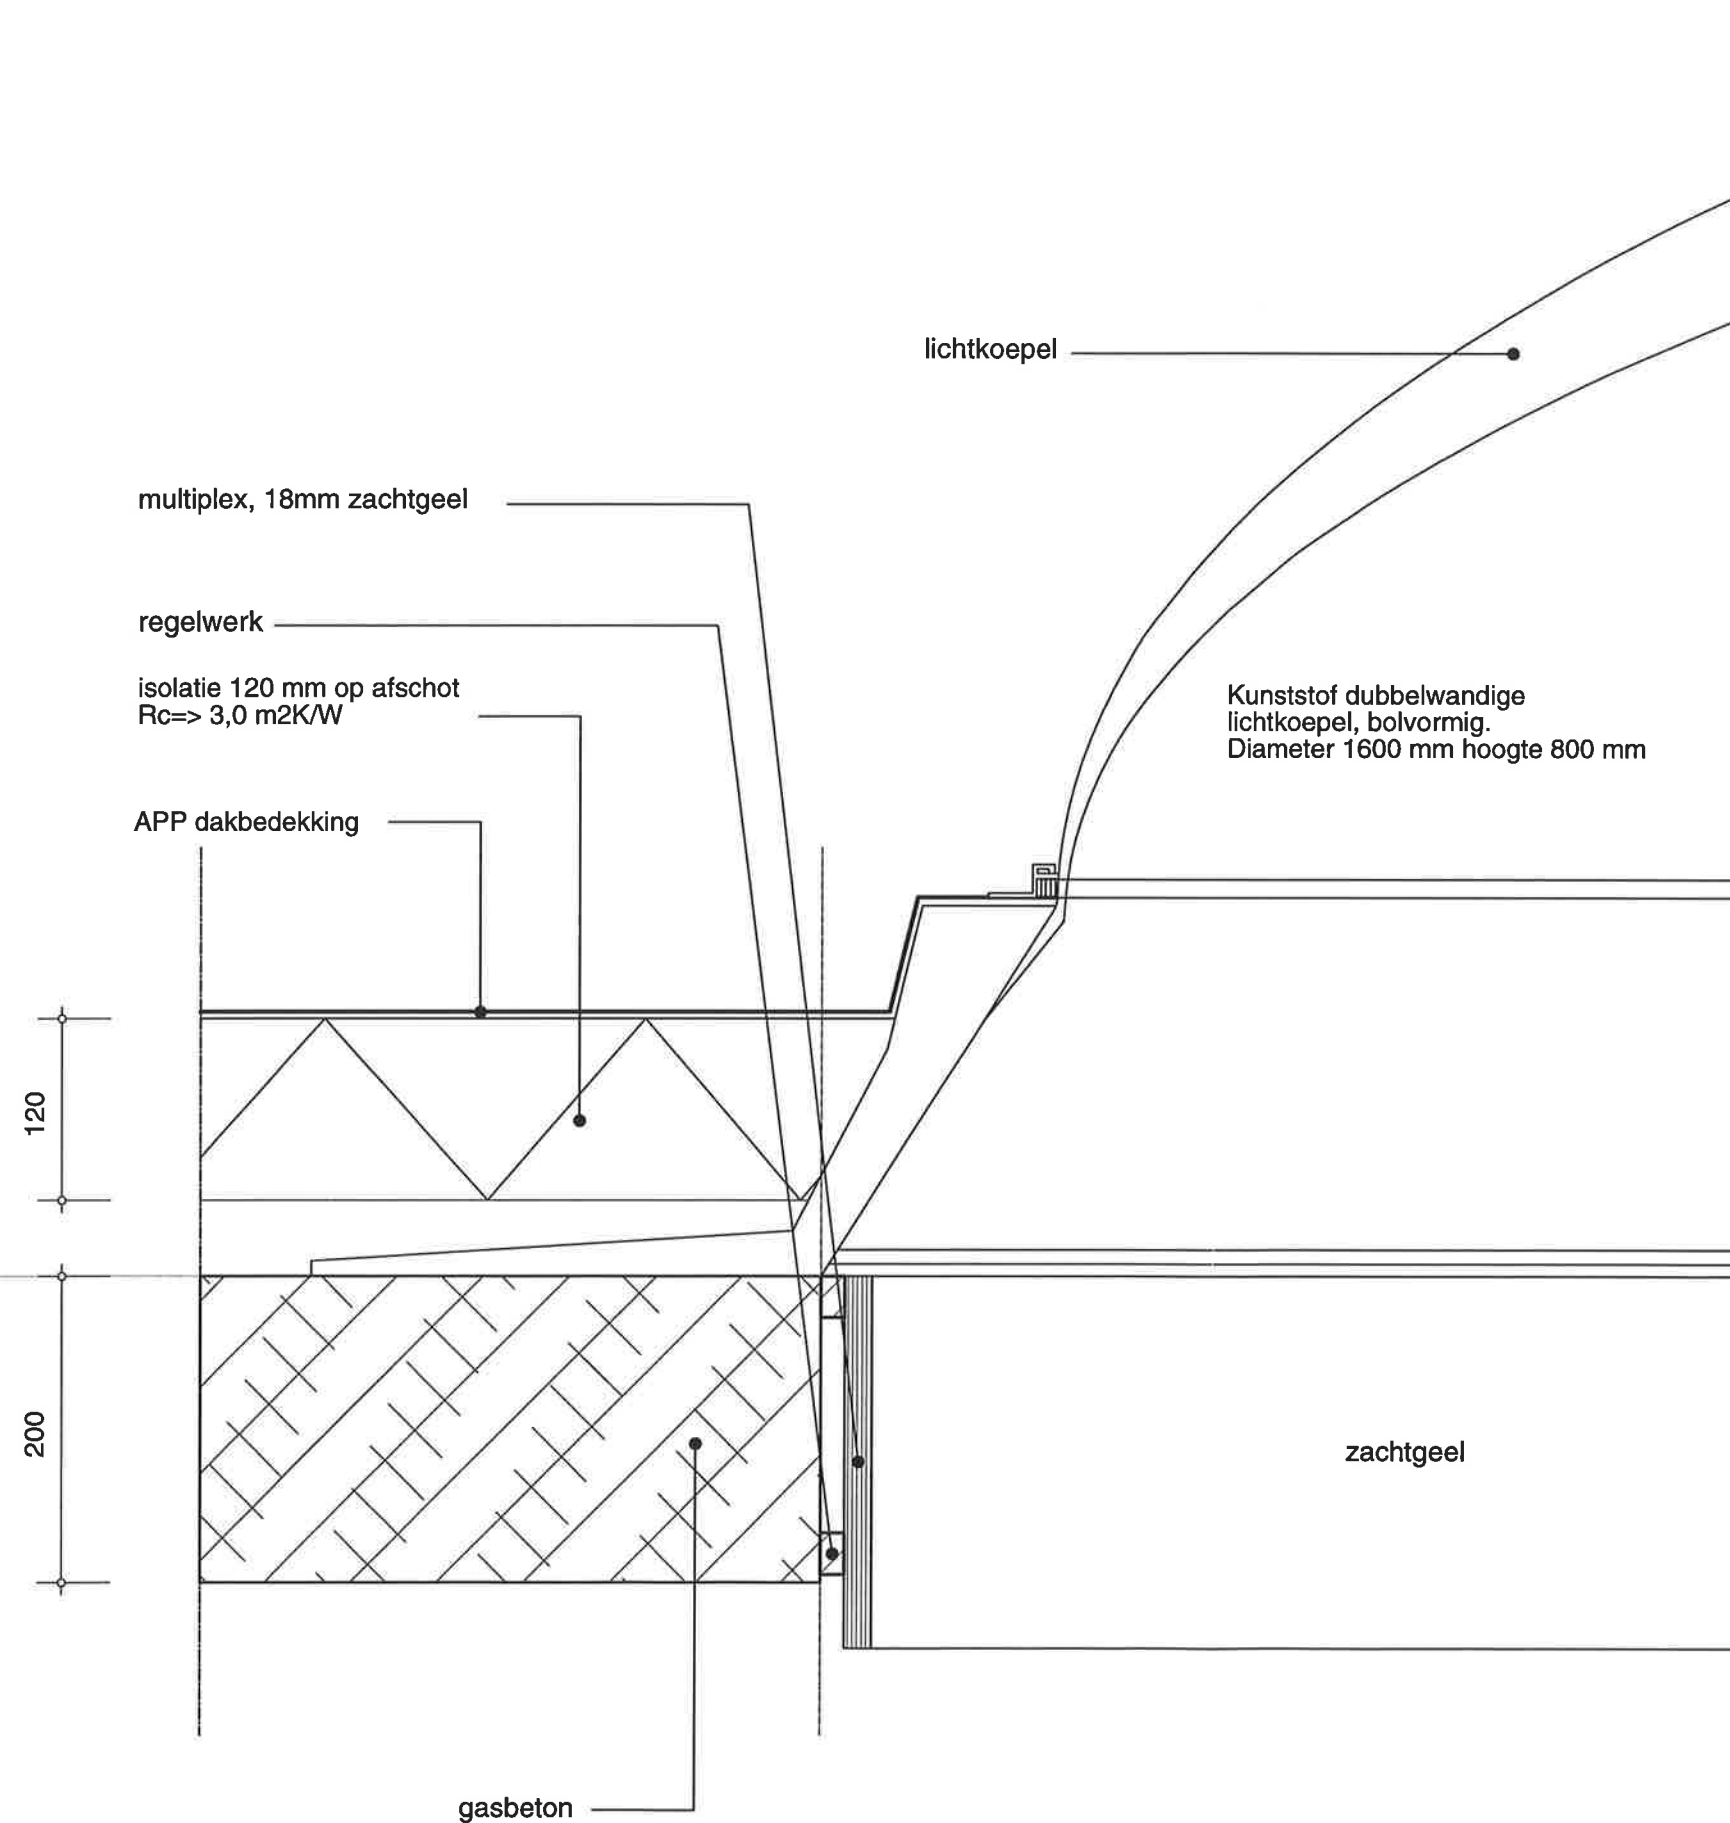

datum: 03-03-2004
wiz :

6130+

bk. dakvloer

-EPDM dakbedekking gelijmd
-Multiplex w.b.p. 12mm
-regelwerk
-staalprofiel
-regelwerk
-Multiplex w.b.p. 12mm

UNP-profiel
Gemoffelde daktrim
Compri CA 633 NM o.g.

5410+


V2.3

SBB Spakenburgs Bouwbedrijf

ir. Peter van Gerwen, architecten

"Haci Bayram", Bunschoten/Spakenburg

datum: 03-03-2004
wiz :

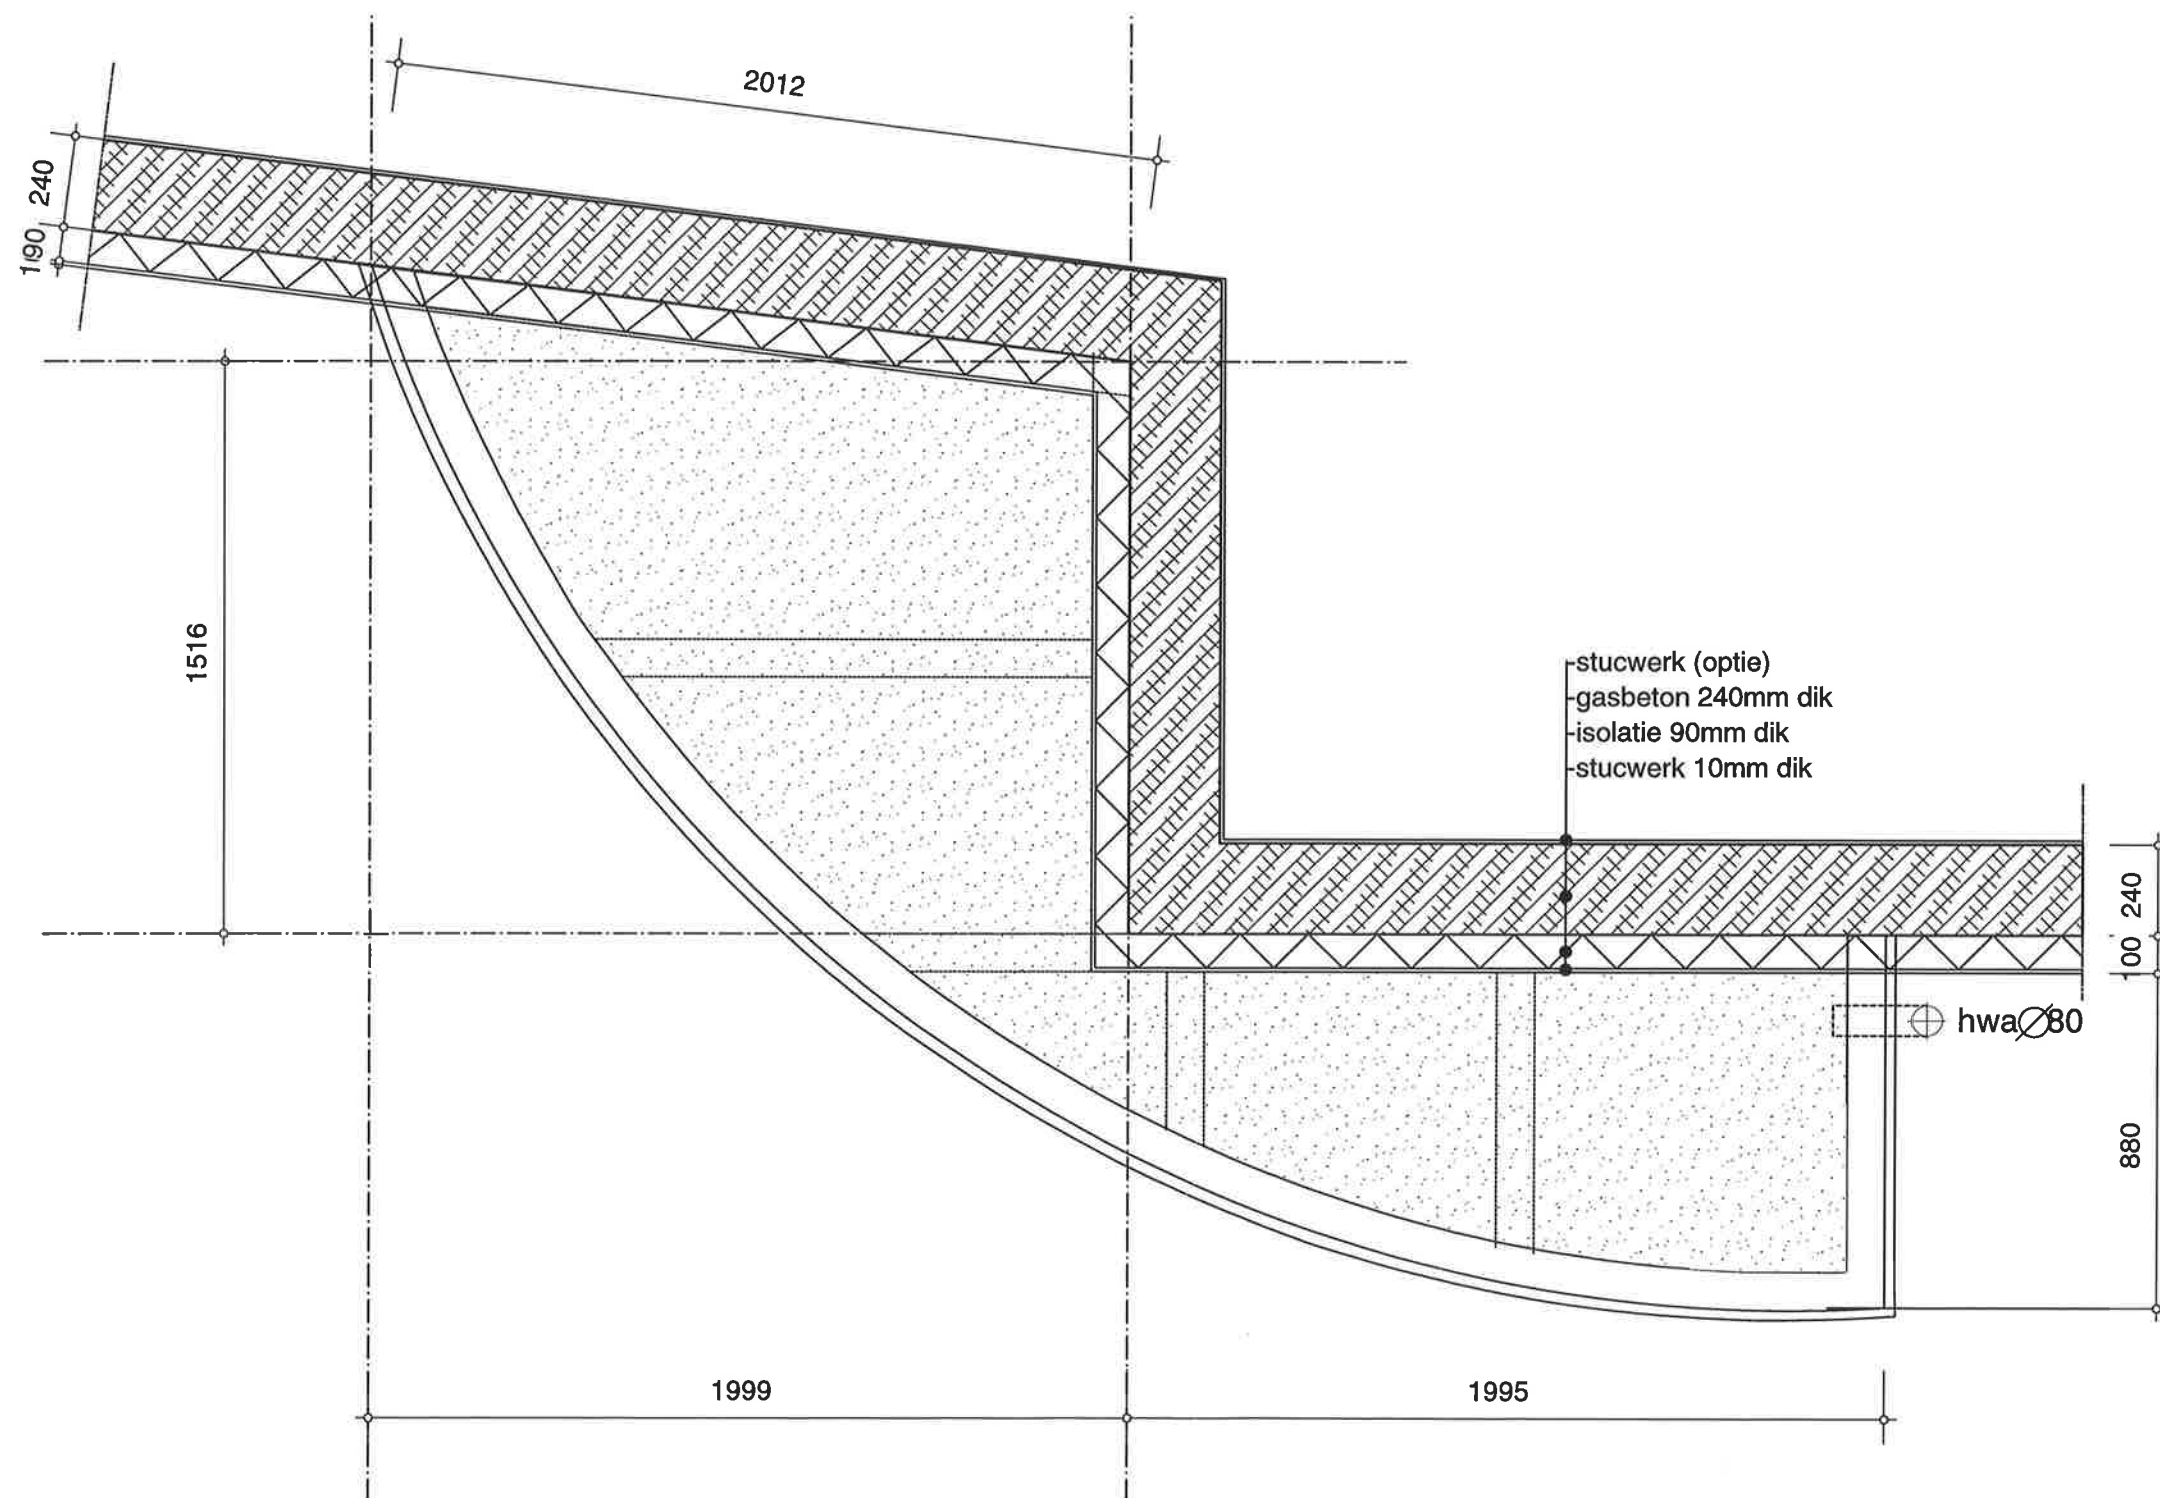

Bovenaanzicht luifel 1/10

